


FIRSTLÜFTERZIEGEL NR. 19 LÜ

Firstziegel: 2,8 Stck./lfm.


Firstanfangsziegel

Hauptwetterrichtung

Firstendziegel

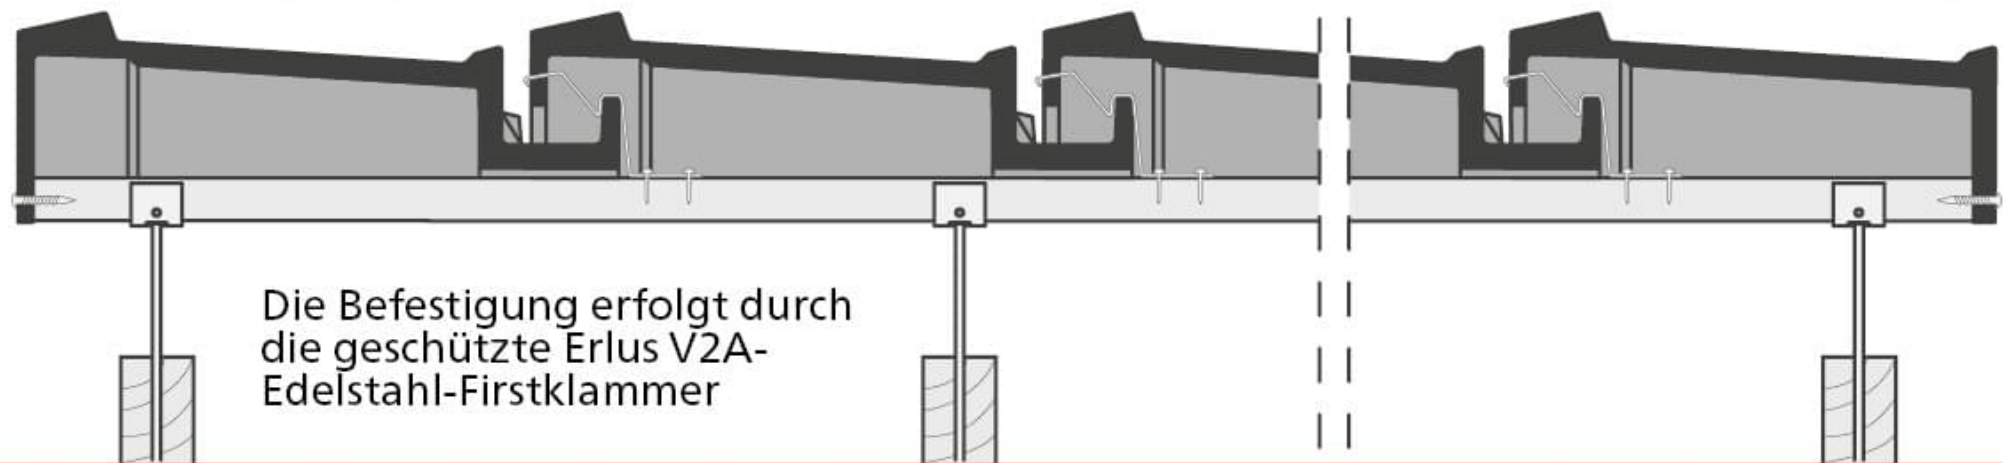


FIRSTLÜFTERZIEGEL NR. 19 LÜ MIT FIRSTANSCHLUSSZIEGEL

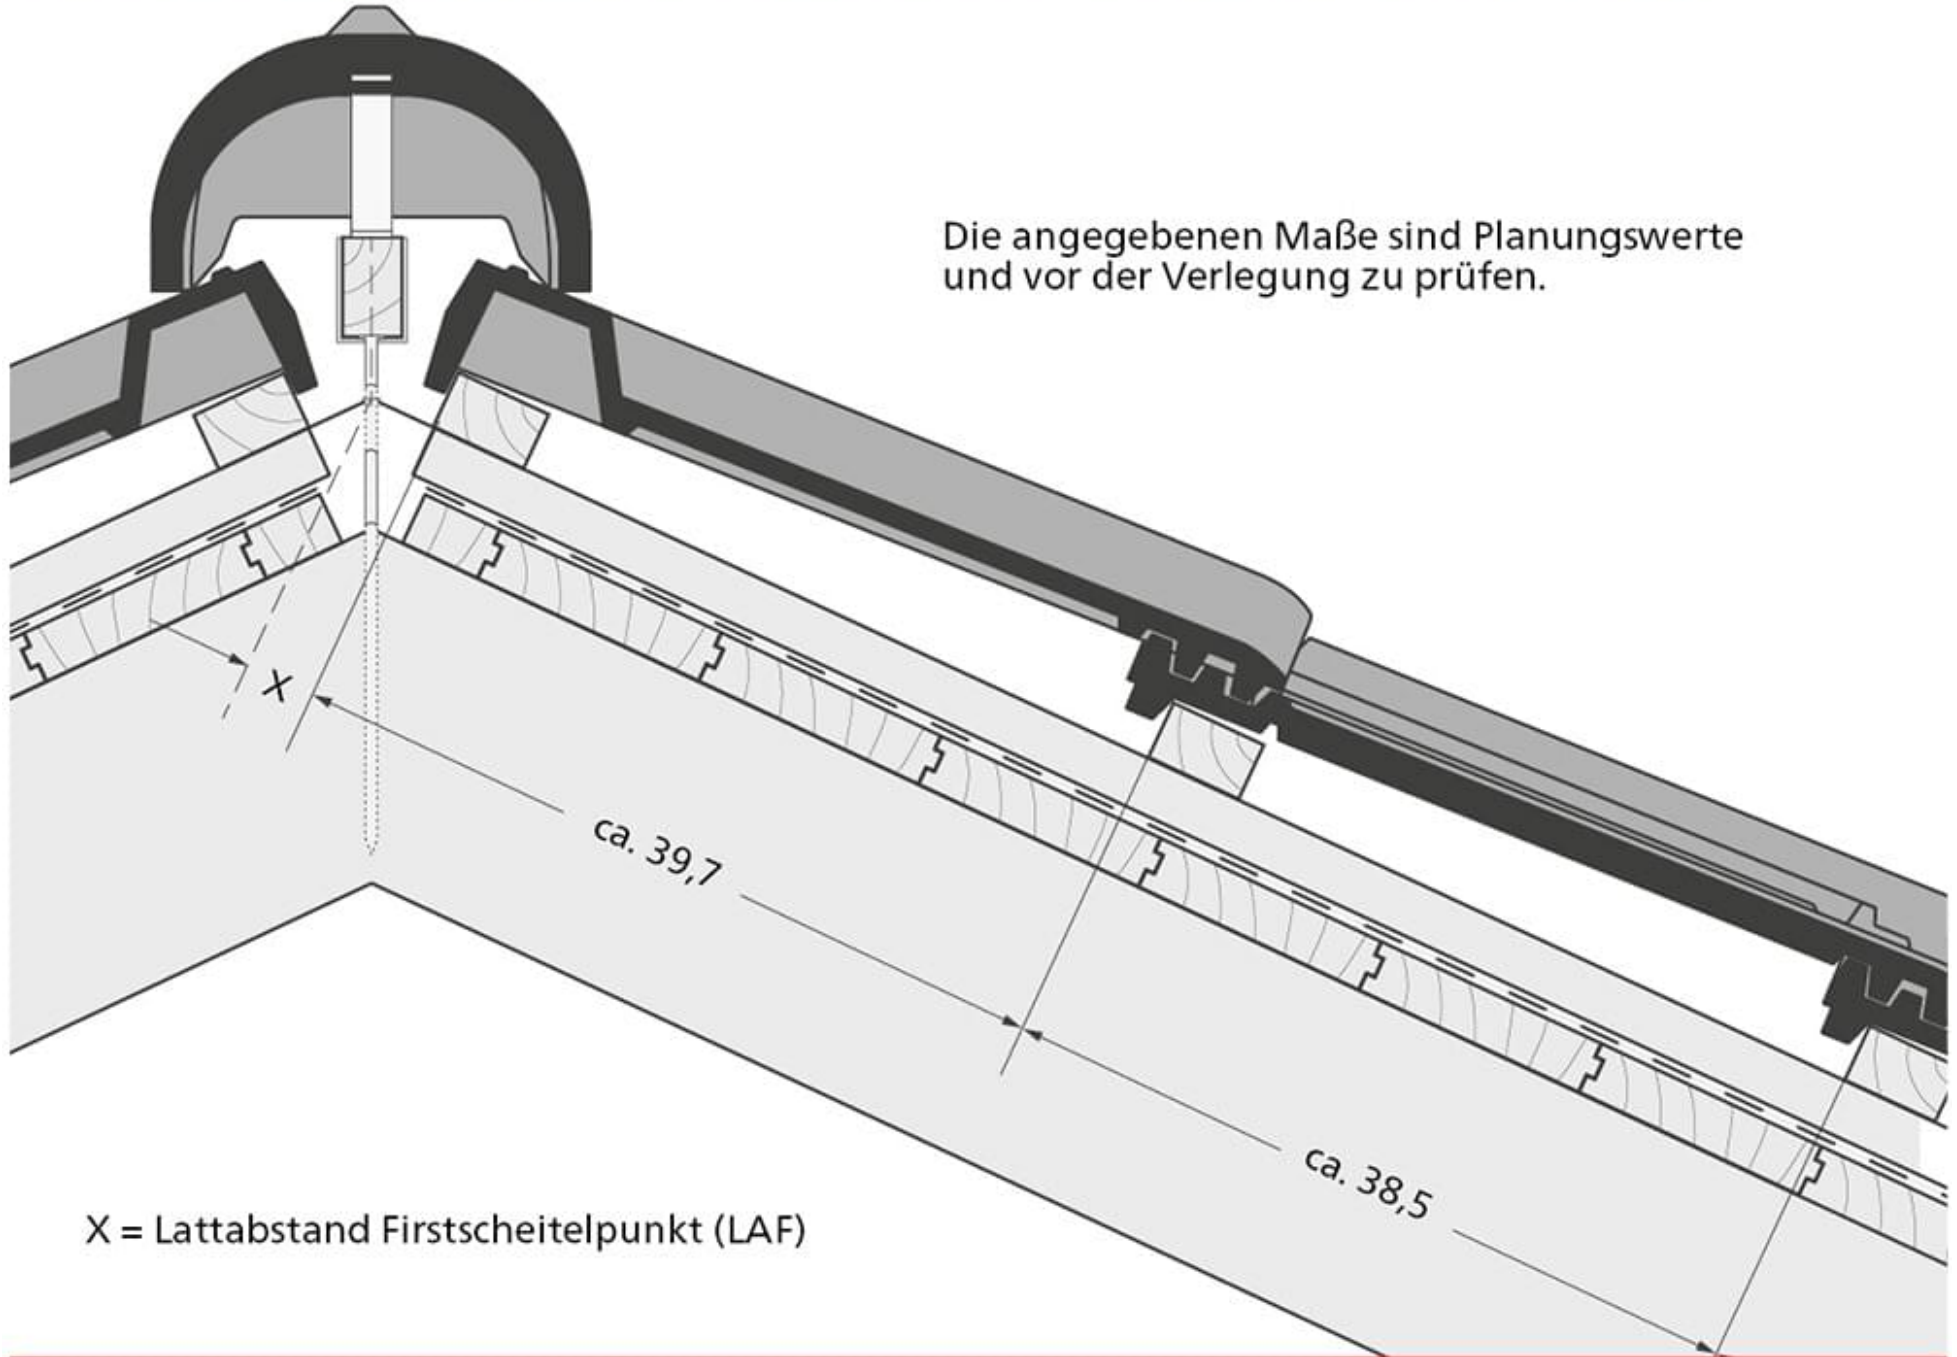


LINKER ORTGANG*

*bei flacher Dachneigung Verschraubungsloch im Ortgang dauerelastisch
(z. B. mit Spenglerschrauben) abdichten

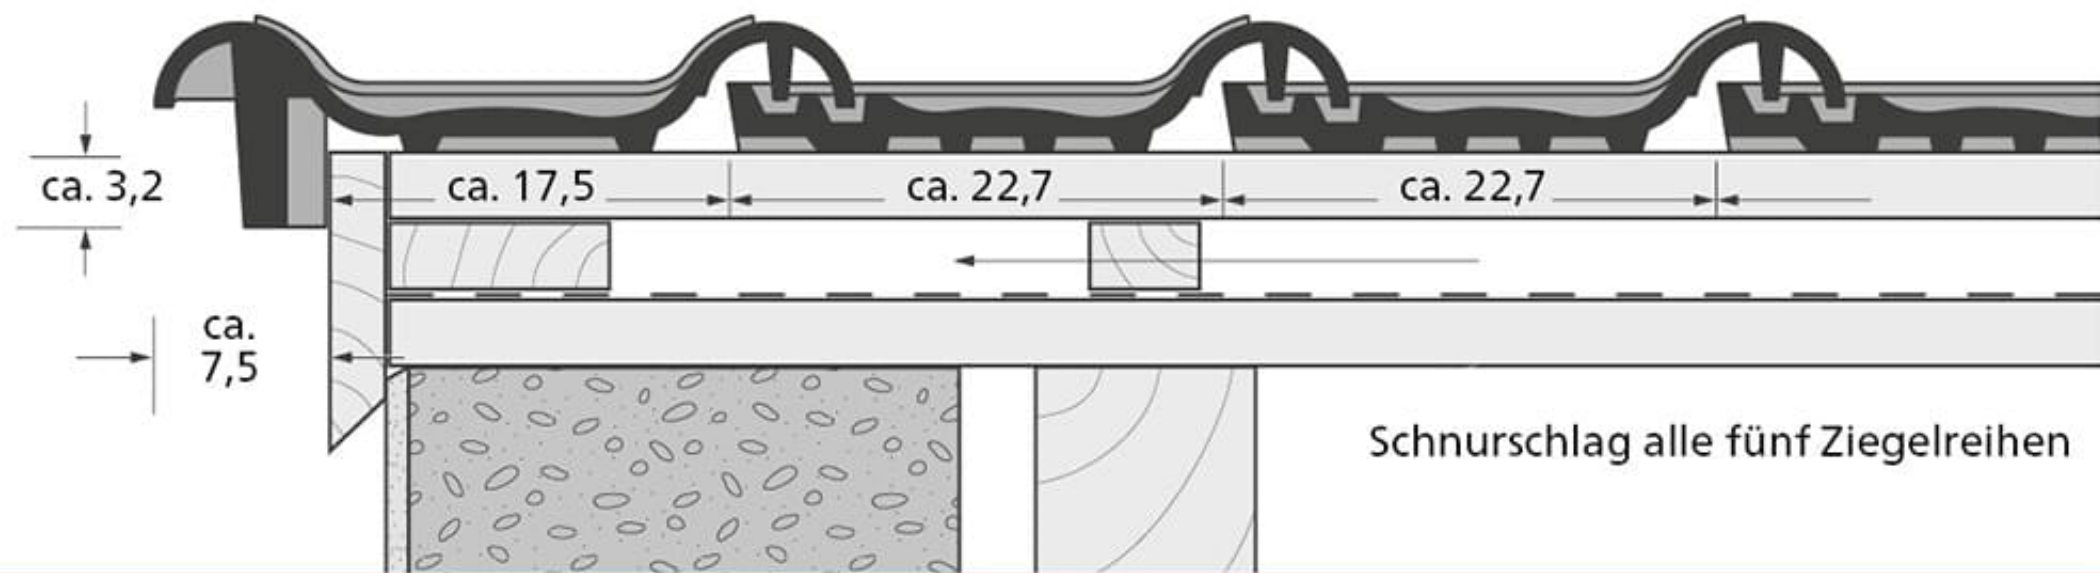


RECHTER ORTGANG*

*bei flacher Dachneigung Verschraubungsloch im Ortgang dauerelastisch
(z. B. mit Spenglerschrauben) abdichten

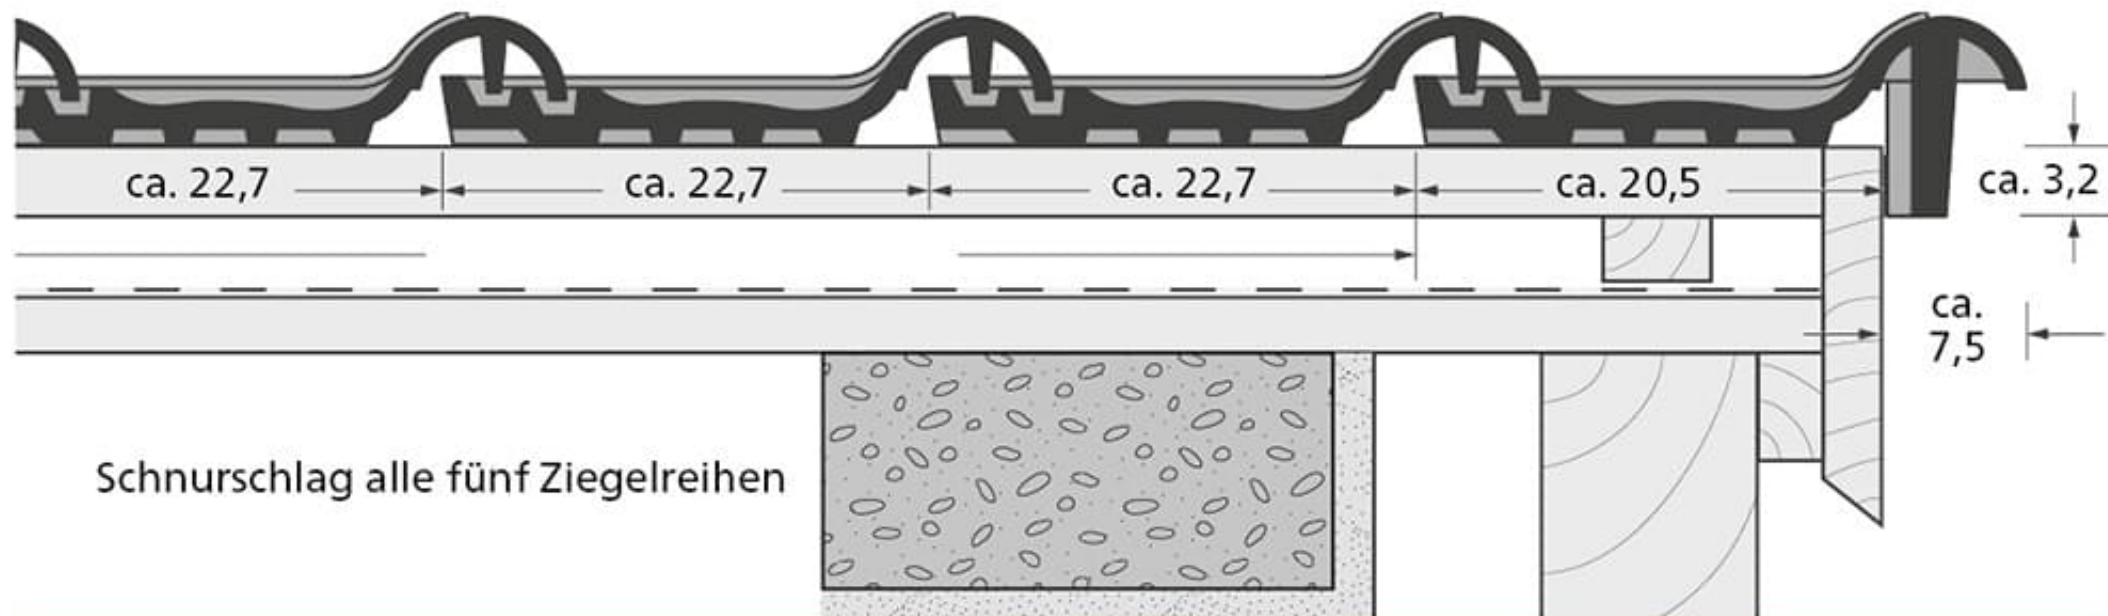


PULTDACH

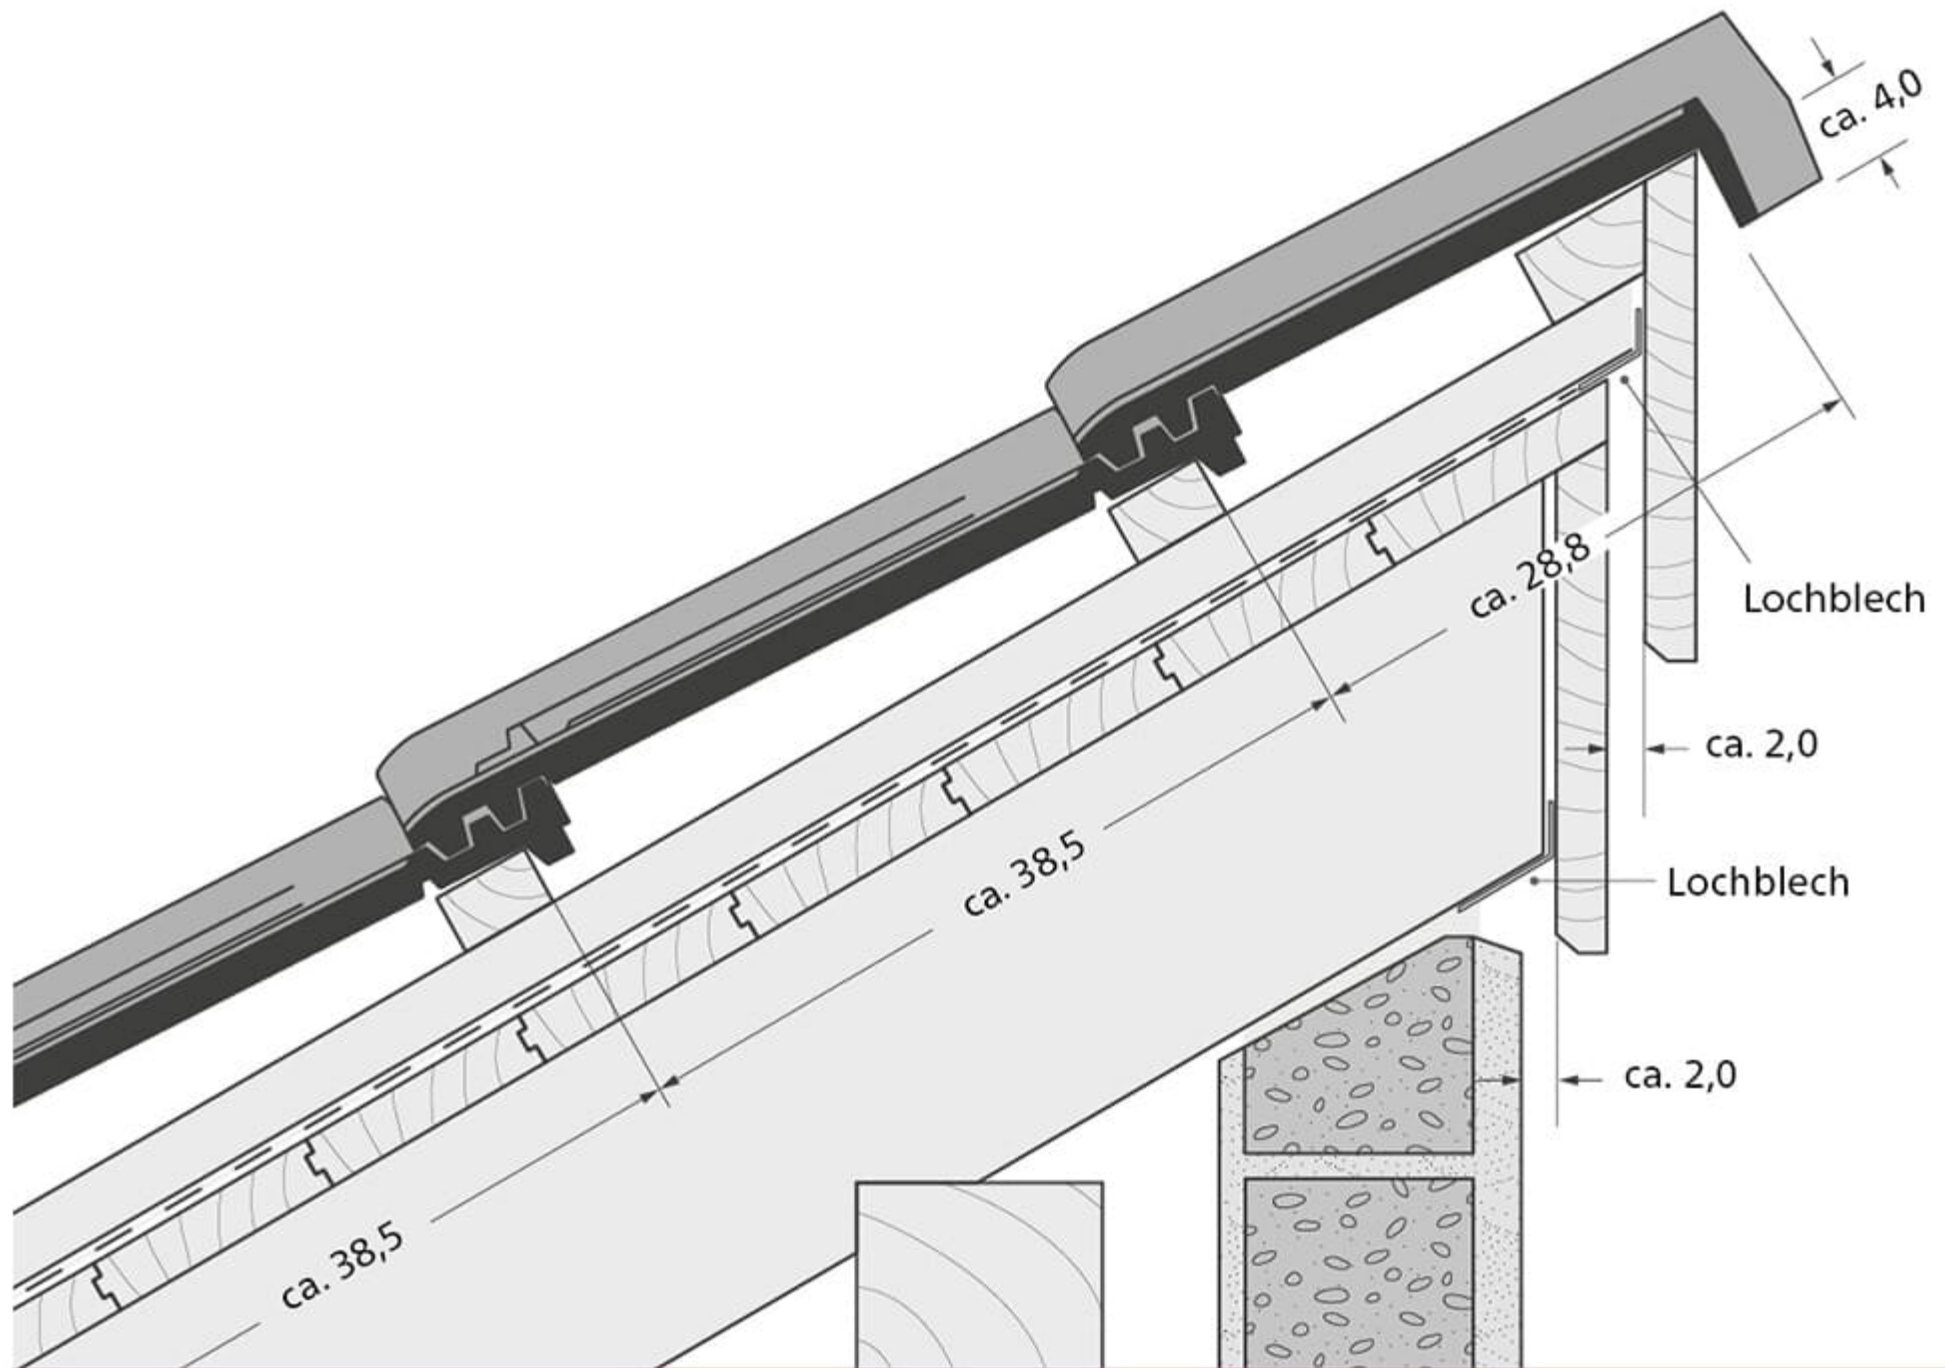


TRAUFE MIT AUFSPARRENDÄMMUNG

ERLUS empfiehlt den Einsatz eines Traufbleches.

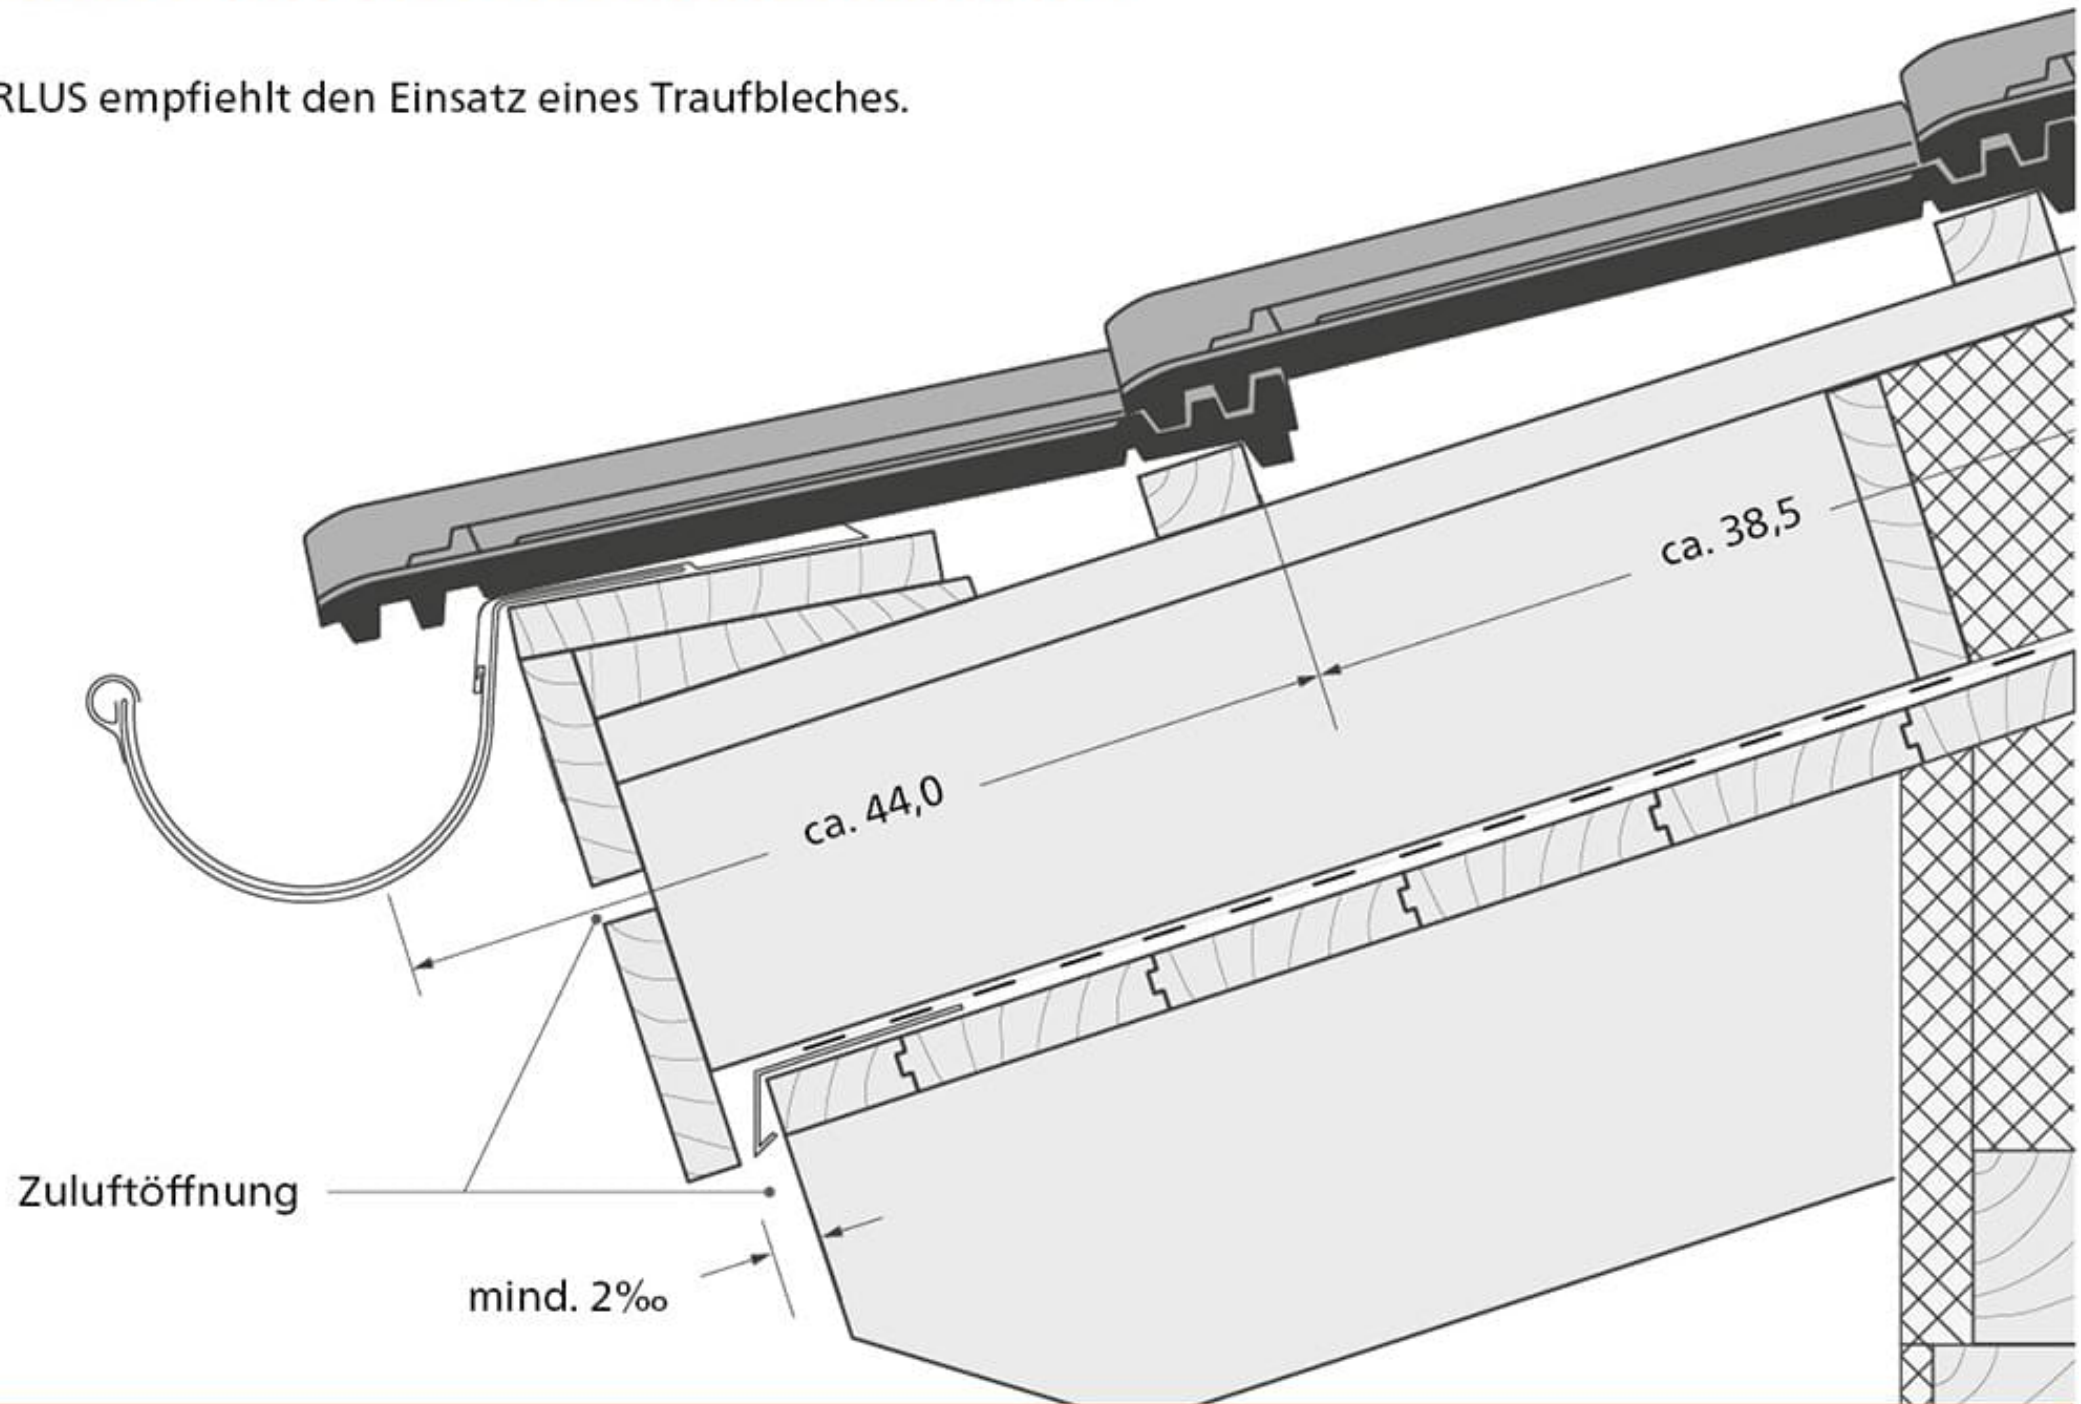

ERLUS Dachbegehungssystem

LATTWEITE > 37,5 cm

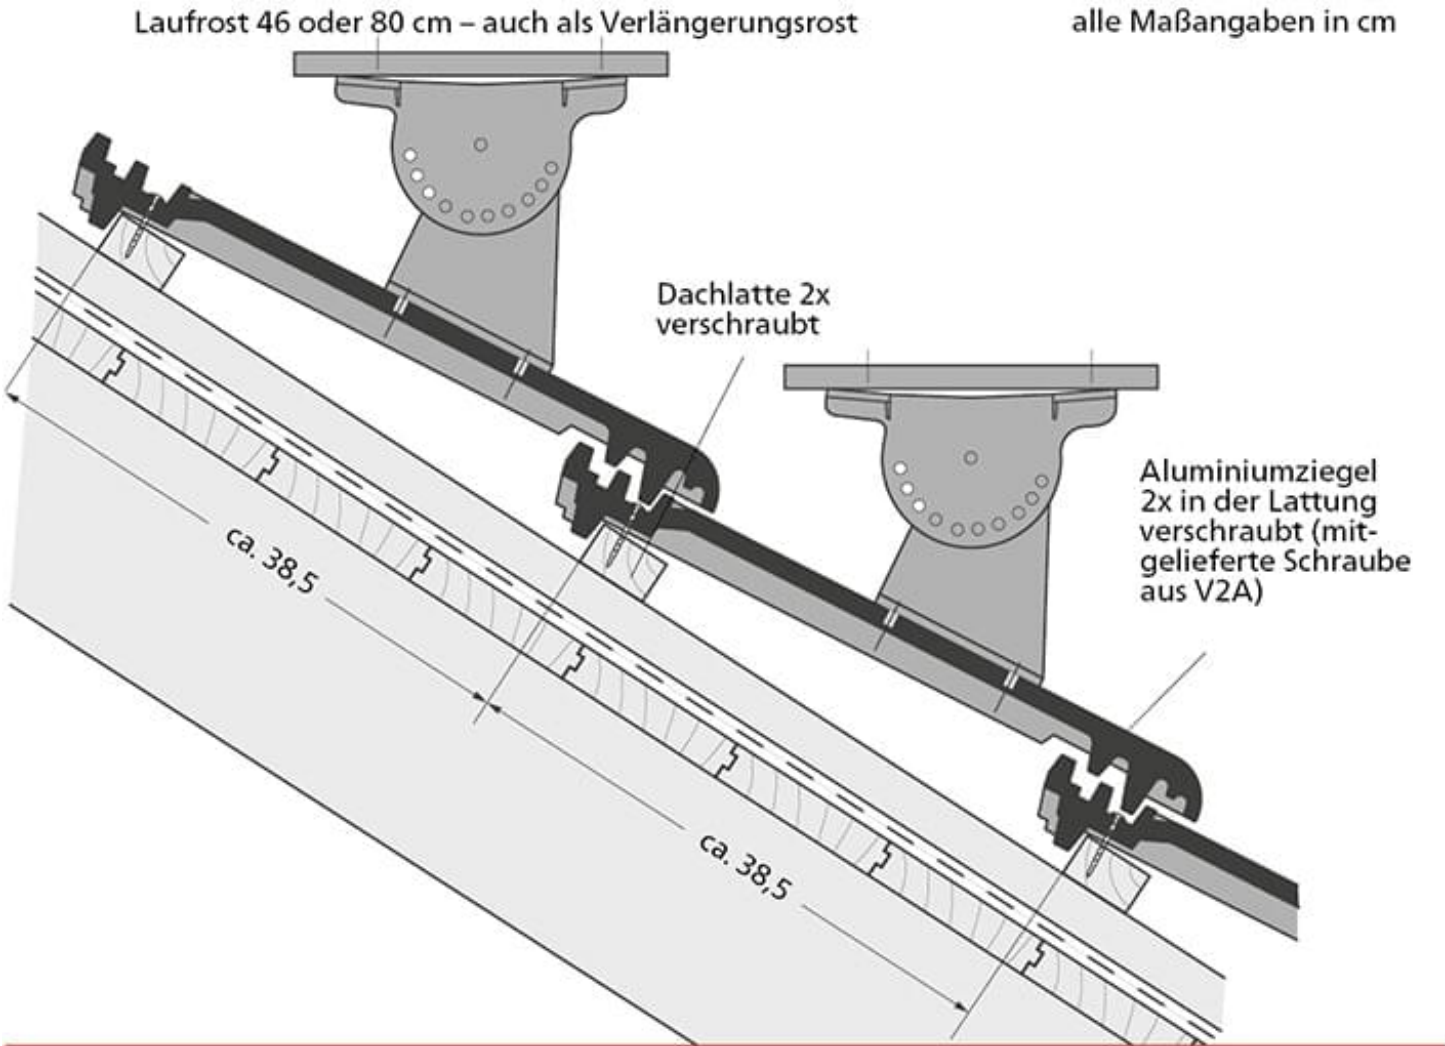

VERARBEITUNG VON TRITTFLÄCHEN UND ROSTEN NACH DIN 18160-5

Zeichnung: Linea

ARTIKEL	≤ 45°	≥ 45°
Trittflächen (Roste 46 cm)	jede Ziegelreihe	jede Ziegelreihe
Einzeltritt (Steigtritt)	jede Ziegelreihe	jede Ziegelreihe

aus nicht rostendem Stahl/Alu, geprüft nach DIN EN 516,
keine Stützlaten erforderlich