


ERLUS Dachbegehungssystem

LATTWEITE > 37,5 cm

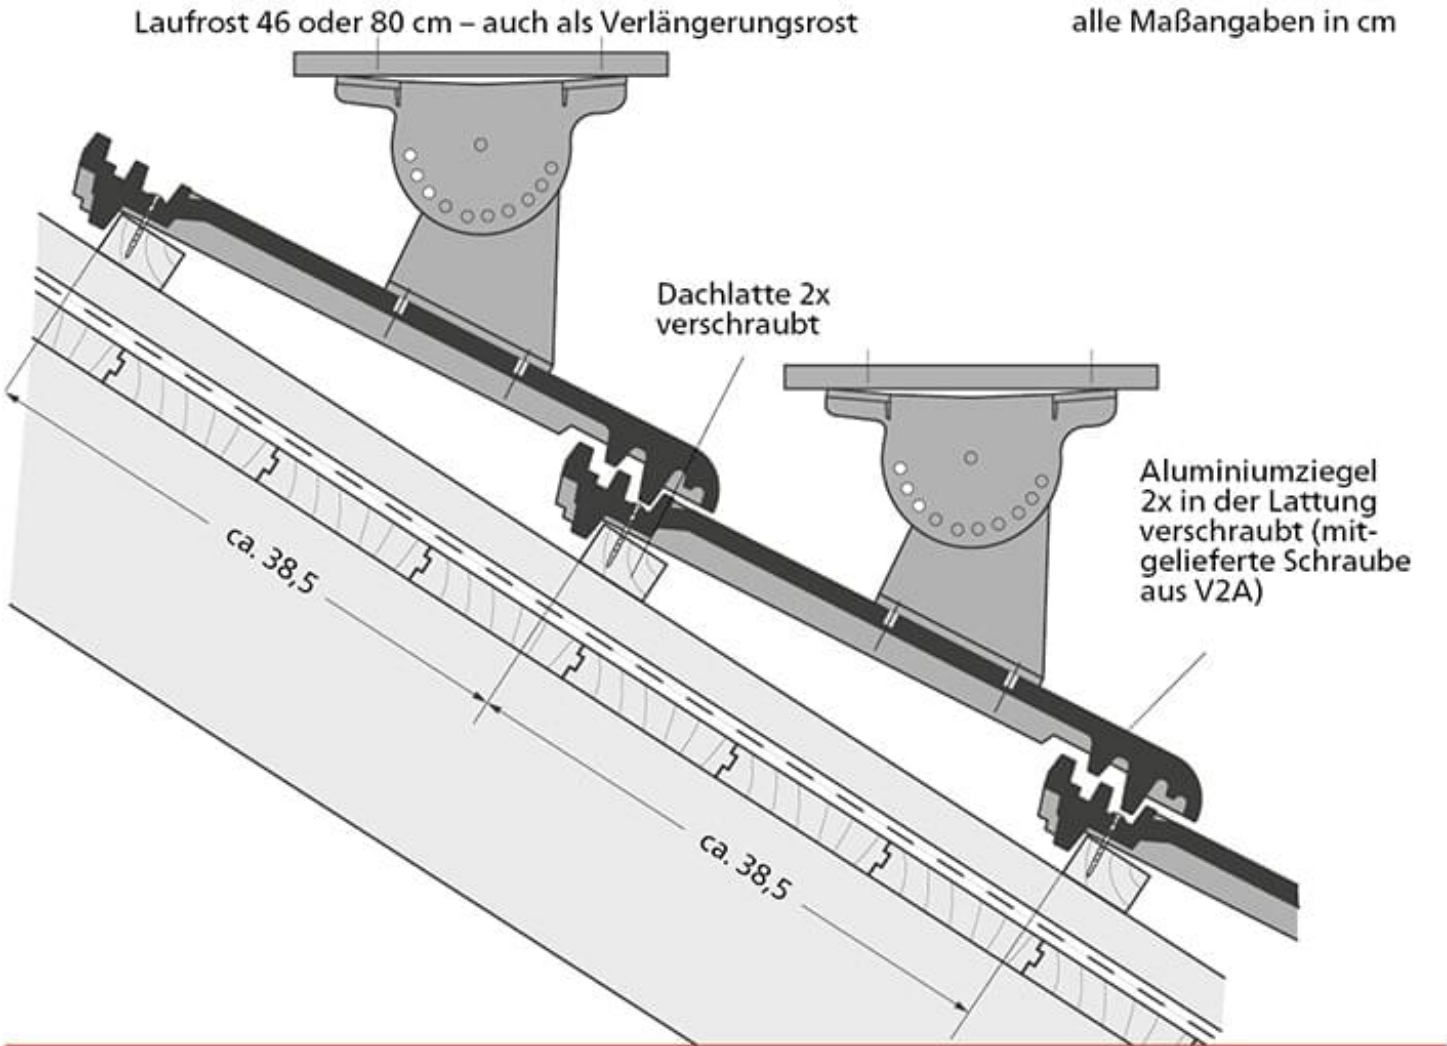


VERARBEITUNG VON TRITTFLÄCHEN UND ROSTEN NACH DIN 18160-5

Zeichnung: Linea

ARTIKEL	≤ 45°	≥ 45°
Trittflächen (Roste 46 cm)	jede Ziegelreihe	jede Ziegelreihe
Einzeltritt (Steigtritt)	jede Ziegelreihe	jede Ziegelreihe

aus nicht rostendem Stahl/Alu, geprüft nach DIN EN 516,
keine Stützlaten erforderlich

FIRSTZIEGEL NR. 15 MIT FIRSTANSCHLUSSZIEGEL

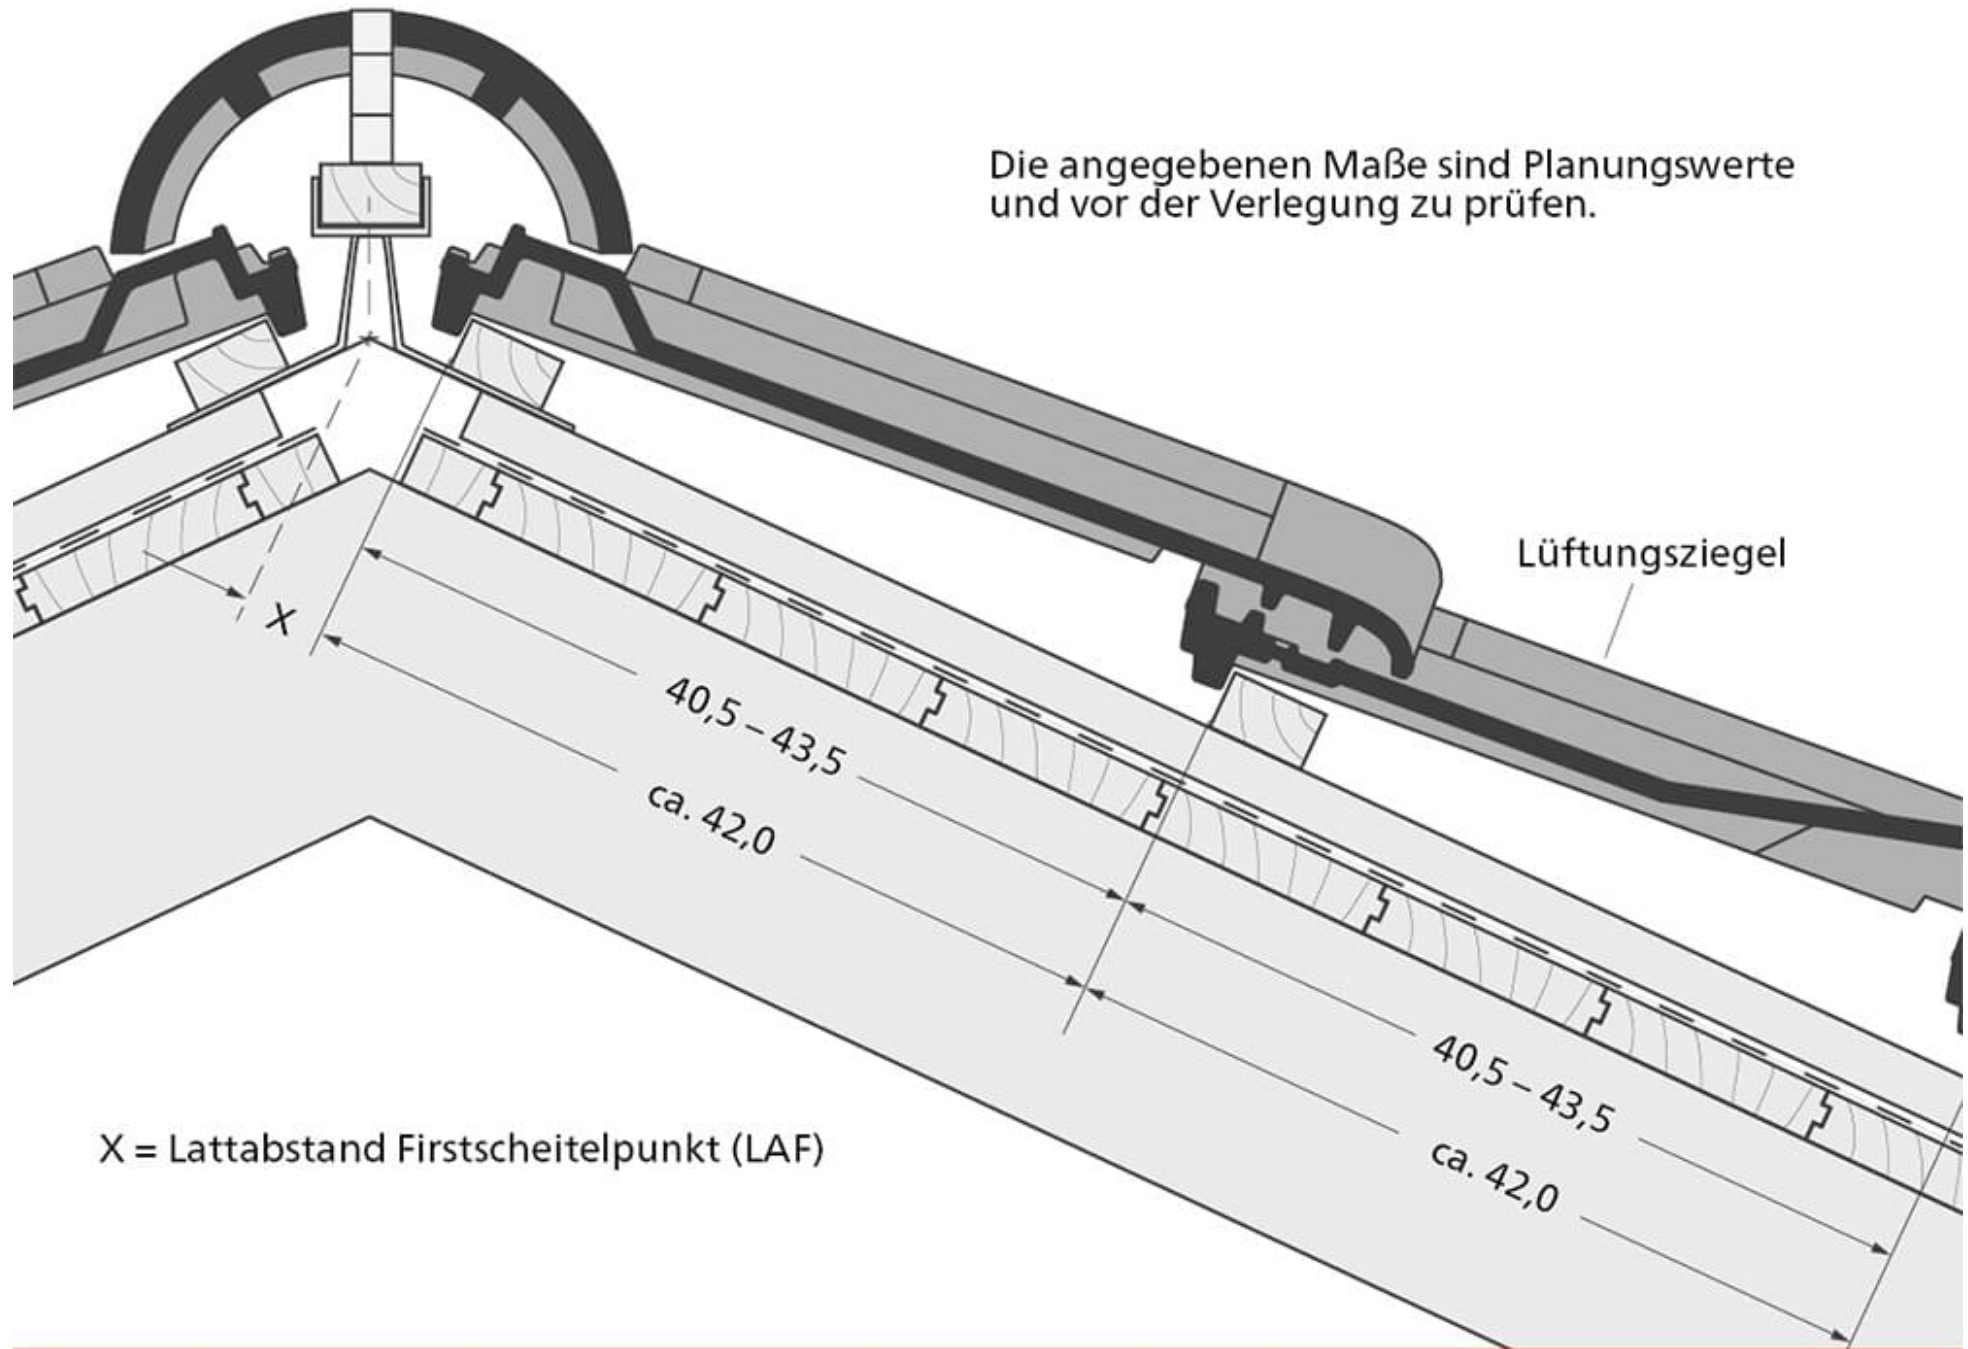


FIRSTLÜFTERZIEGEL NR. 19 LÜ

Firstziegel: 2,8 Stck./lfm.


Firstanfangsziegel

Hauptwetterrichtung

Firstendziegel

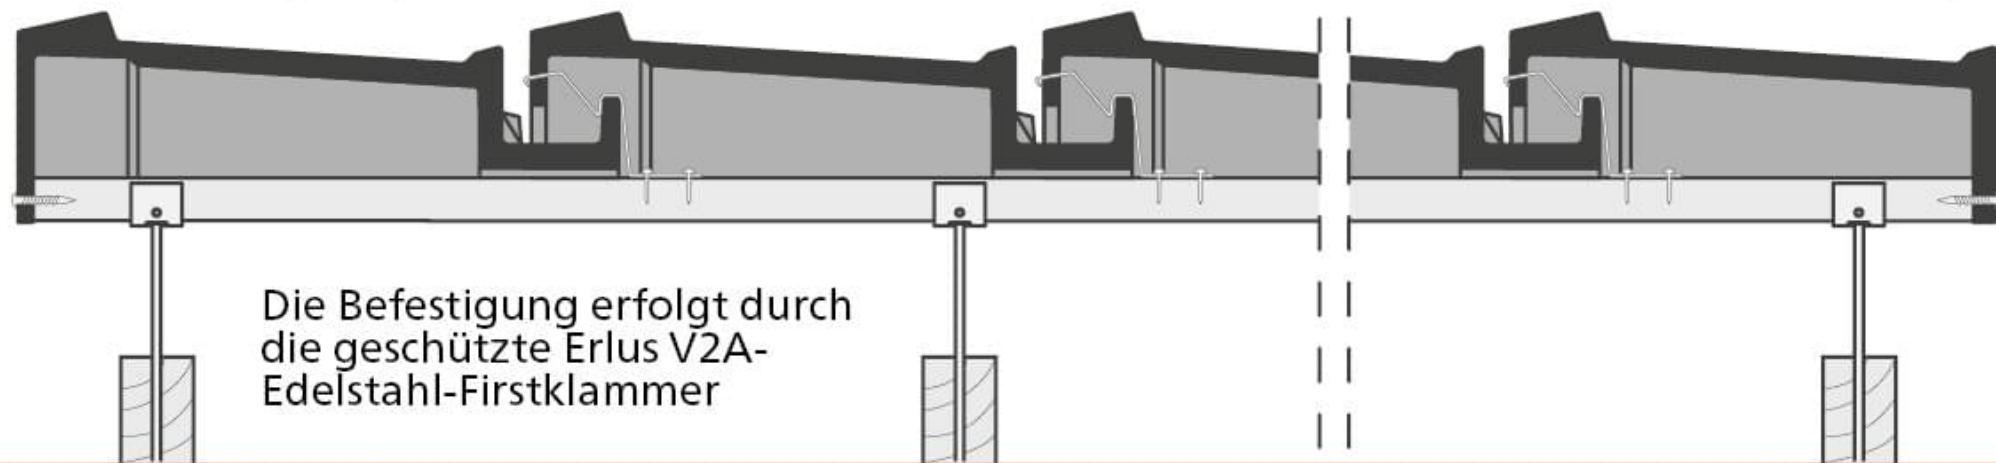


FIRSTZIEGEL NR. 15

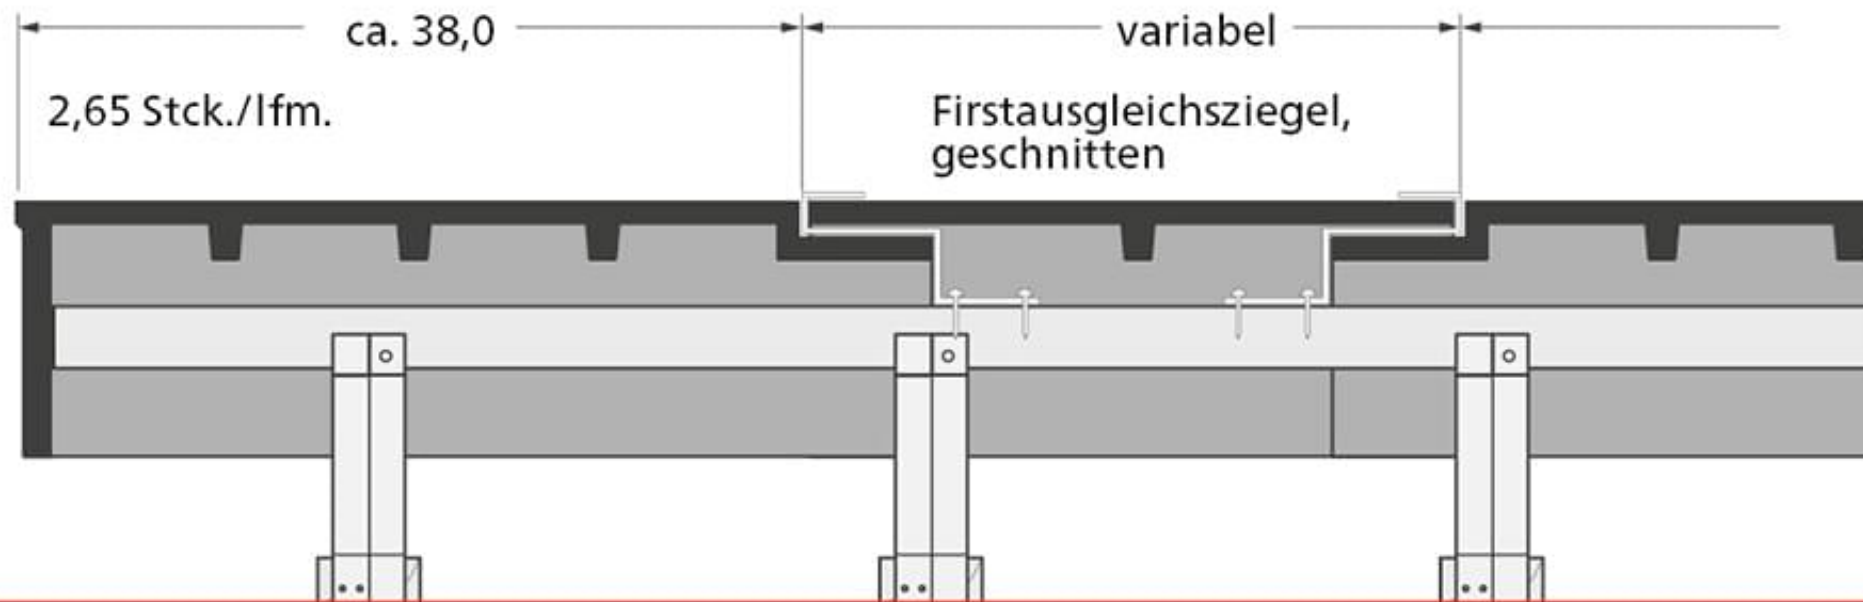


LINKER ORTGANG*

*bei flacher Dachneigung Verschraubungsloch im Ortgang dauerelastisch
(z. B. mit Spenglerschrauben) abdichten

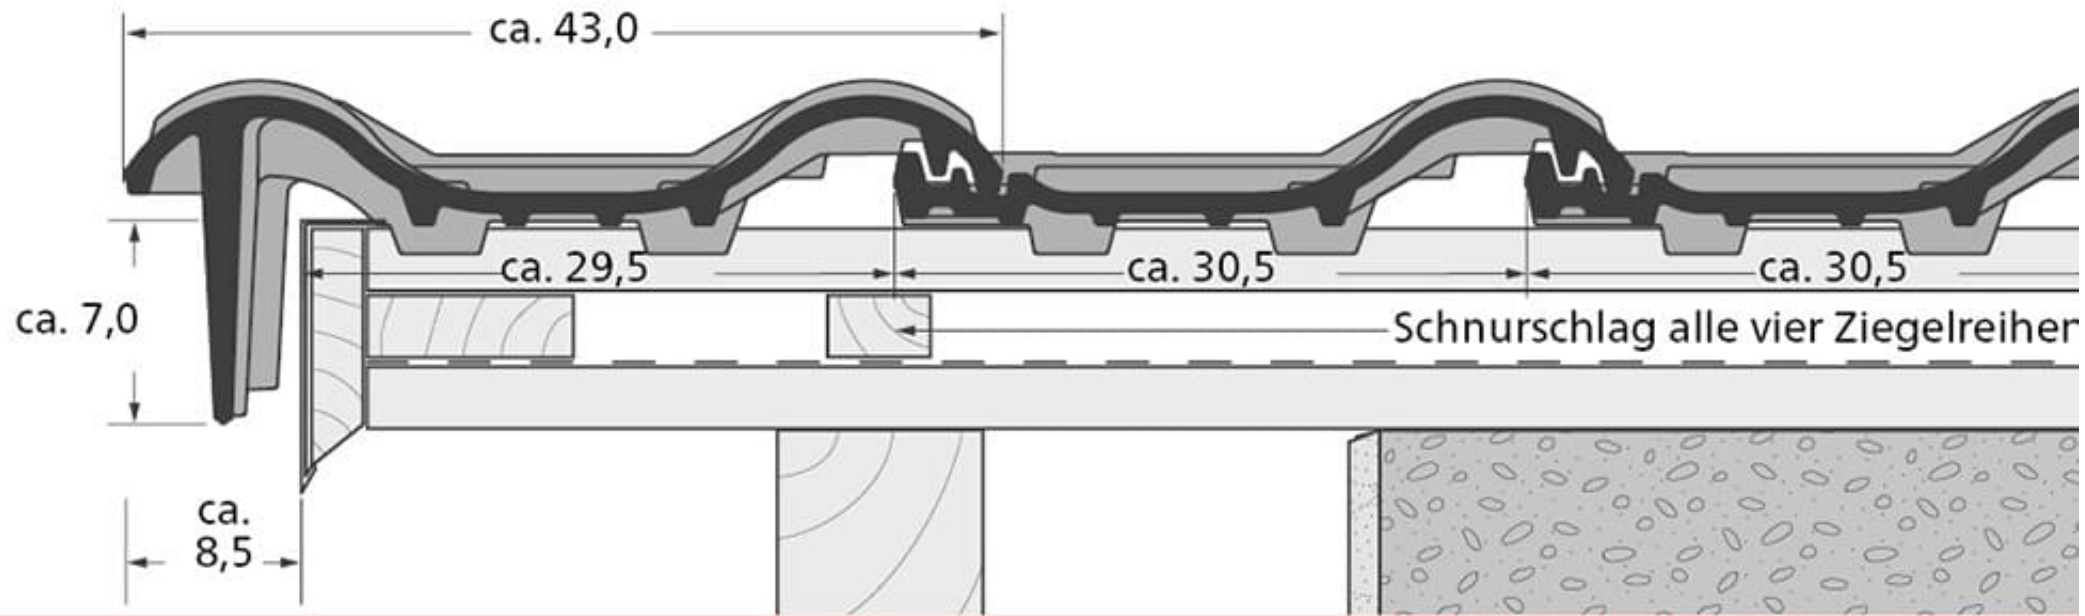


RECHTER ORTGANG*

*bei flacher Dachneigung Verschraubungsloch im Ortgang dauerelastisch
(z. B. mit Spenglerschrauben) abdichten

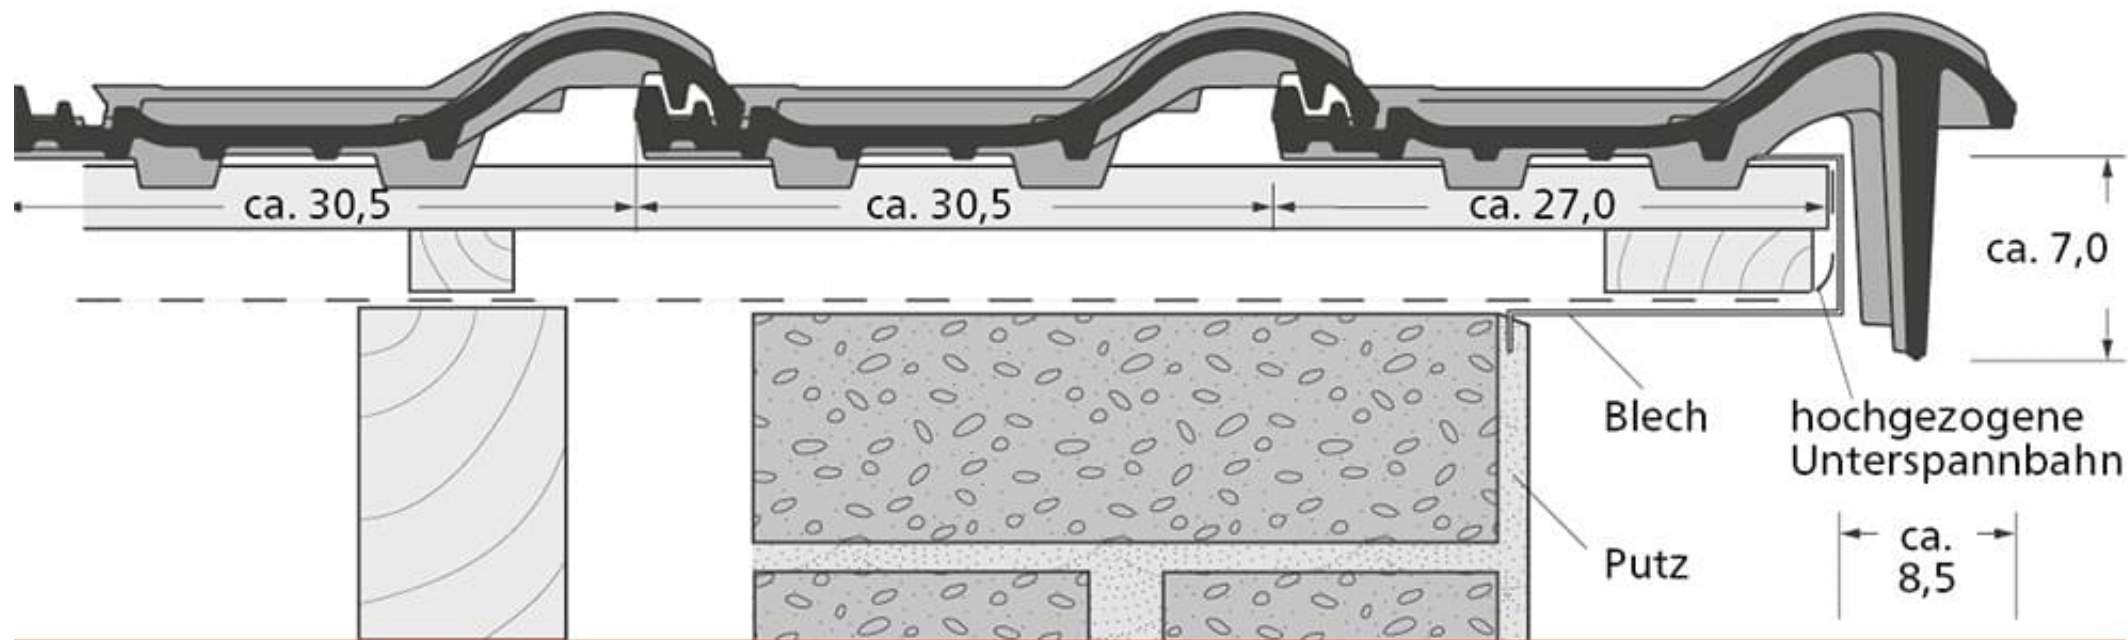

TRAUFE MIT ENTWÄSSERTEM UNTERDACH

ERLUS empfiehlt den Einsatz eines Traufbleches.

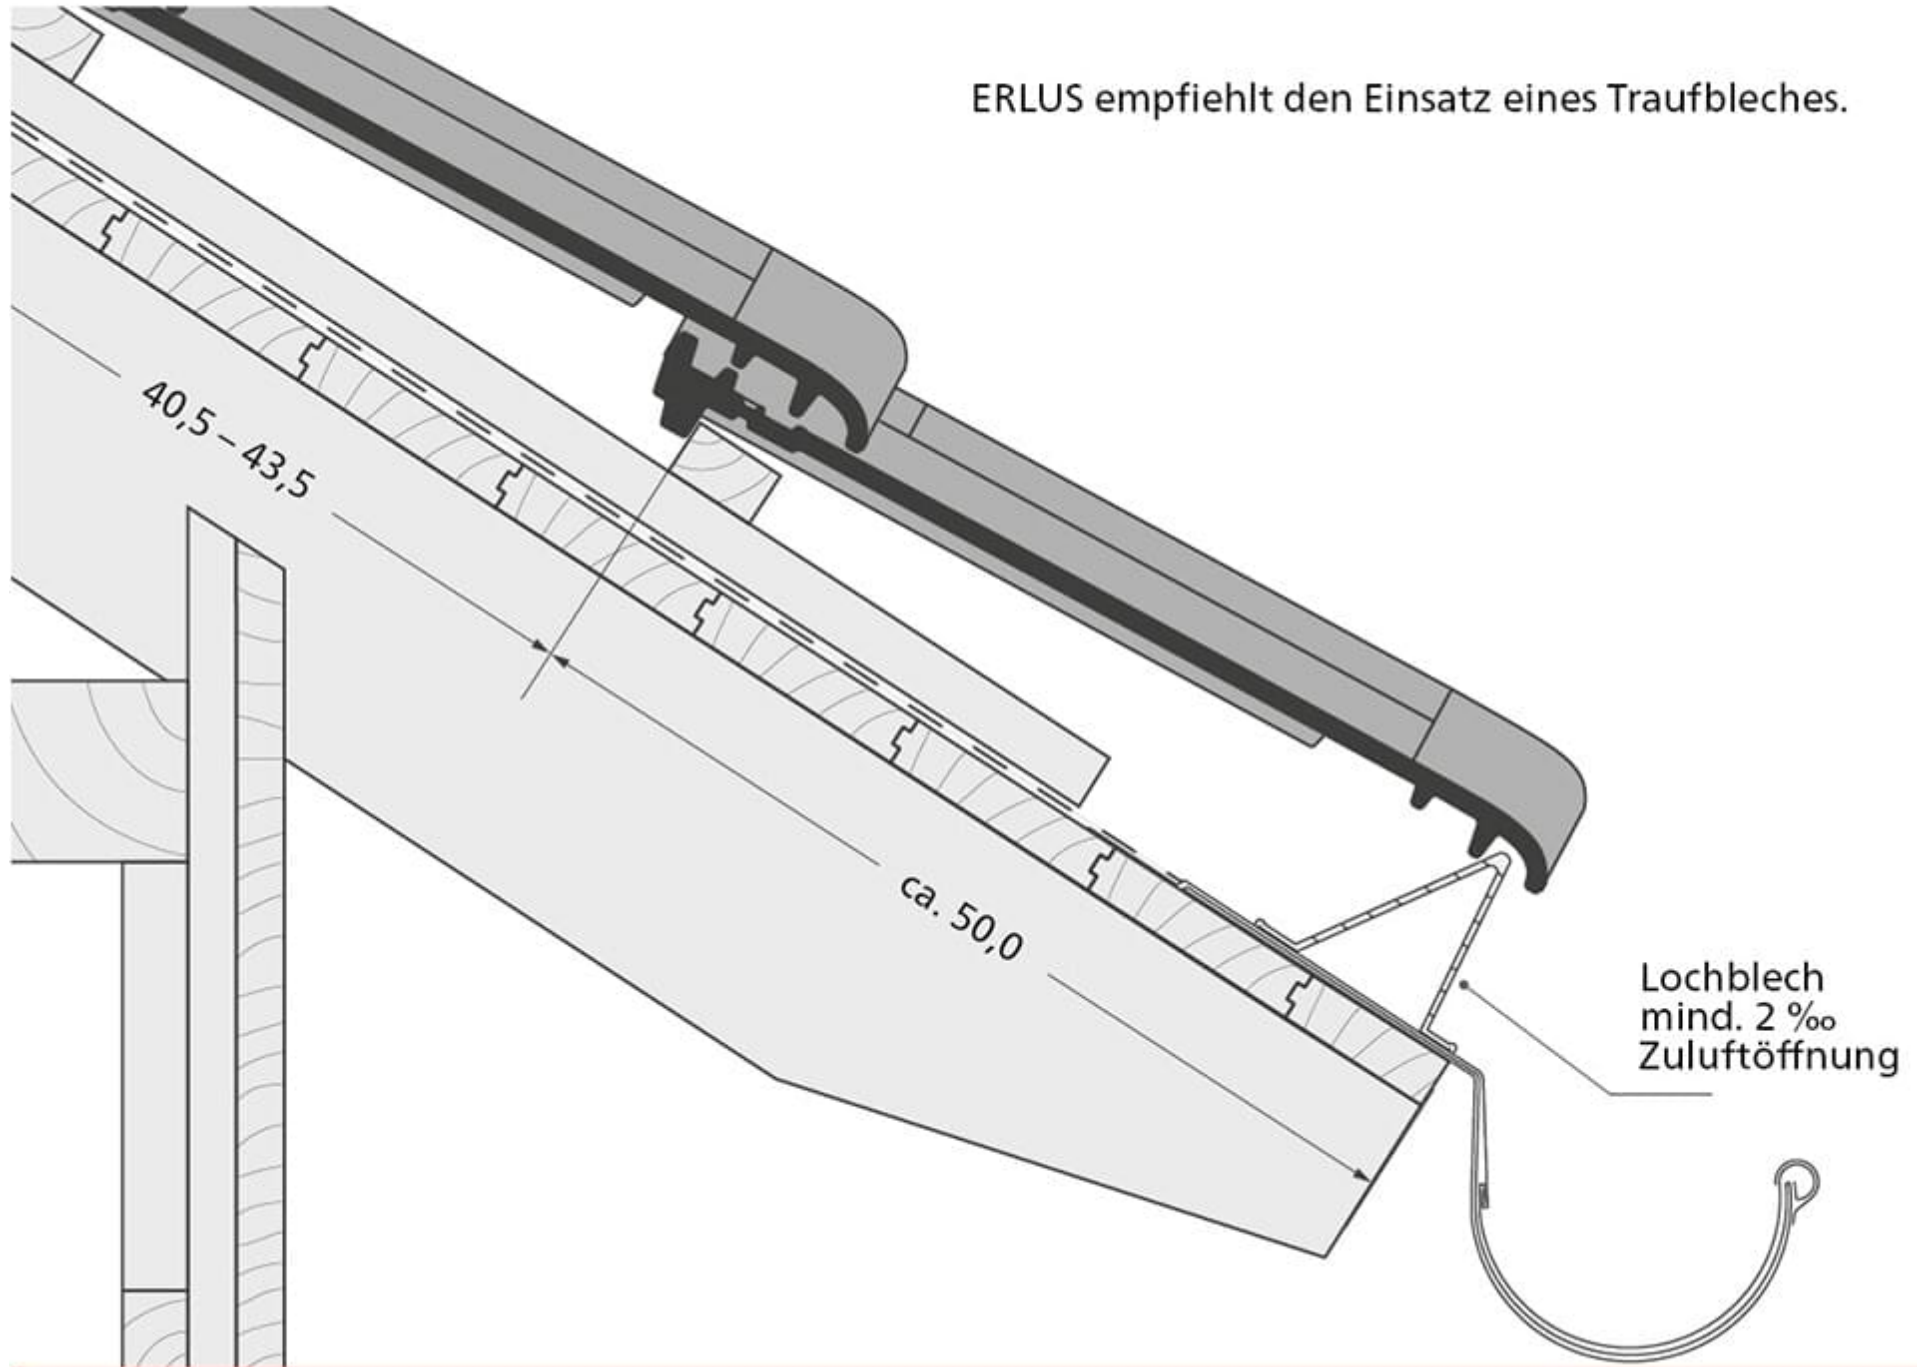

TRAUFE MIT AUFSPARRENDÄMMUNG

ERLUS empfiehlt den Einsatz eines Traufbleches.

