


ERLUS Dachbegehungssystem

LATTWEITE < 37,5 cm

alle Maßangaben in cm

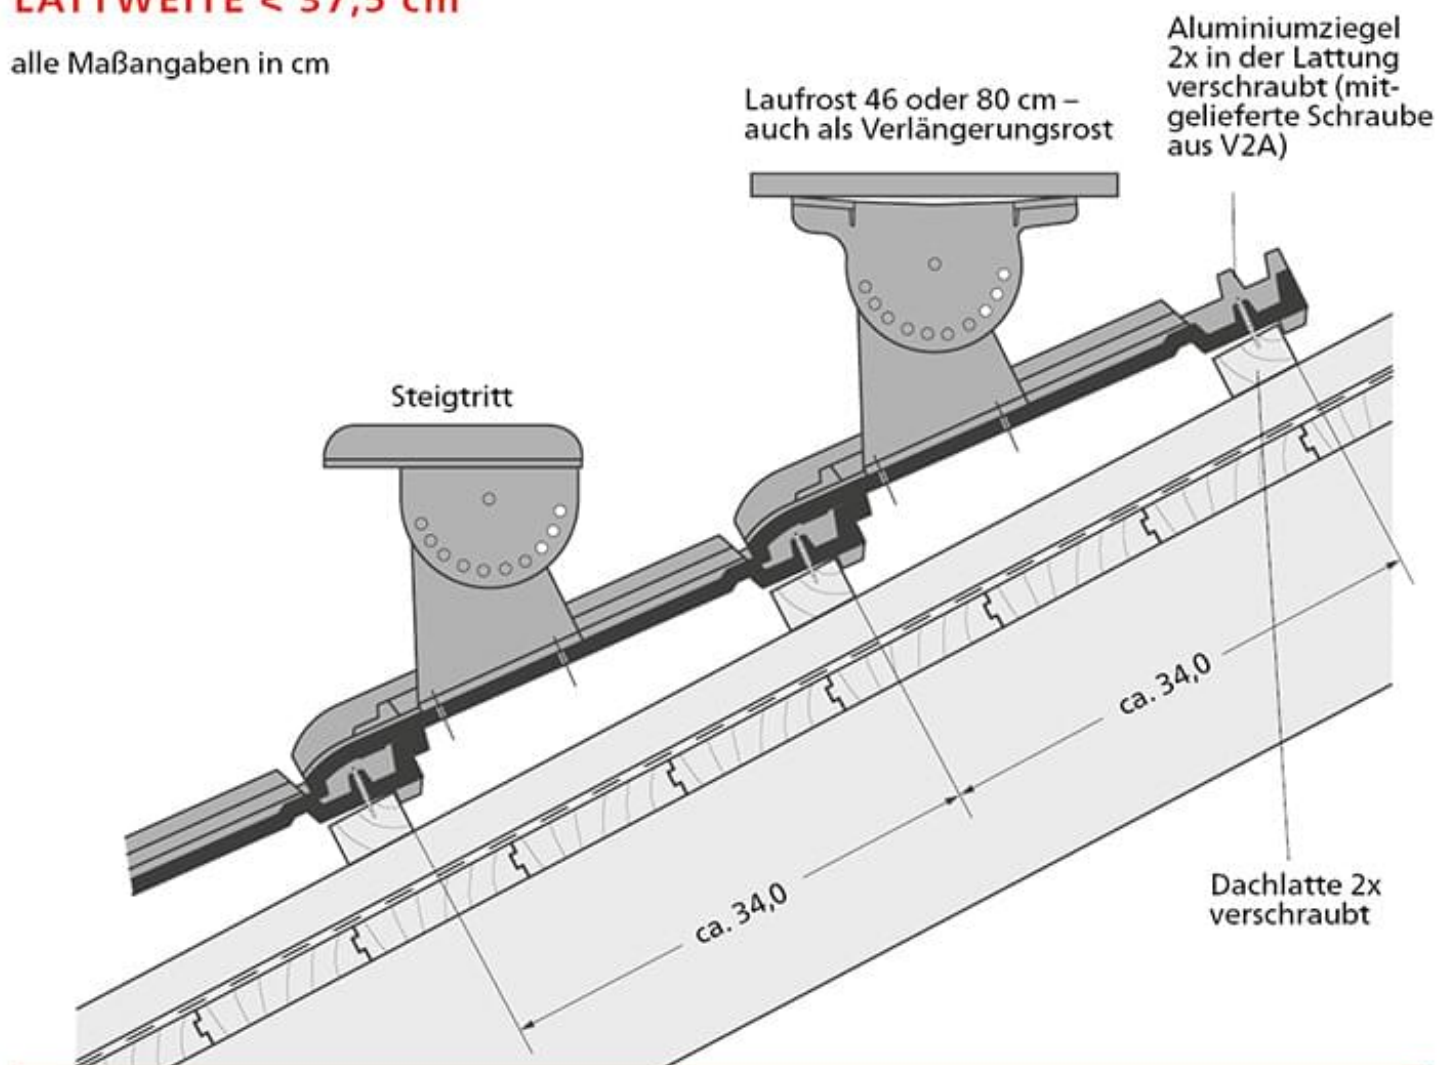

Zeichnung: E58


VERARBEITUNG VON TRITTFLÄCHEN UND ROSTEN NACH DIN 18160-5

ARTIKEL	$\leq 45^\circ$	$\geq 45^\circ$
Trittflächen (Roste 46 cm)	jede 2. Ziegelreihe	jede Ziegelreihe
Einzeltritt (Steigtritt)	jede Ziegelreihe	jede Ziegelreihe

aus nicht rostendem Stahl/Alu, geprüft nach DIN EN 516,

keine Stützlatte erforderlich

FIRSTLÜFTERZIEGEL NR. 19 LÜ MIT FIRSTANSCHLUSSZIEGEL

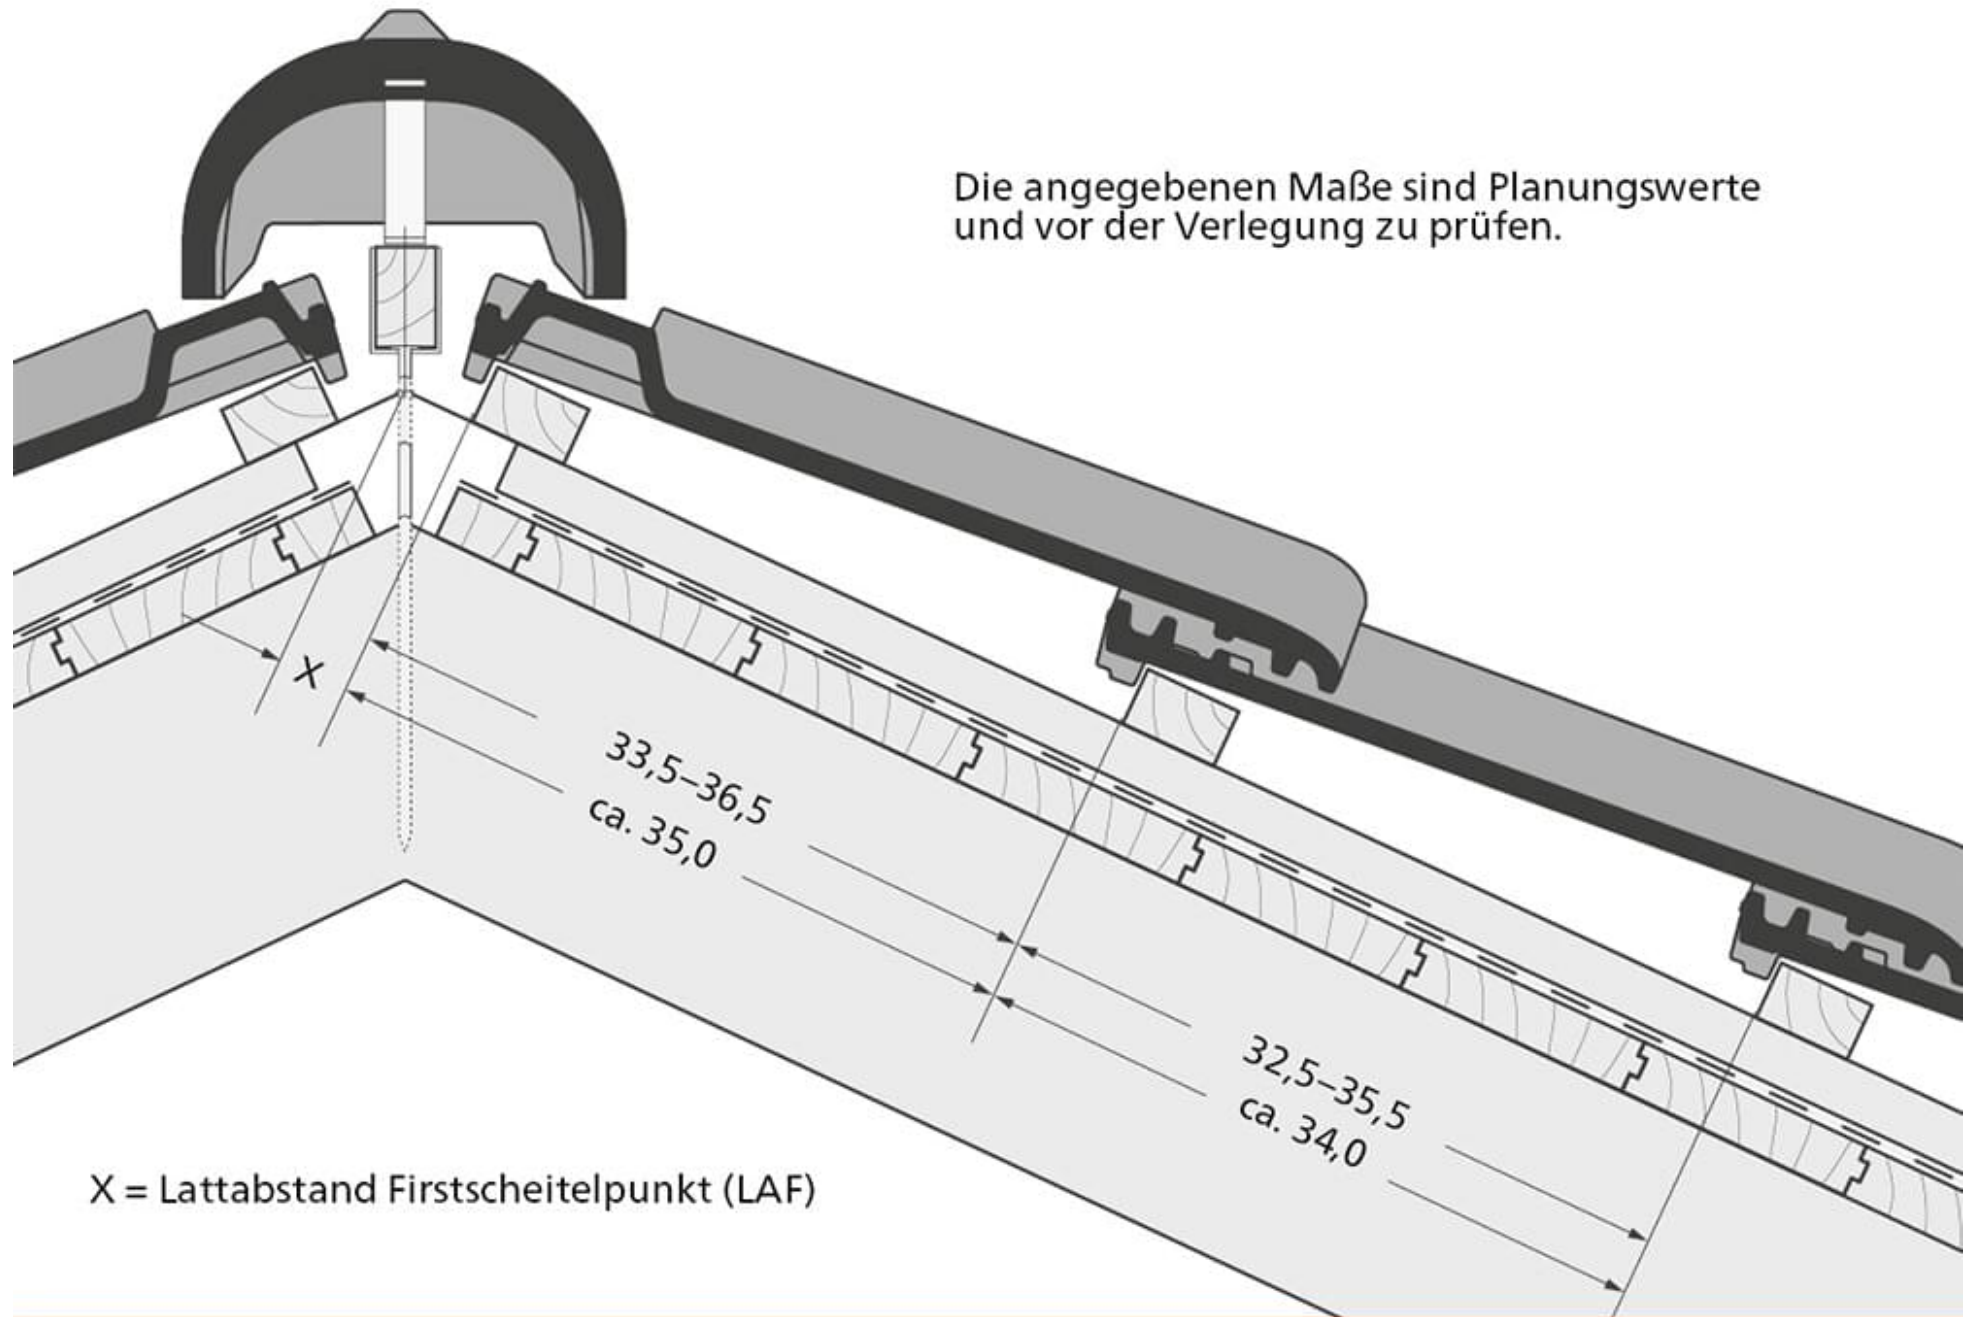


FIRSTLÜFTERZIEGEL NR. 19 LÜ

Firstziegel: 2,8 Stck./lfm.


Firstanfangsziegel

Hauptwetterrichtung

Firstendziegel

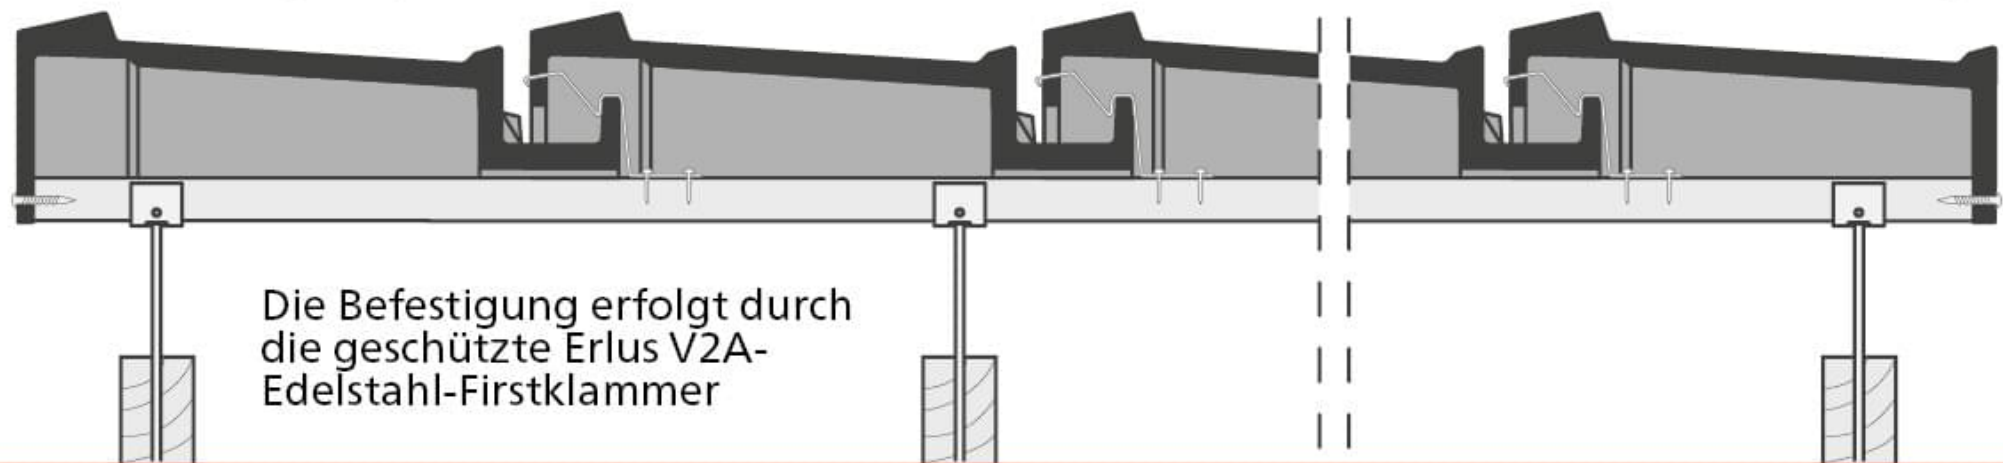


FIRSTZIEGEL NR. 15

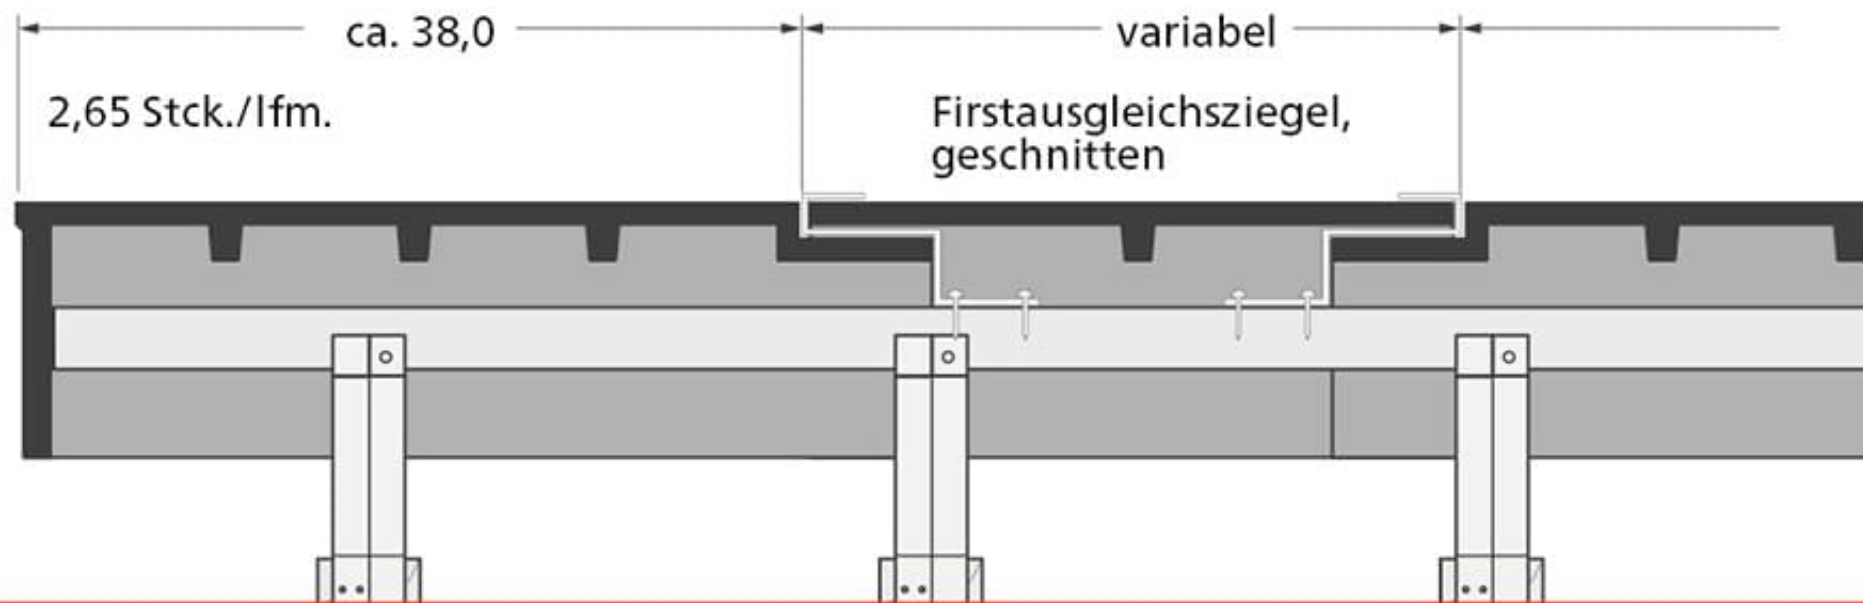


LINKER ORTGANG*

*bei flacher Dachneigung Verschraubungsloch im Ortgang dauerelastisch
(z. B. mit Spenglerschrauben) abdichten

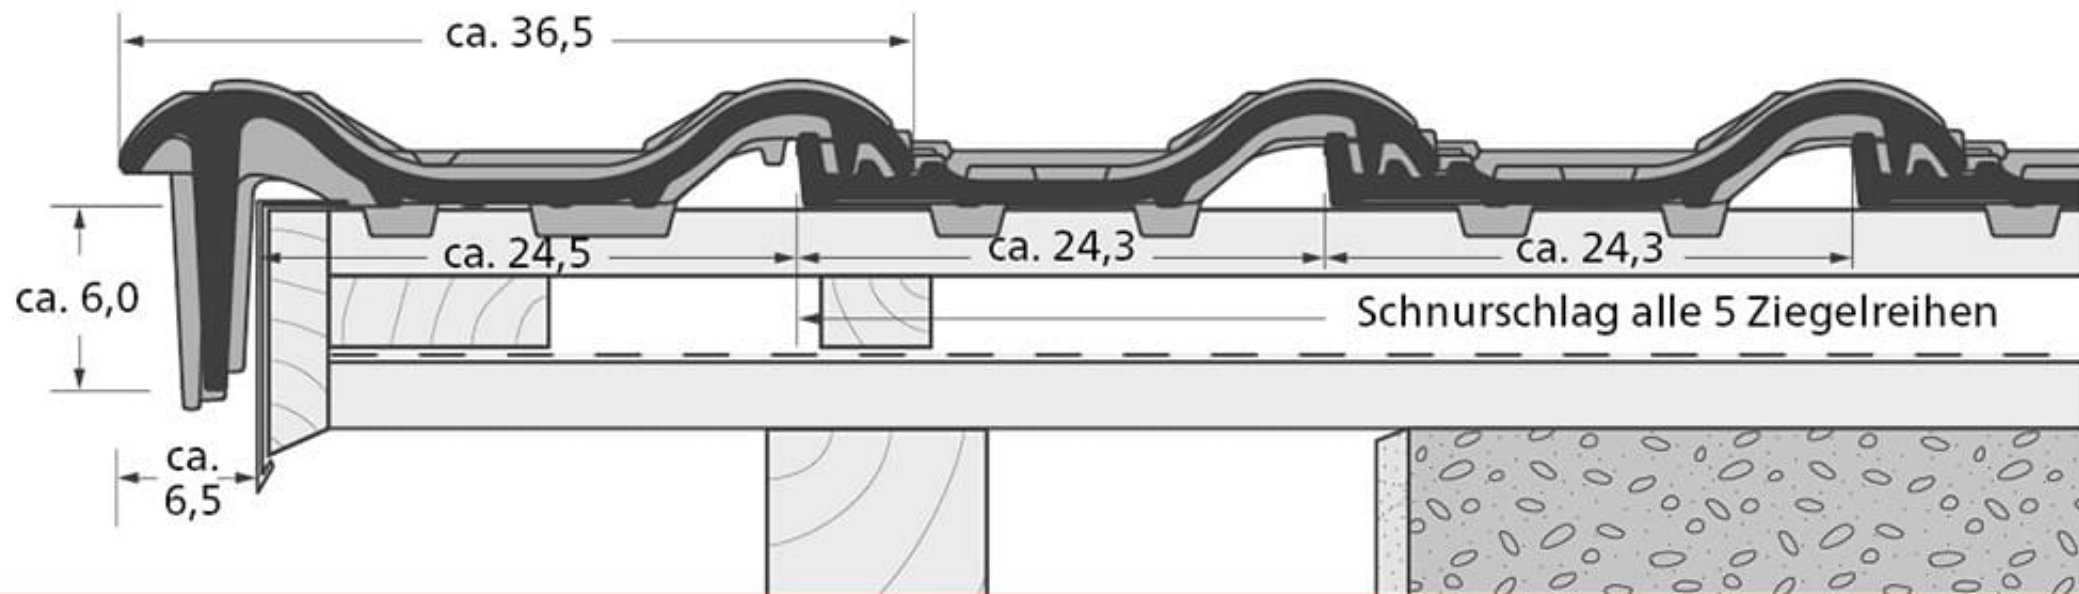


RECHTER ORTGANG*

*bei flacher Dachneigung Verschraubungsloch im Ortgang dauerelastisch
(z. B. mit Spenglerschrauben) abdichten

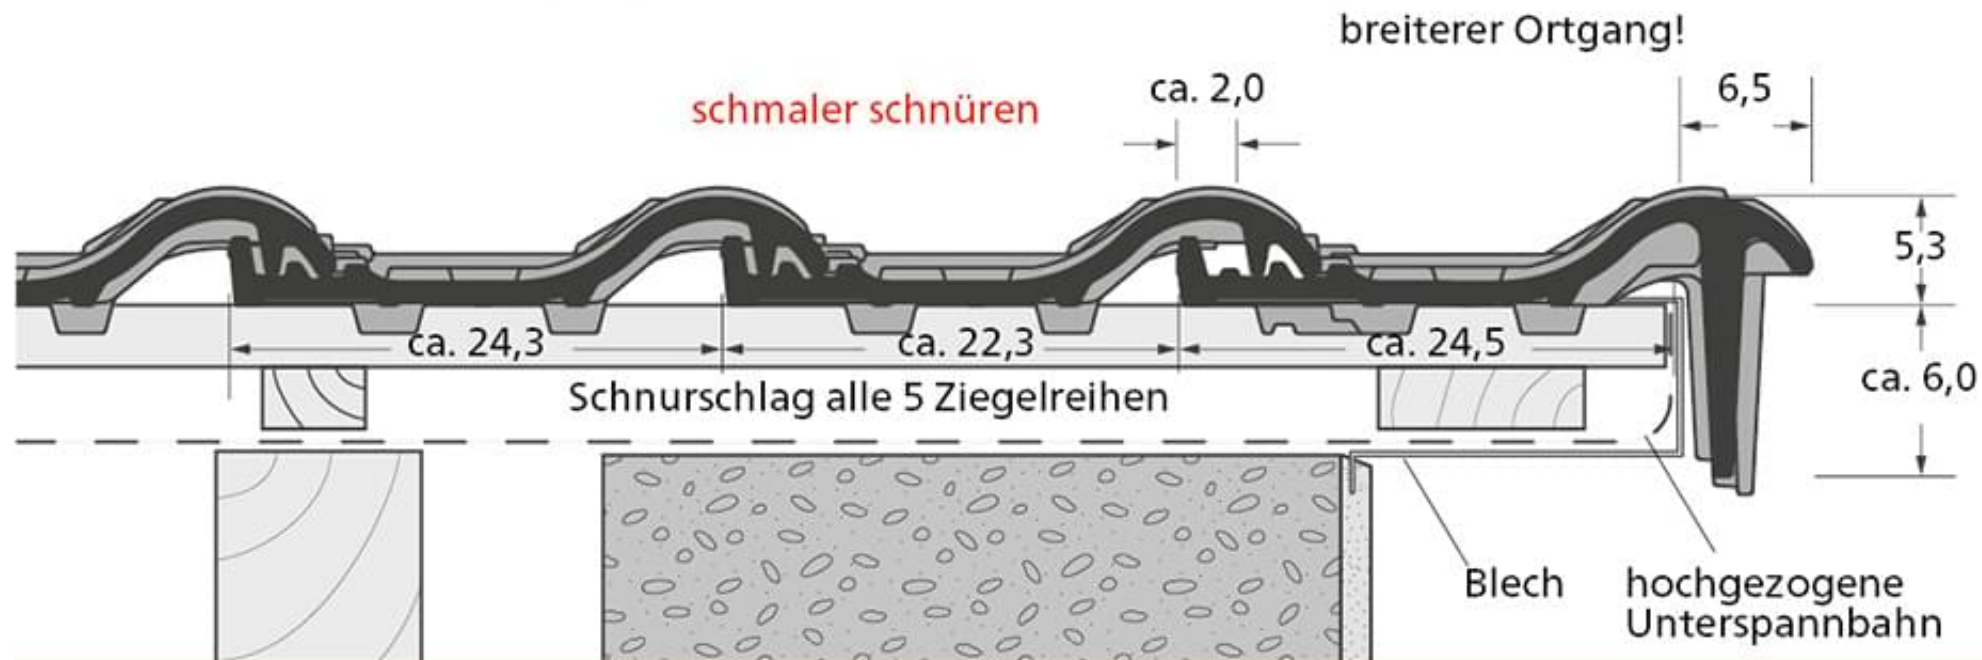

PULTDACH

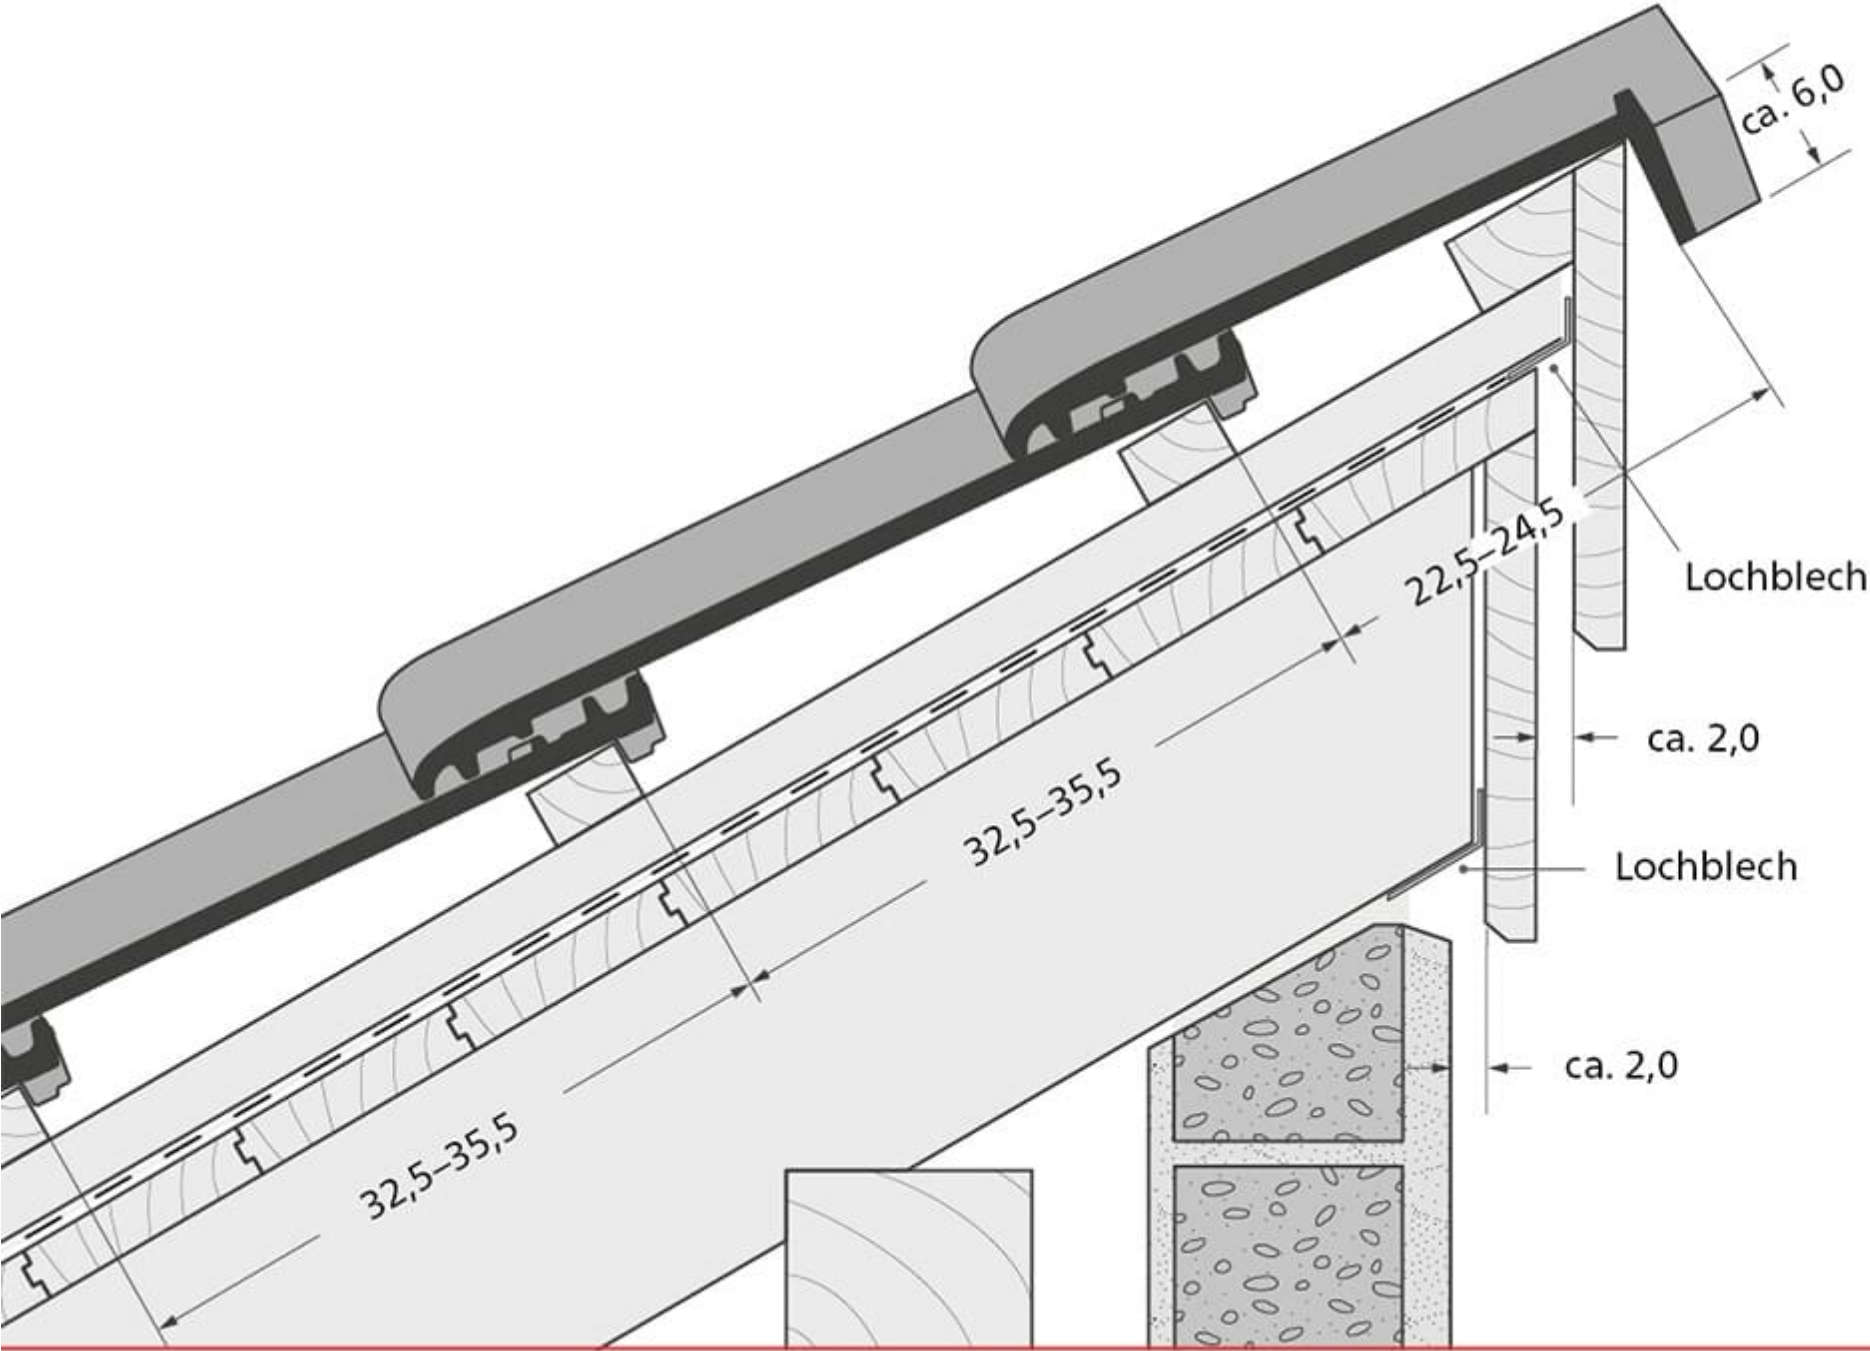

TRAUFE MIT AUFSPARRENDÄMMUNG

ERLUS empfiehlt den Einsatz eines Traufbleches.

