


ERLUS Dachbegehungssystem

LATTWEITE < 37,5 cm

alle Maßangaben in cm

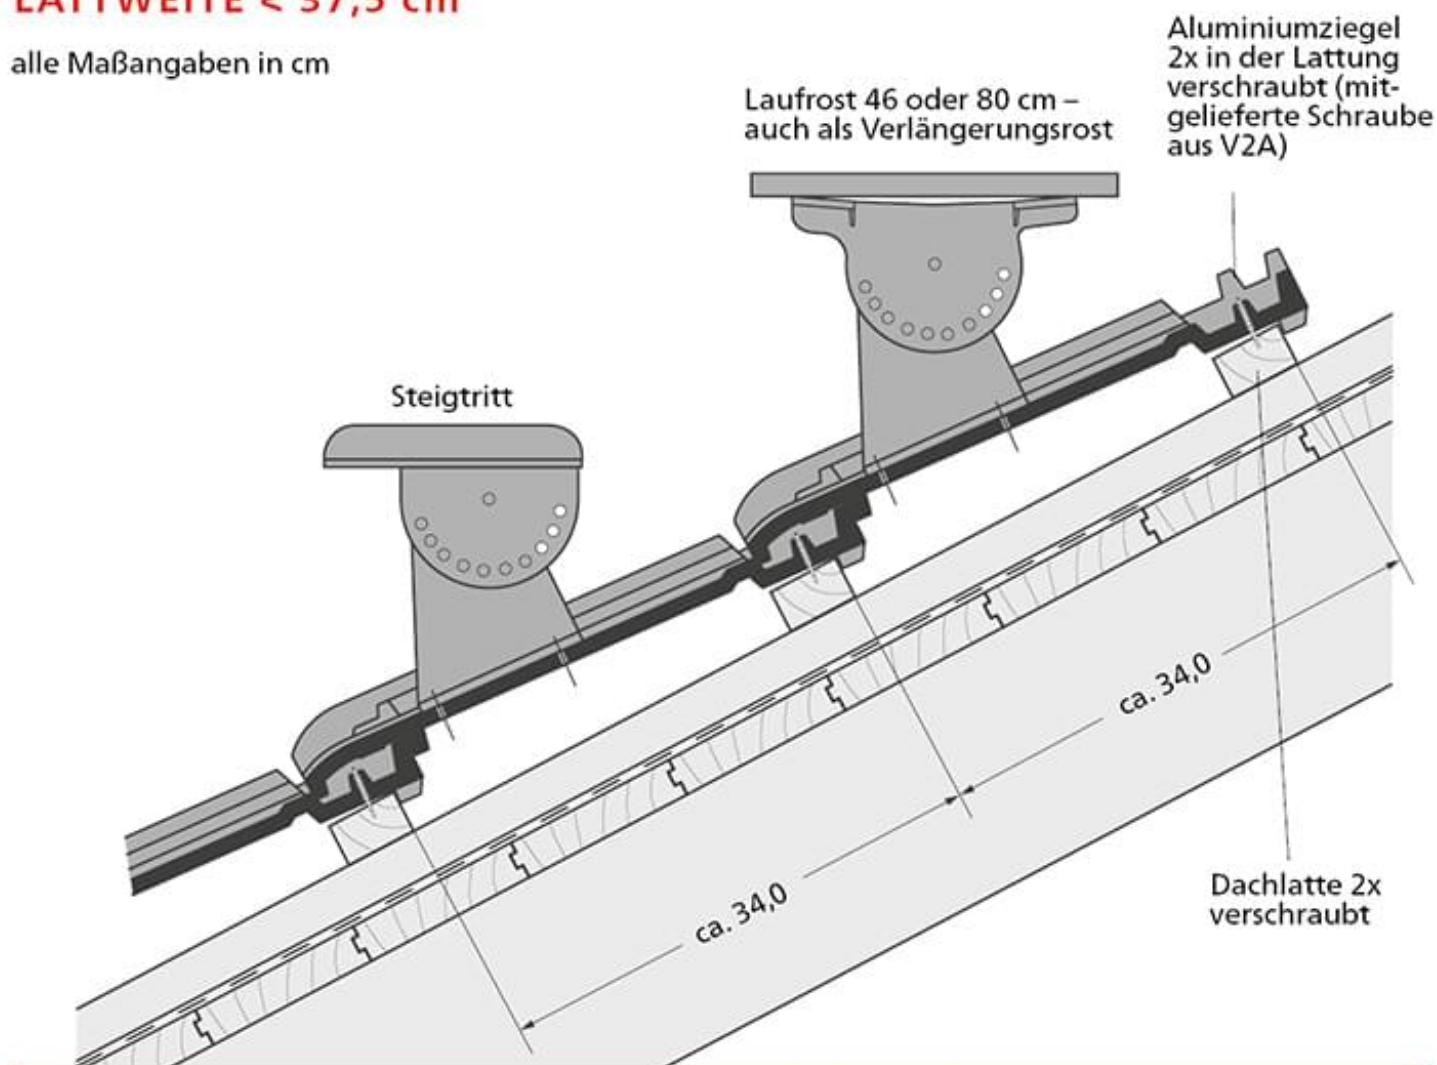

Zeichnung: E58


VERARBEITUNG VON TRITTFLÄCHEN UND ROSTEN NACH DIN 18160-5

ARTIKEL	$\leq 45^\circ$	$\geq 45^\circ$
Trittflächen (Roste 46 cm)	jede 2. Ziegelreihe	jede Ziegelreihe
Einzeltritt (Steigtritt)	jede Ziegelreihe	jede Ziegelreihe

aus nicht rostendem Stahl/Alu, geprüft nach DIN EN 516,

keine Stützlaten erforderlich

FIRSTZIEGEL NR. 18 MIT FLÄCHENZIEGEL

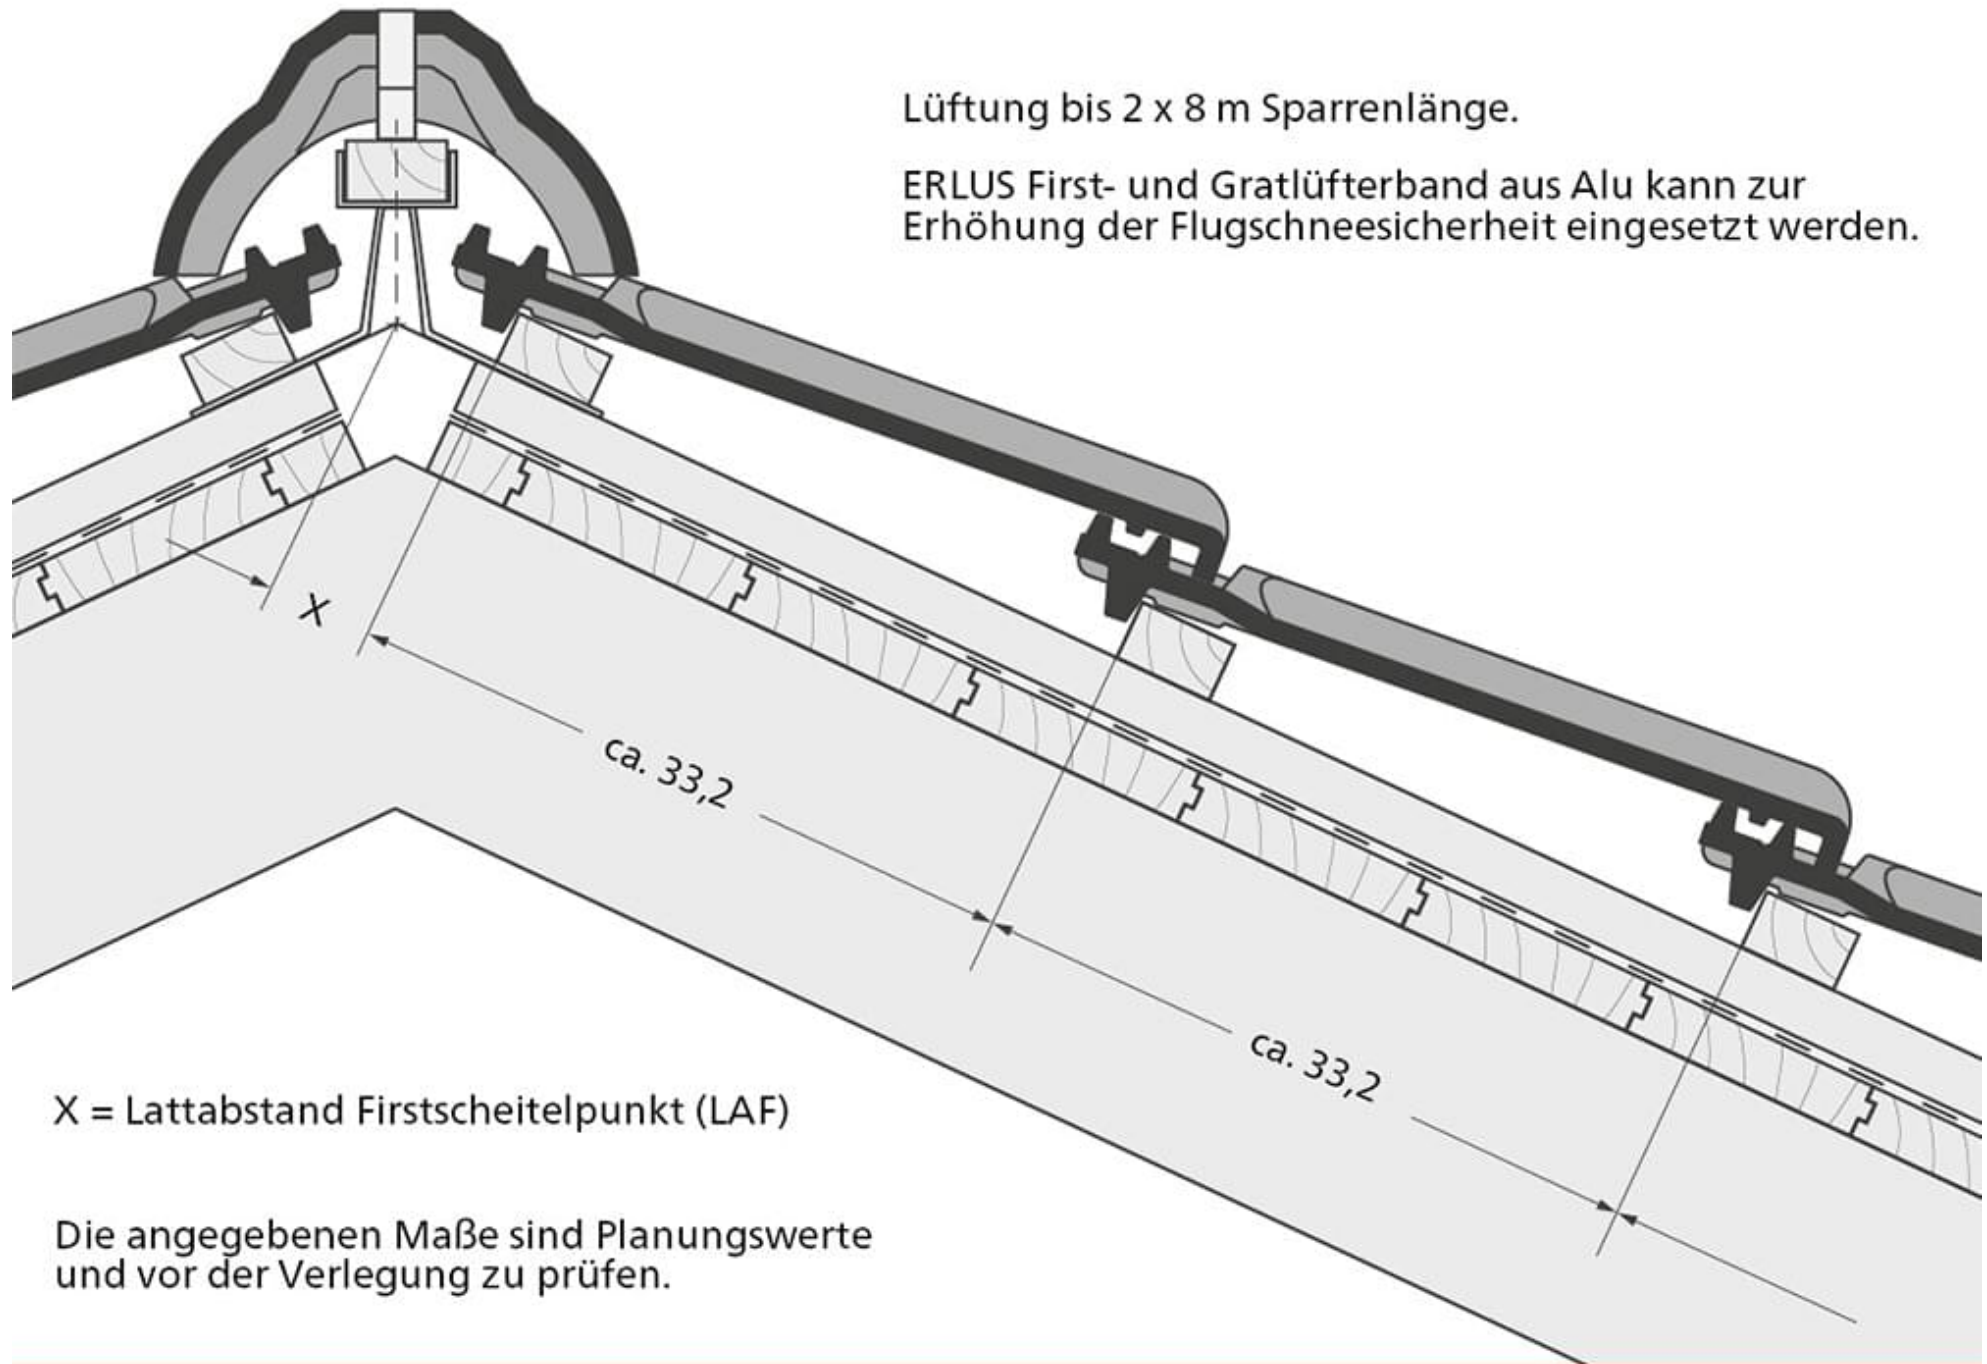


FIRSTZIEGEL NR. 18

Firstabschlussziegel
Nr. 18 geschnitten

Firstausgleichsziegel Nr. 18

Firstziegel Nr. 18
2,6 Stck./lfm.

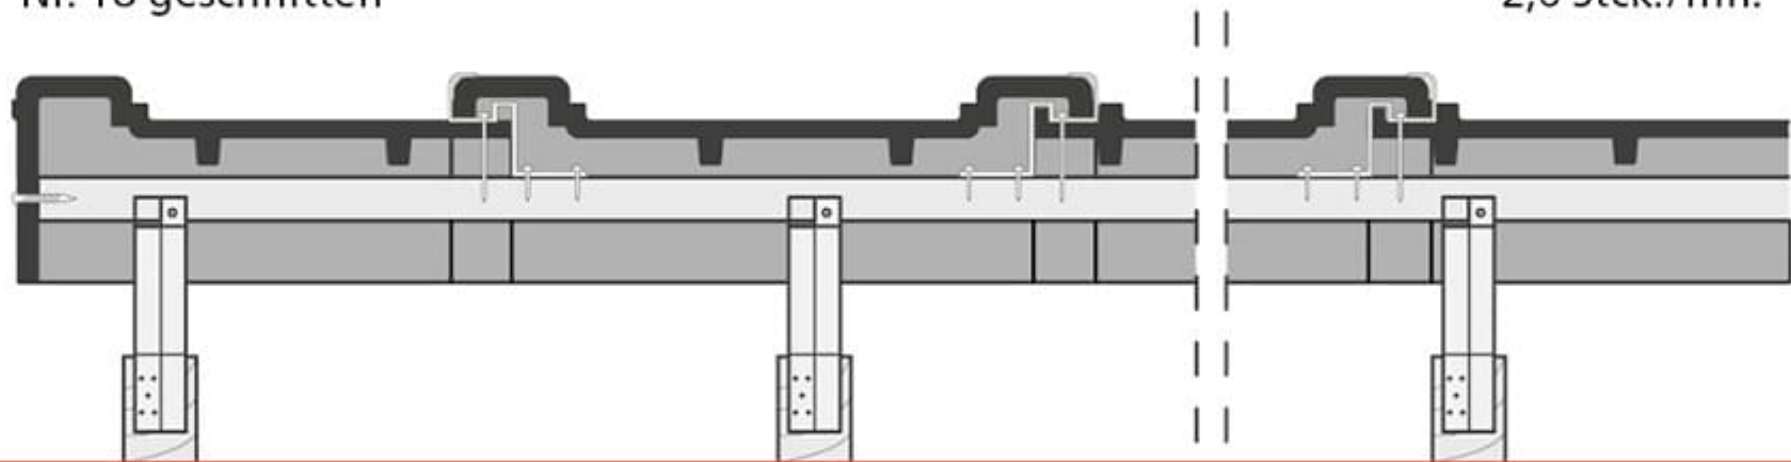


FIRSTLÜFTERZIEGEL NR. 19 LÜ

Firstziegel: 2,8 Stck./lfm.

Firstanfangsziegel

Hauptwetterrichtung


Firstendziegel

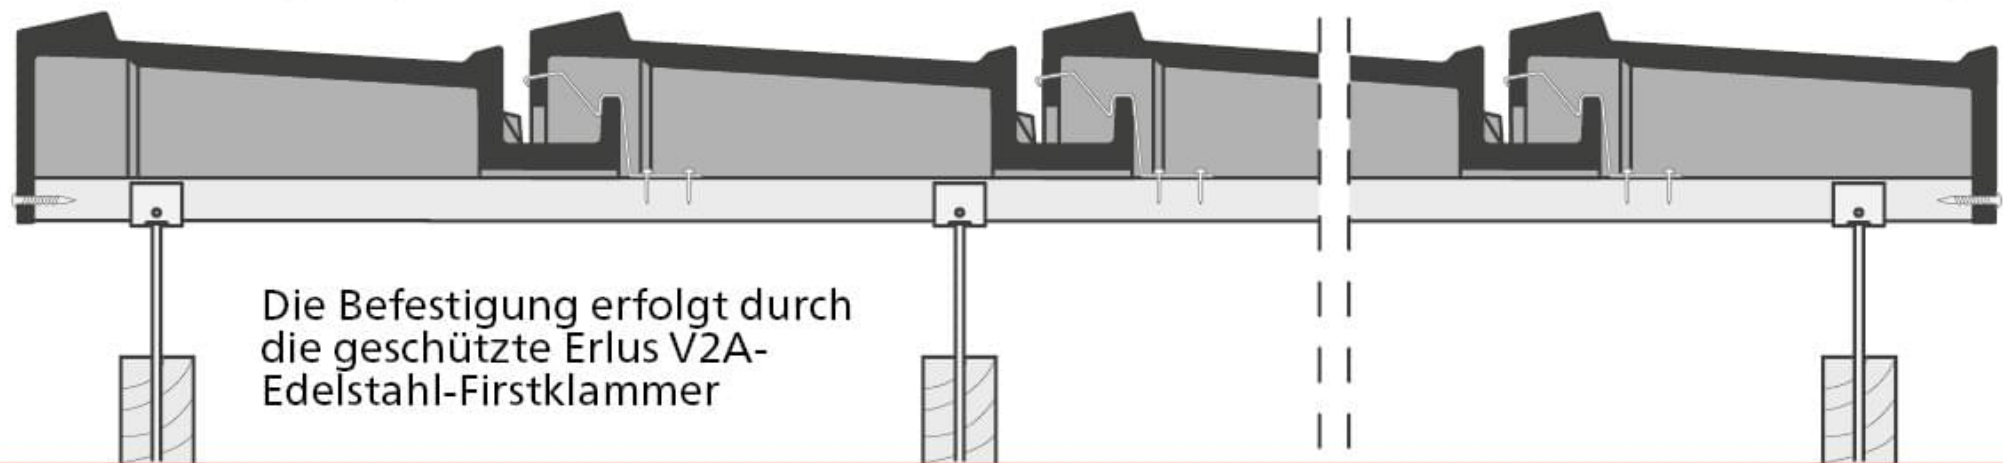

Die Befestigung erfolgt durch die geschützte Erlus V2A-Edelstahl-Firstklammer


LINKER ORTGANG*

*bei flacher Dachneigung Verschraubungsloch im Ortgang dauerelastisch
(z. B. mit Spenglerschrauben) abdichten

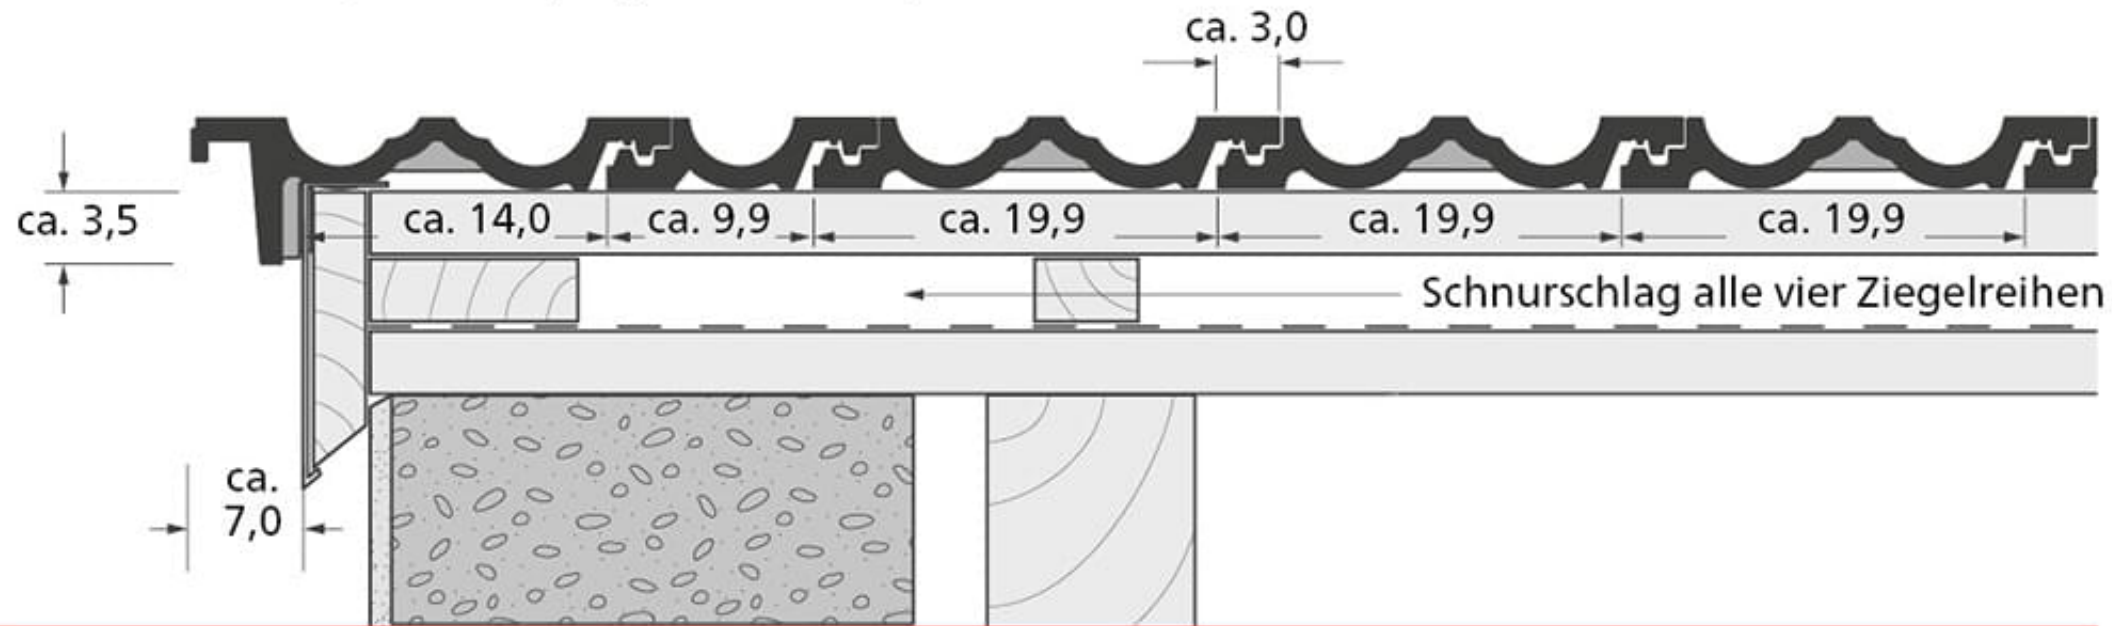


RECHTER ORTGANG*

*bei flacher Dachneigung Verschraubungsloch im Ortgang dauerelastisch
(z. B. mit Spenglerschrauben) abdichten

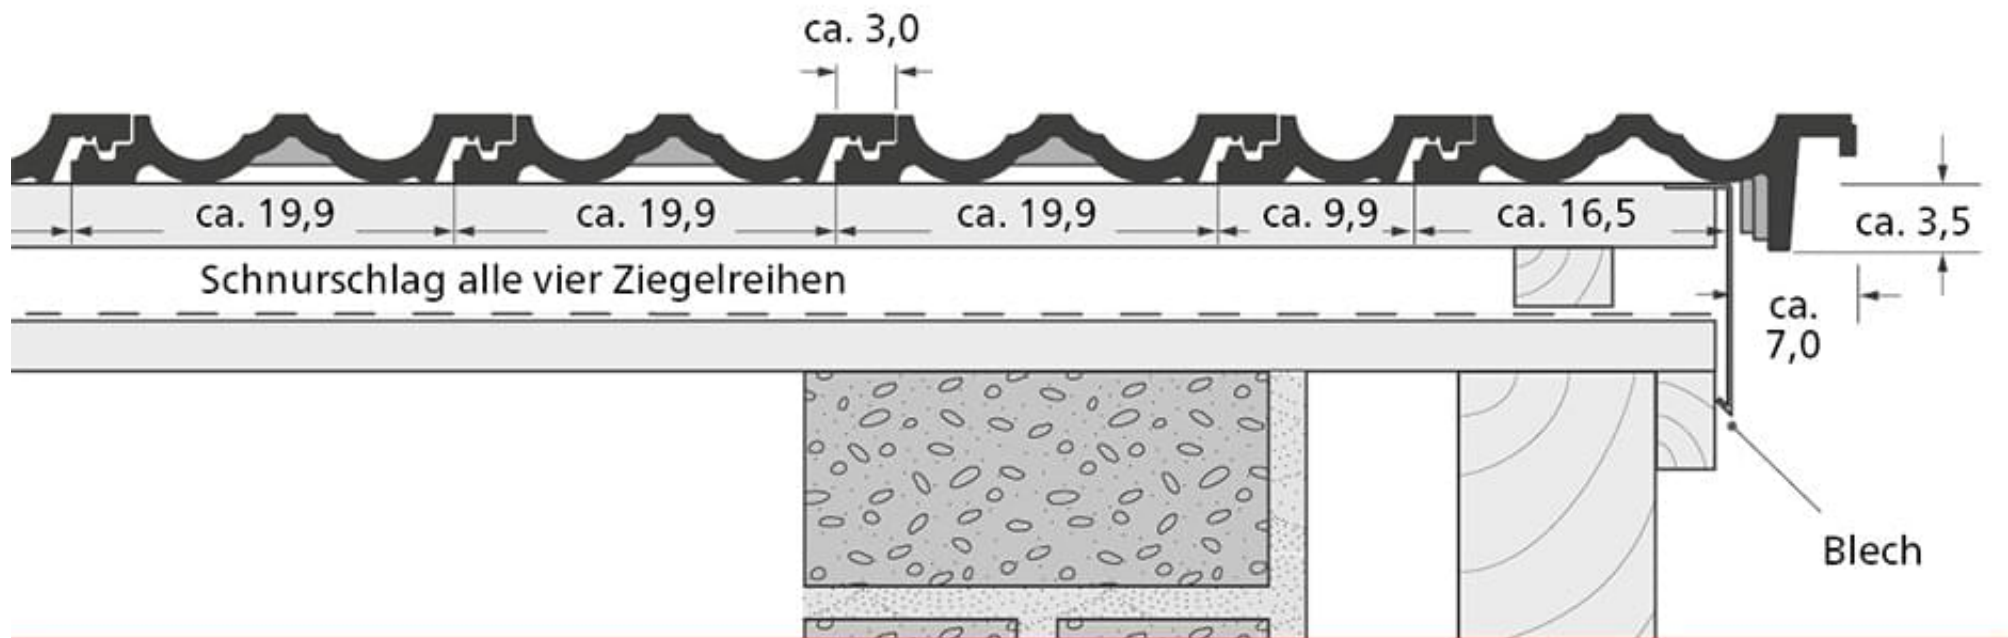

TRAUFE

ERLUS empfiehlt den Einsatz eines Traufbleches.

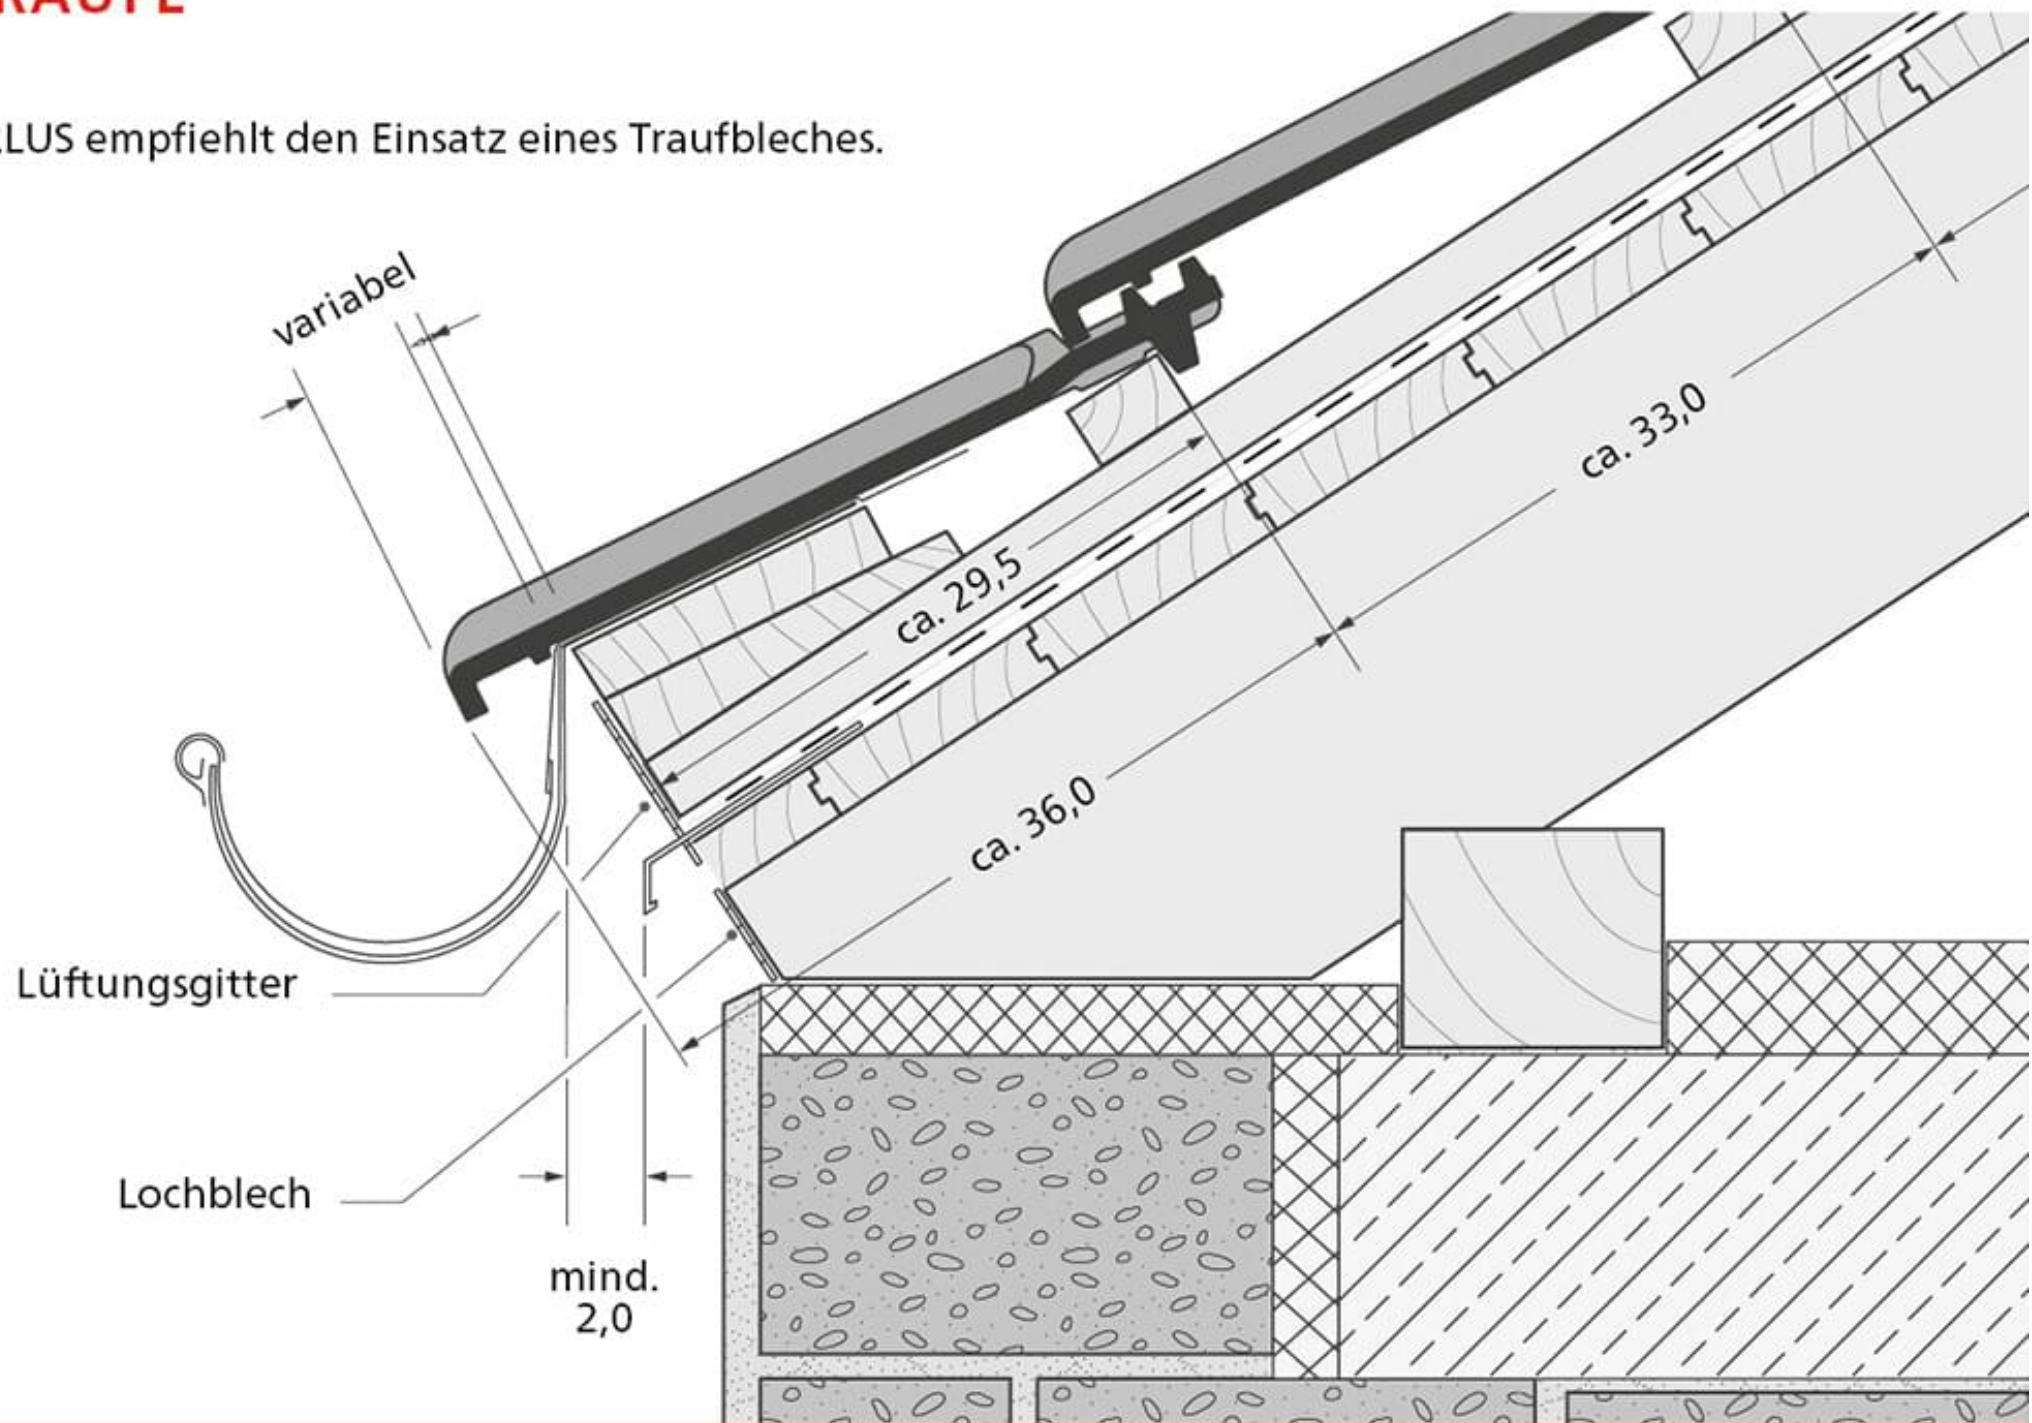

ERLUS empfiehlt den Einsatz eines Traufbleches.

ca. 33,2

ca. 36,0

Verklebung

Lochblech
mind. 2‰
Zuluftöffnung

ERLUS empfiehlt den Einsatz eines Traufbleches.

ca. 33,2

Verklebung

ca. 36,0

Lochblech
mind. 2‰
Zuluftöffnung