


FIRSTZIEGEL NR. 18 MIT FLÄCHENZIEGEL

Lüftung bis 2 x 16 m Sparrenlänge.

ERLUS First- und Gratlüfterband aus Alu kann zur Erhöhung der Flugschneesicherheit eingesetzt werden.

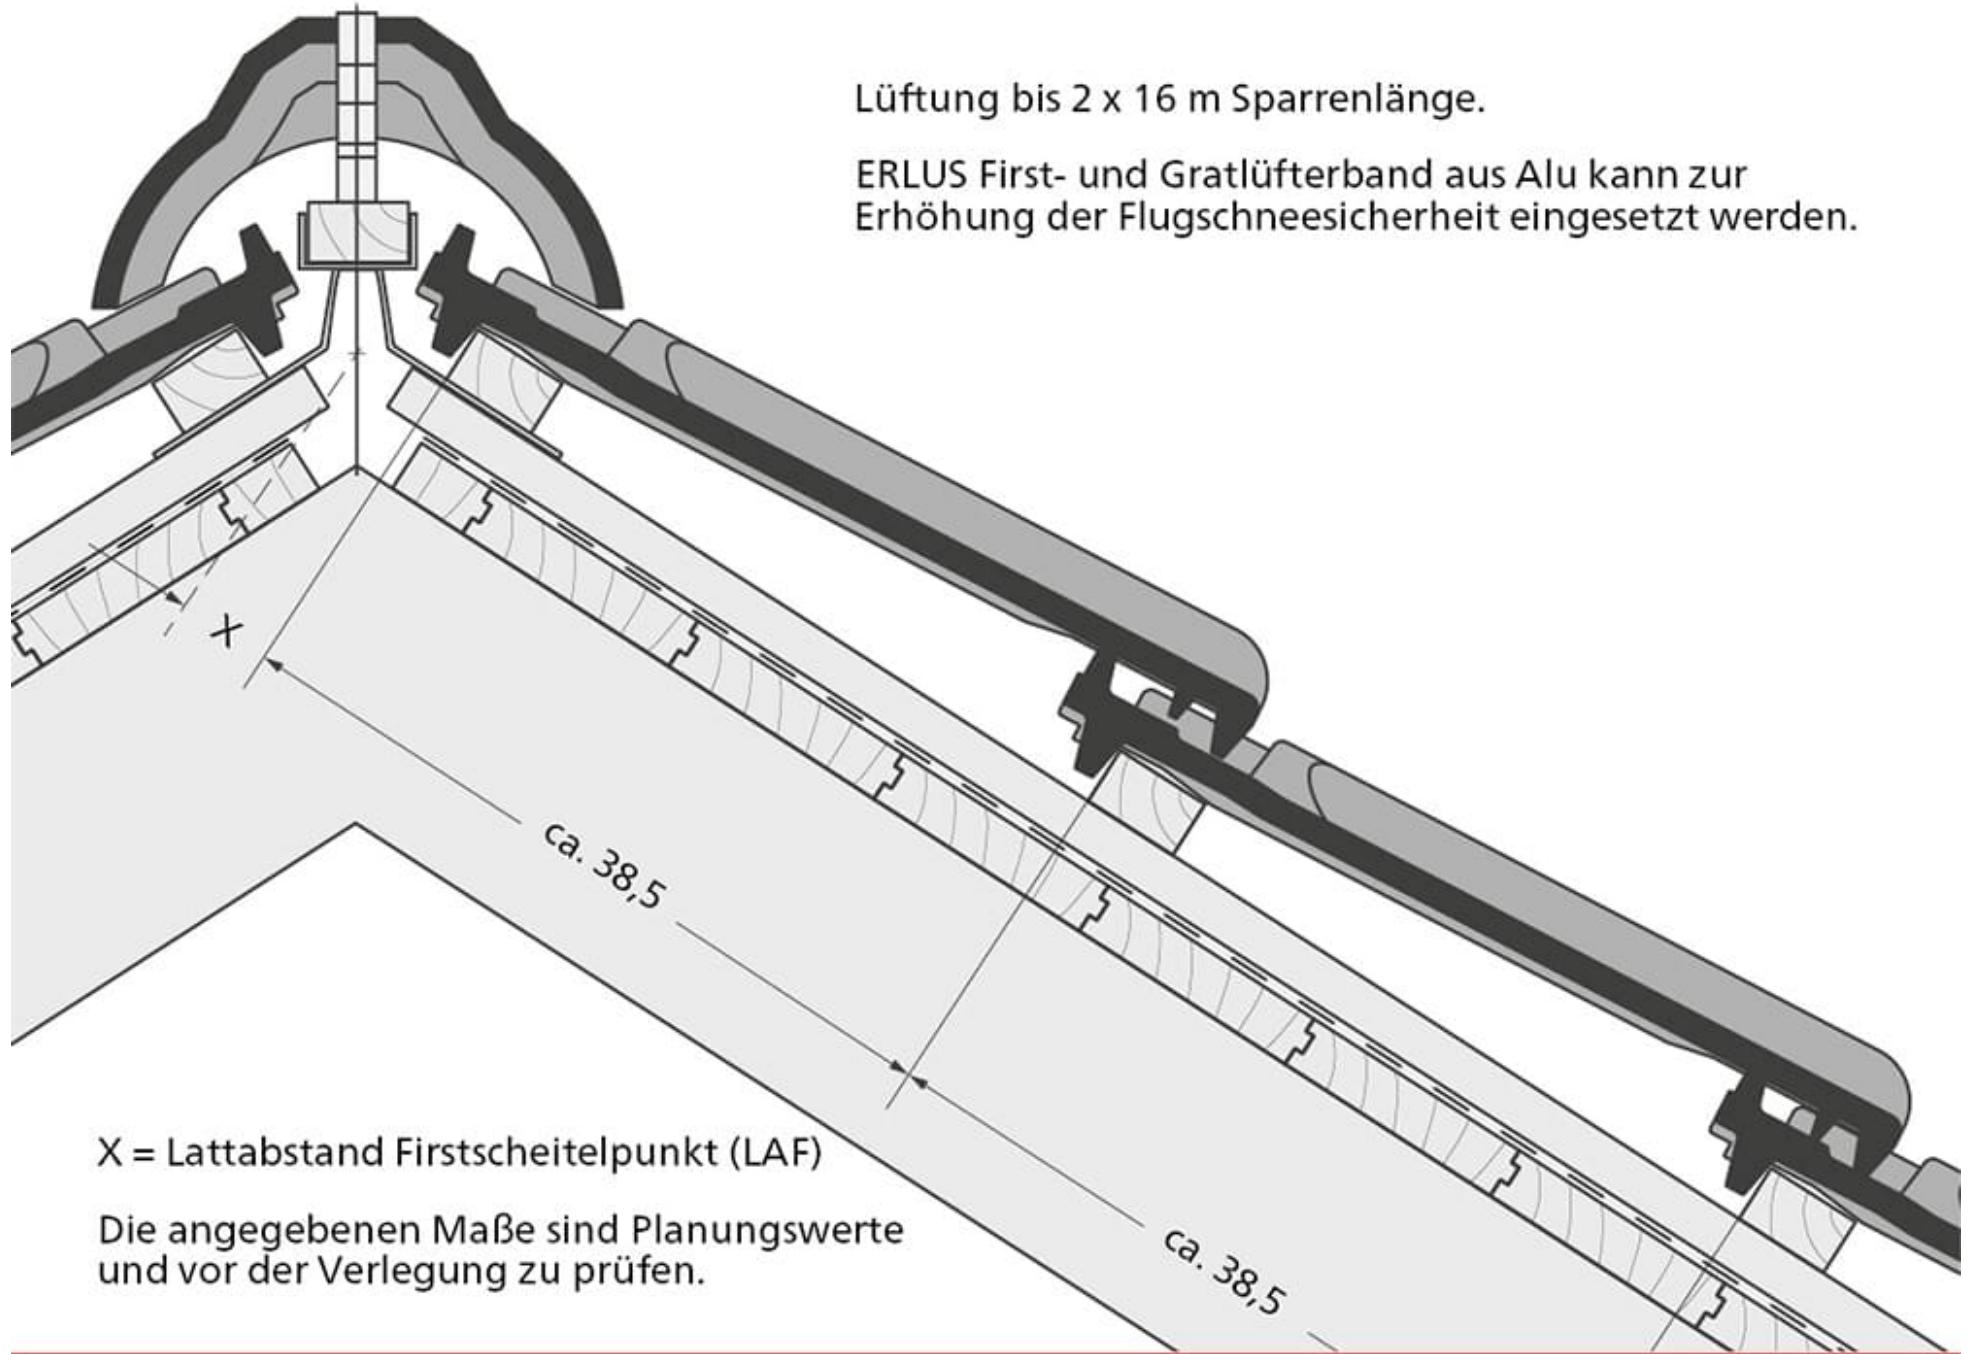

X = Lattabstand Firstscheitelpunkt (LAF)

Die angegebenen Maße sind Planungswerte und vor der Verlegung zu prüfen.


FIRSTLÜFTERZIEGEL NR. 19 LÜ

Firstziegel: 2,8 Stck./lfm.

Firstanfangsziegel

Hauptwetterrichtung

Firstendziegel

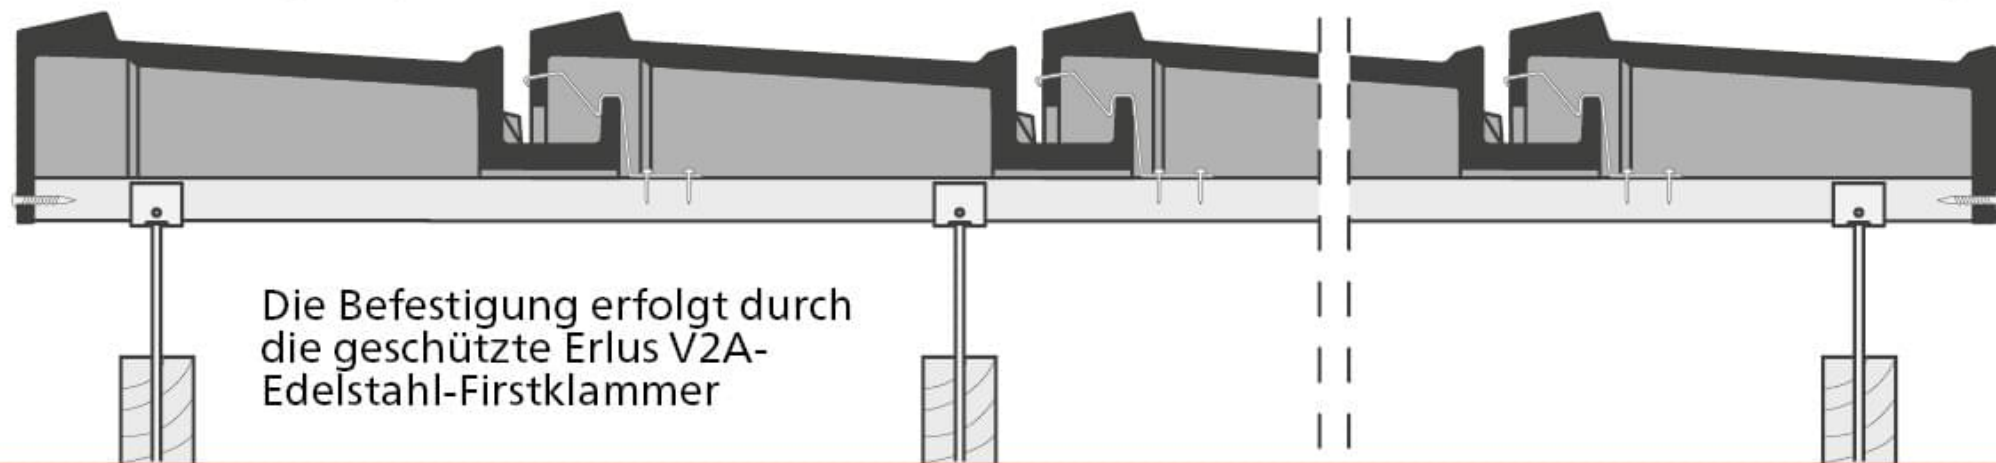


Die Befestigung erfolgt durch die geschützte Erlus V2A-Edelstahl-Firstklammer

FIRSTZIEGEL NR. 18

Firstabschlussziegel
Nr. 18 geschnitten


Firstausgleichsziegel Nr. 18

Firstziegel Nr. 18
2,6 Stck./lfm.

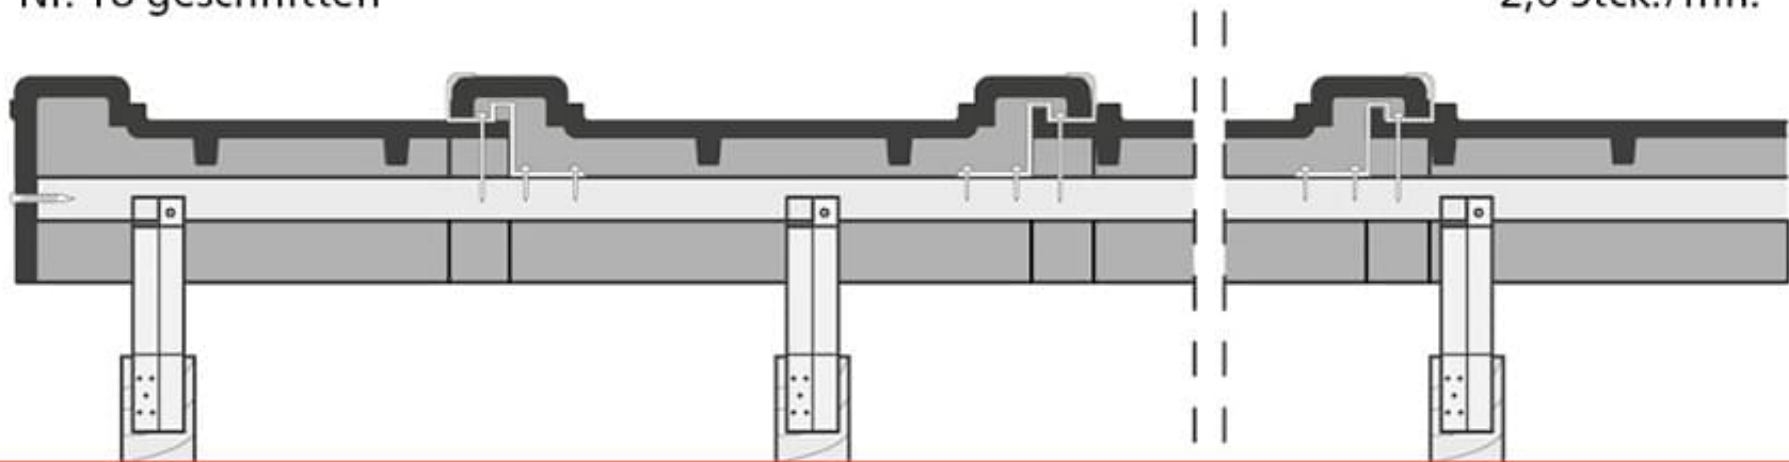


LINKER ORTGANG*

*bei flacher Dachneigung Verschraubungsloch im Ortgang dauerelastisch
(z. B. mit Spenglerschrauben) abdichten

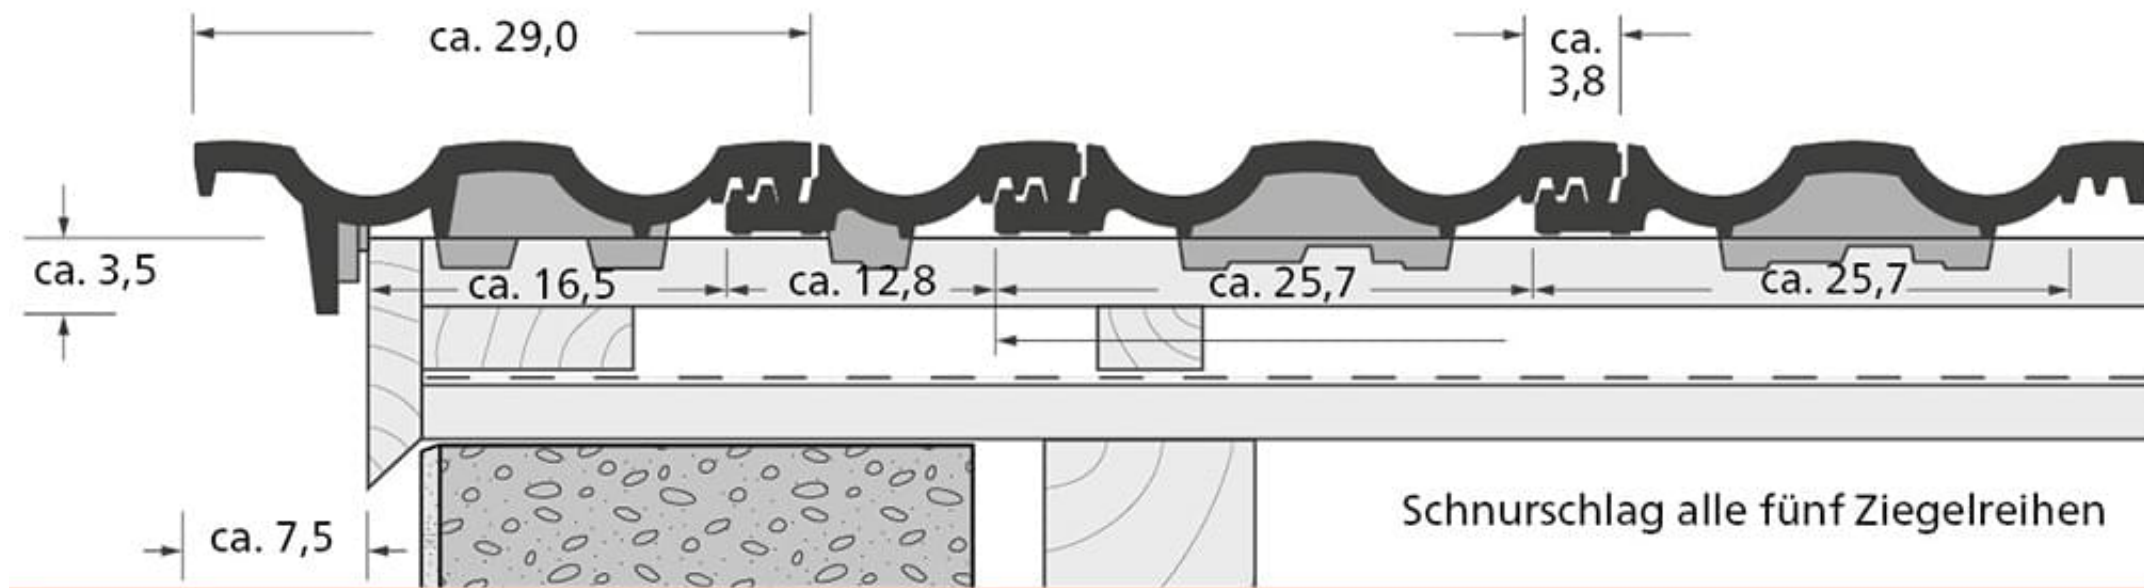


RECHTER ORTGANG*

*bei flacher Dachneigung Verschraubungsloch im Ortgang dauerelastisch
(z. B. mit Spenglerschrauben) abdichten

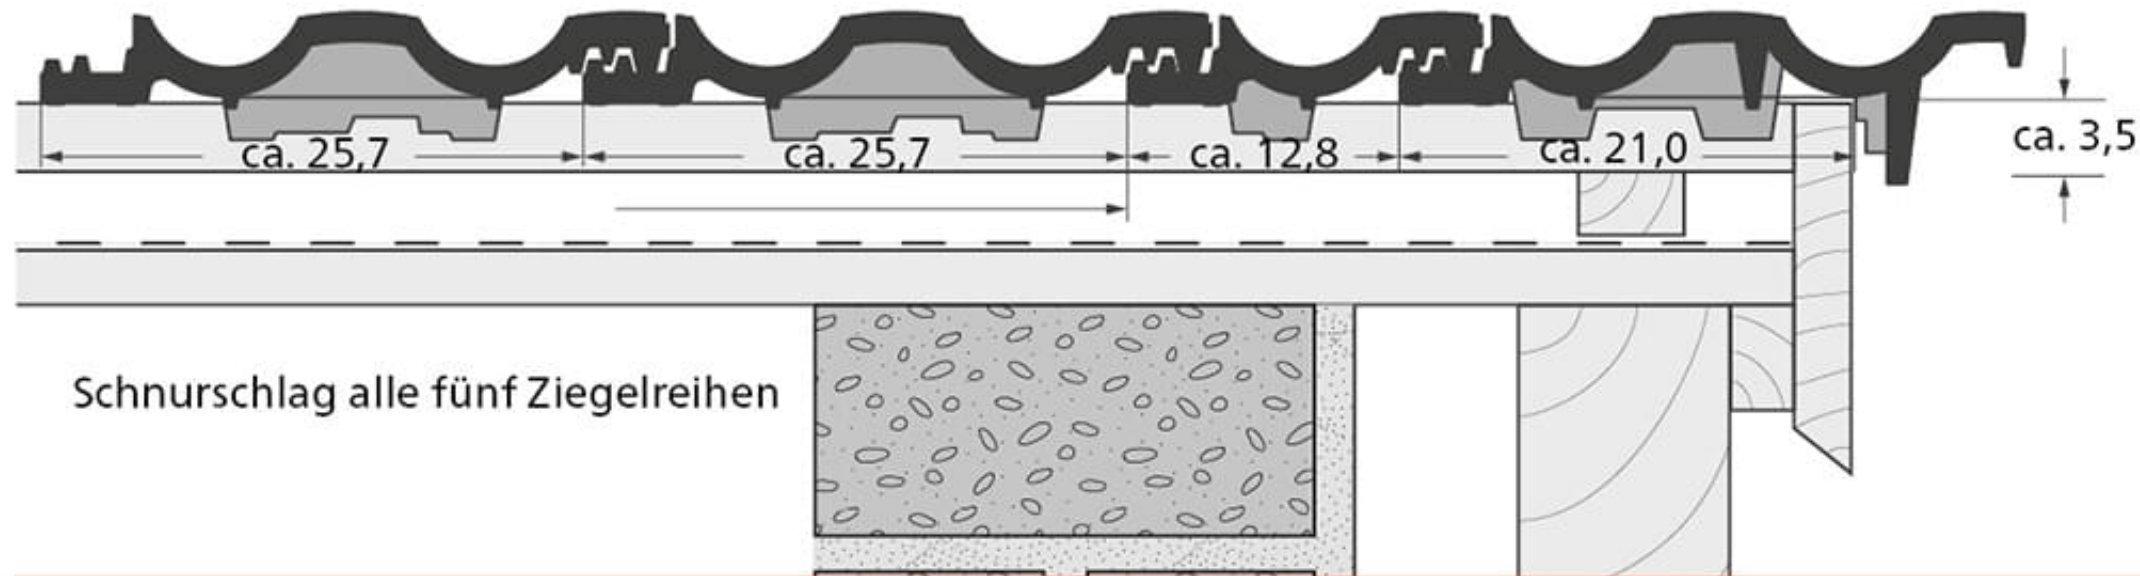

TRAUFE

ERLUS empfiehlt den Einsatz eines Traufbleches.

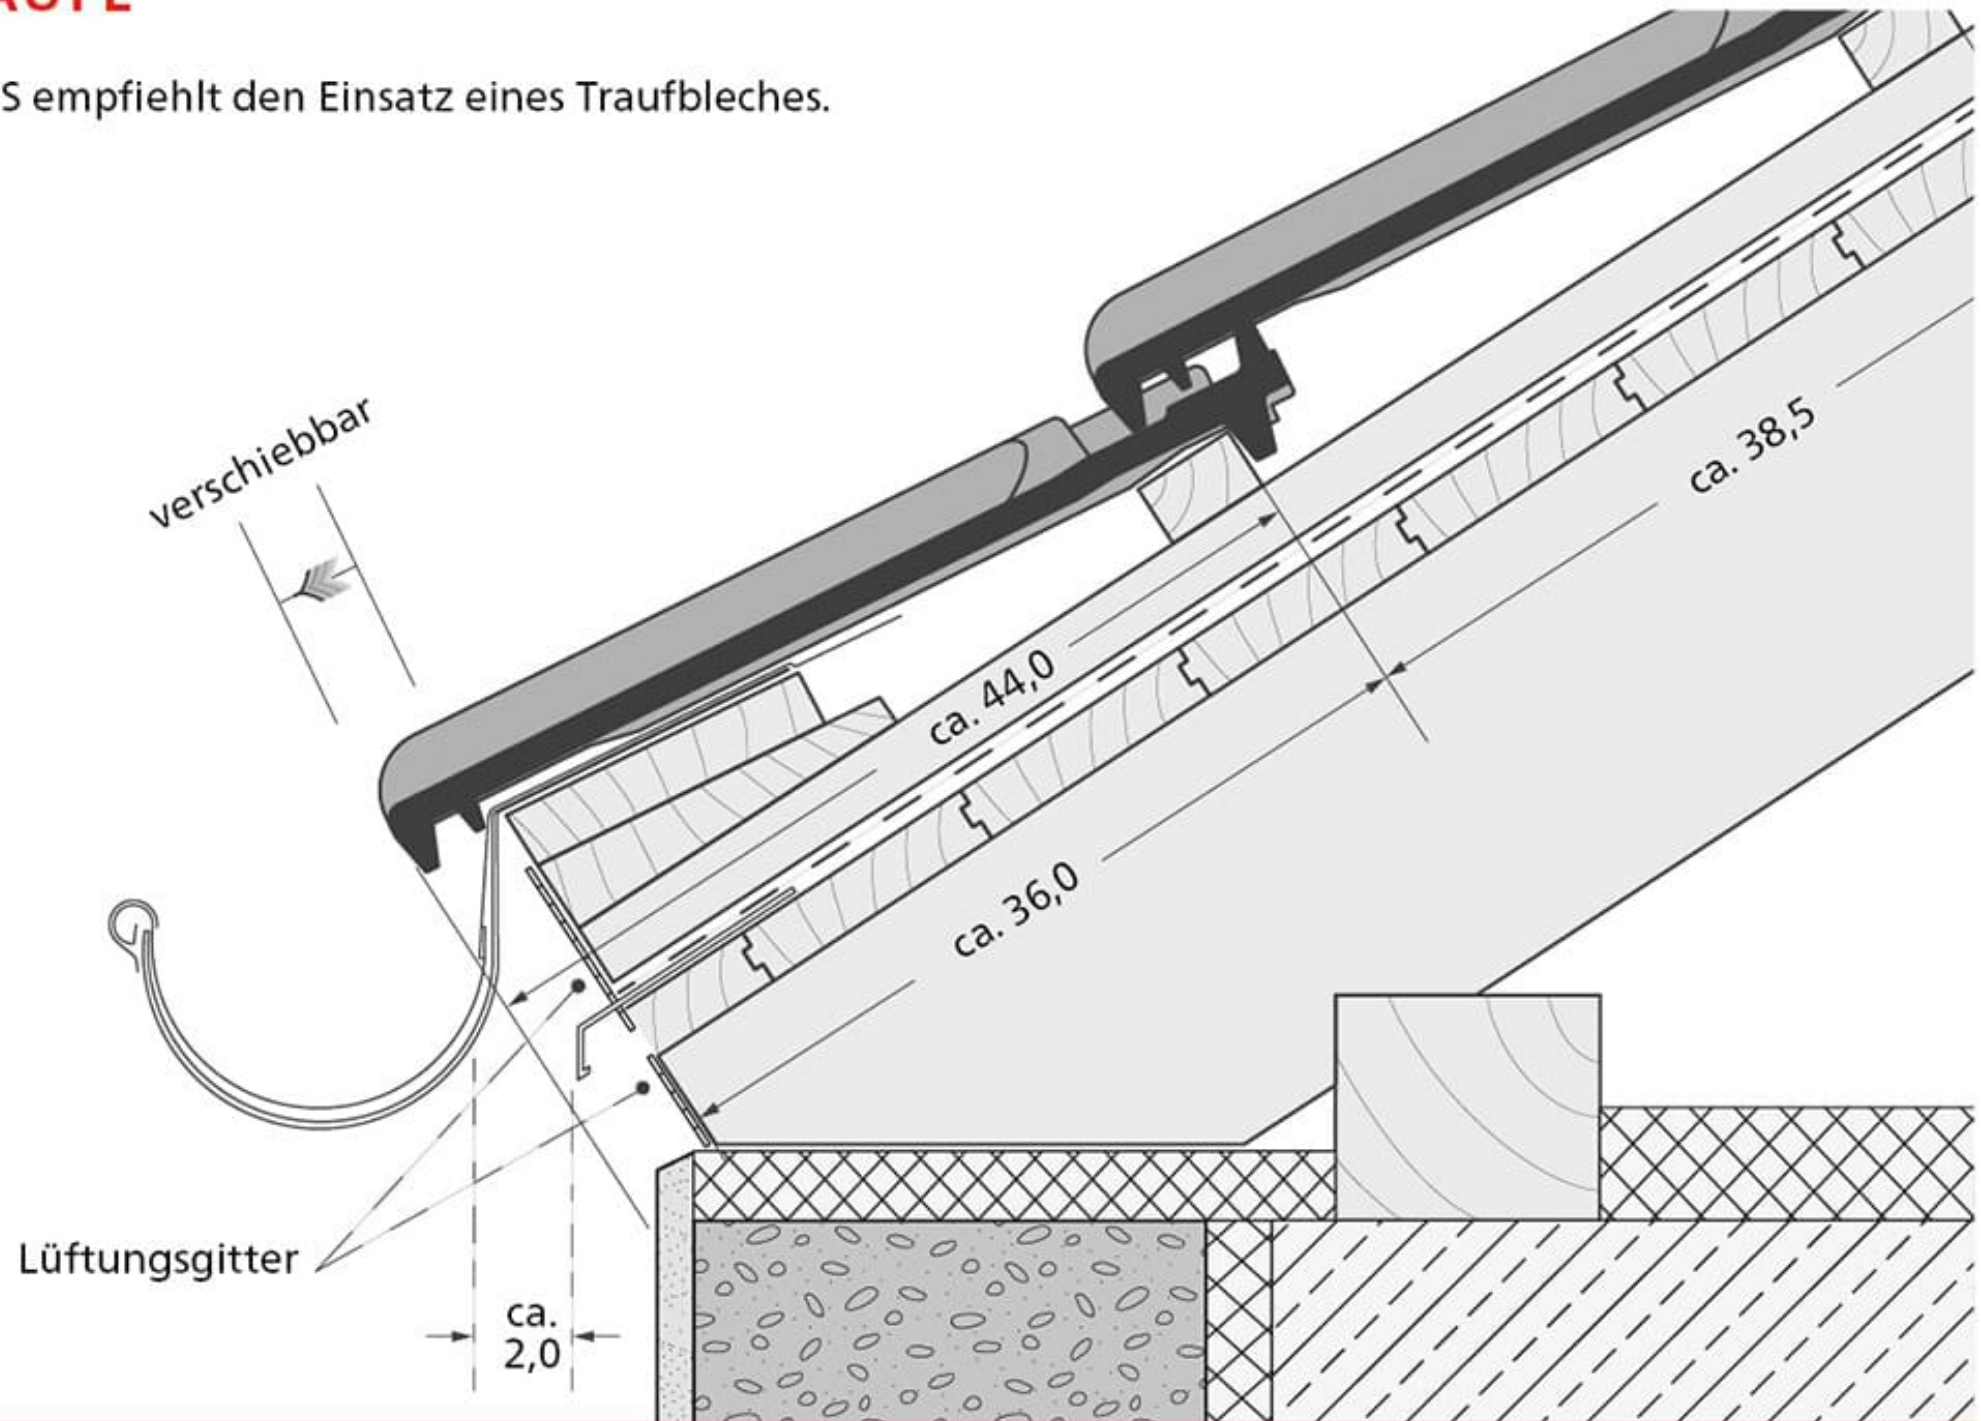

TRAUFE MIT ENTWÄSSERTEM UNTERDACH

ERLUS empfiehlt den Einsatz eines Traufbleches.

