


ERLUS Dachbegehungssystem

LATTWEITE < 37,5 cm

alle Maßangaben in cm

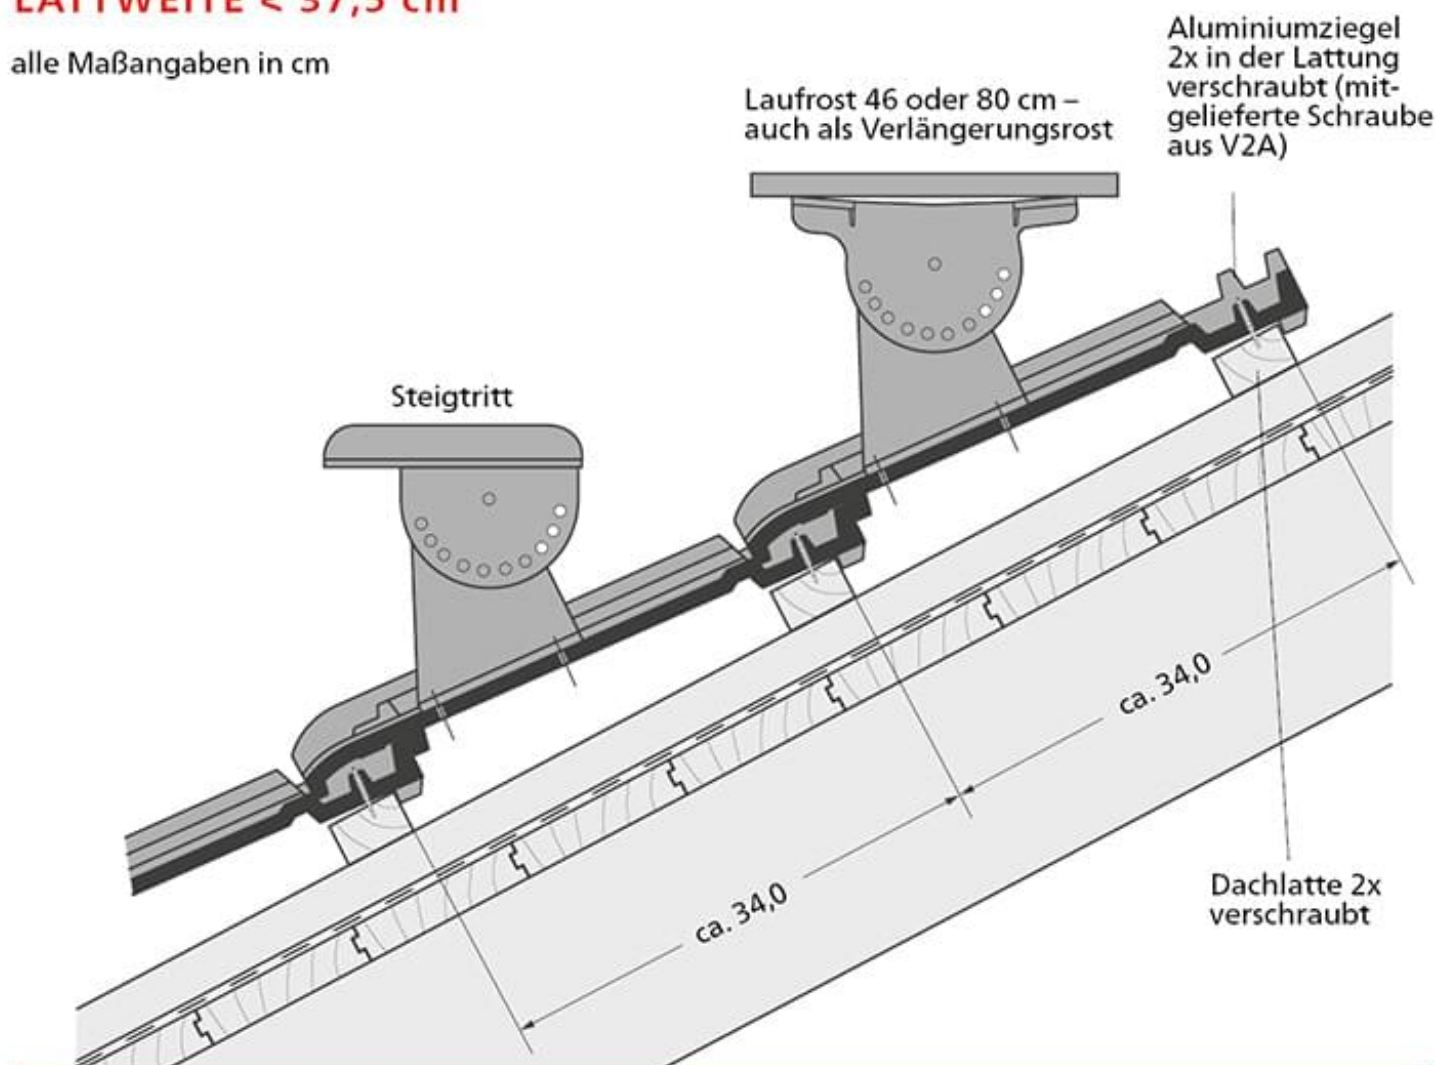

Zeichnung: E58

VERARBEITUNG VON TRITTFLÄCHEN UND ROSTEN NACH DIN 18160-5

ARTIKEL	$\leq 45^\circ$	$\geq 45^\circ$
Trittflächen (Roste 46 cm)	jede 2. Ziegelreihe	jede Ziegelreihe
Einzeltritt (Steigtritt)	jede Ziegelreihe	jede Ziegelreihe

aus nicht rostendem Stahl/Alu, geprüft nach DIN EN 516,


keine Stützlatte erforderlich

FIRSTZIEGEL NR. 18 MIT FIRSTANSCHLUSSZIEGEL

Um optimale Regensicherheit auch im Firstbereich garantieren zu können, ist bei Dachneigungen $< 30^\circ$ die Verwendung von Firstanschlussziegeln zu empfehlen.

Lüftung bis 2 x 12 m Sparrenlänge.

ERLUS First- und Gratlüfterband aus Alu kann zur Erhöhung der Flugschneesicherheit eingesetzt werden.

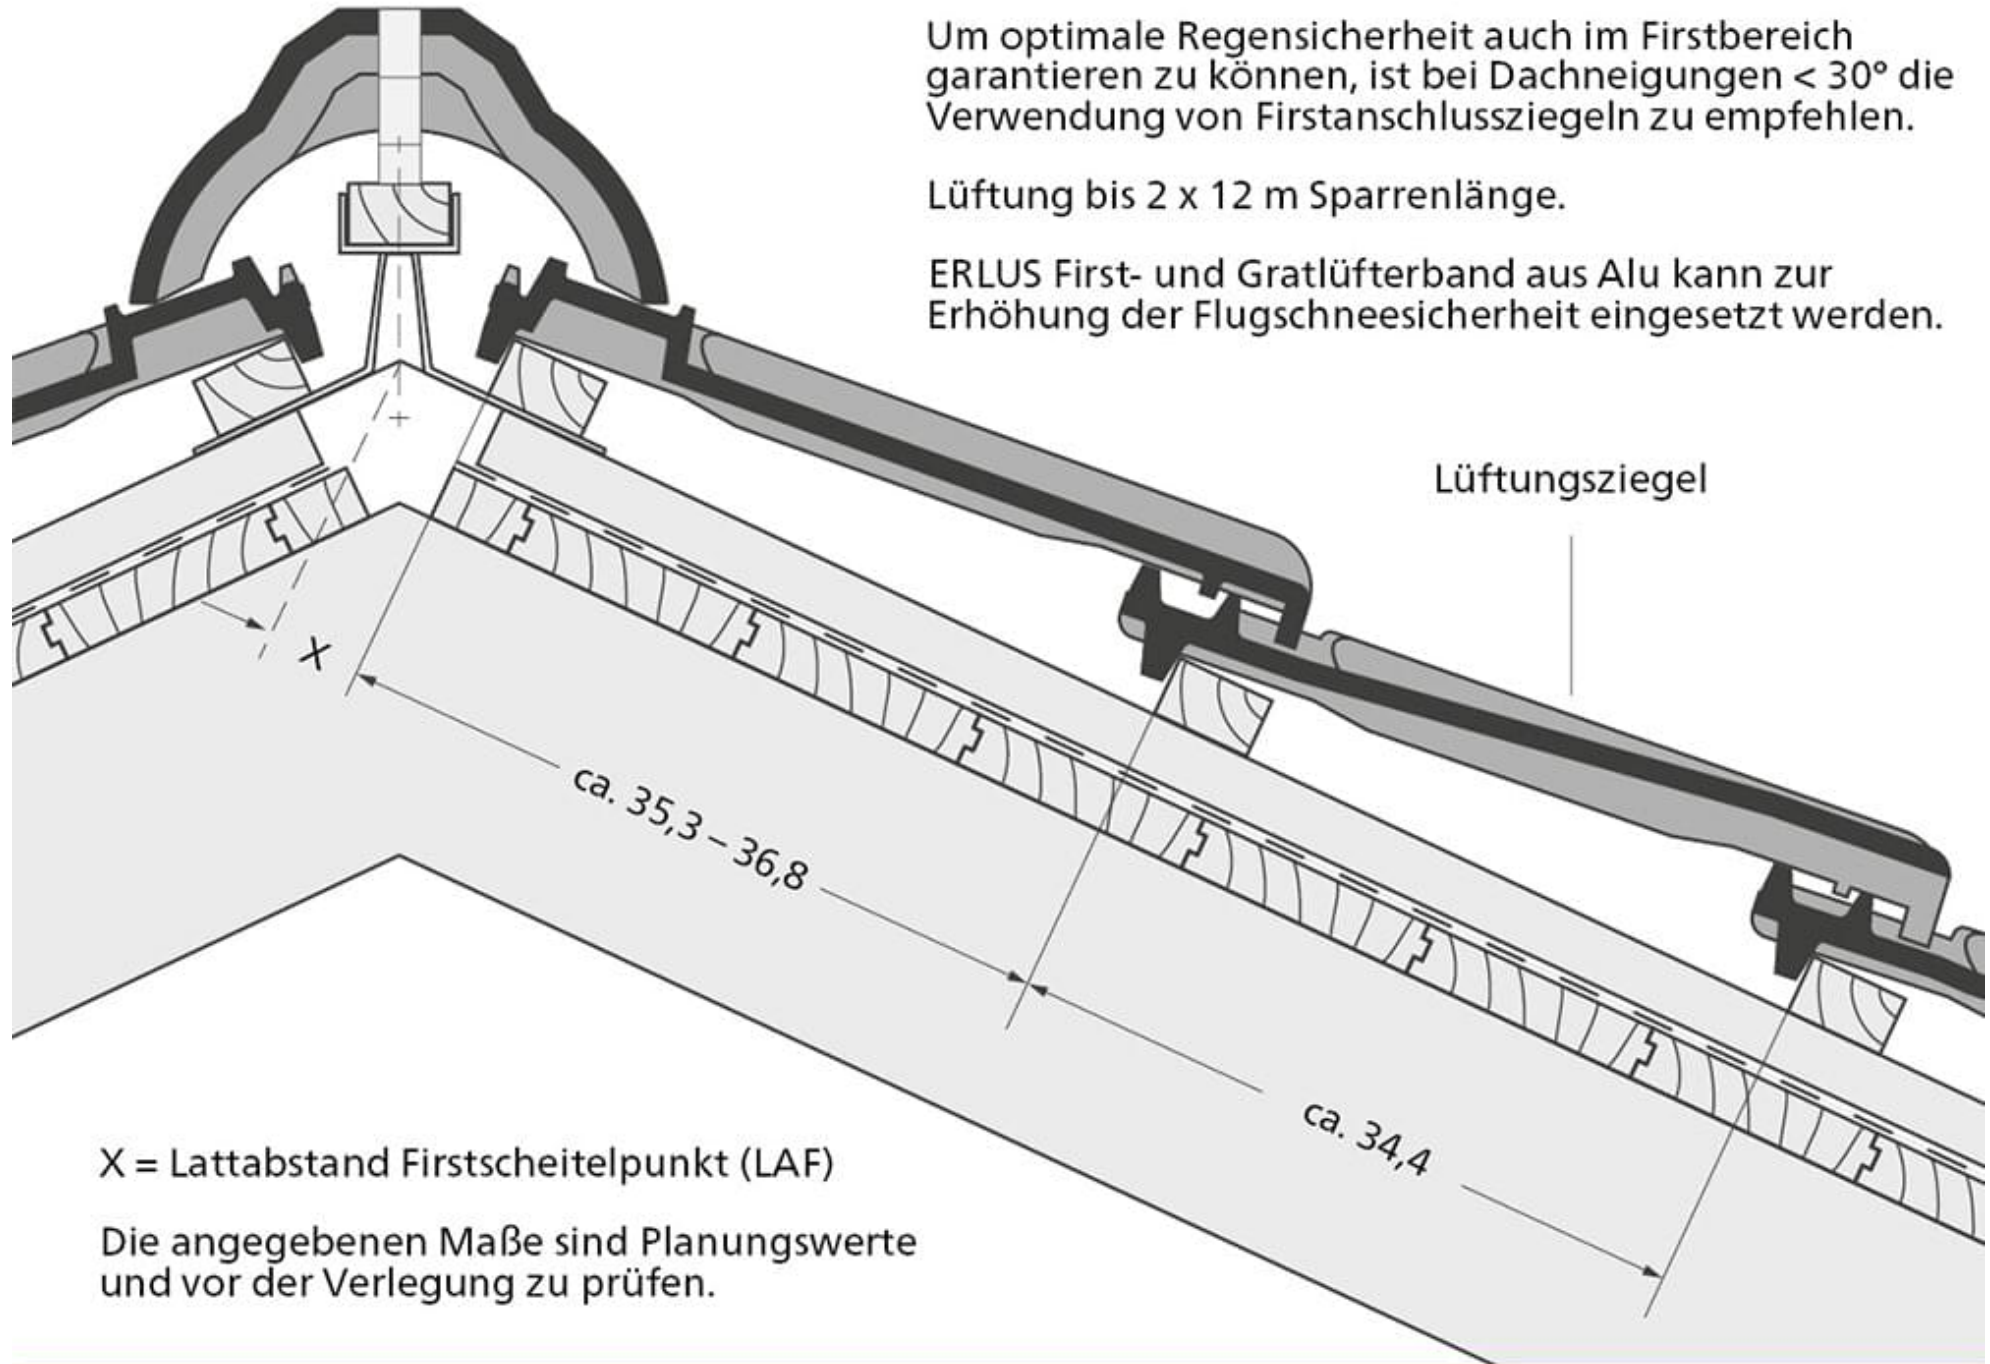


FIRSTZIEGEL NR. 18

Firstabschlussziegel
Nr. 18 geschnitten

Firstausgleichsziegel Nr. 18

Firstziegel Nr. 18
2,6 Stck./lfm.

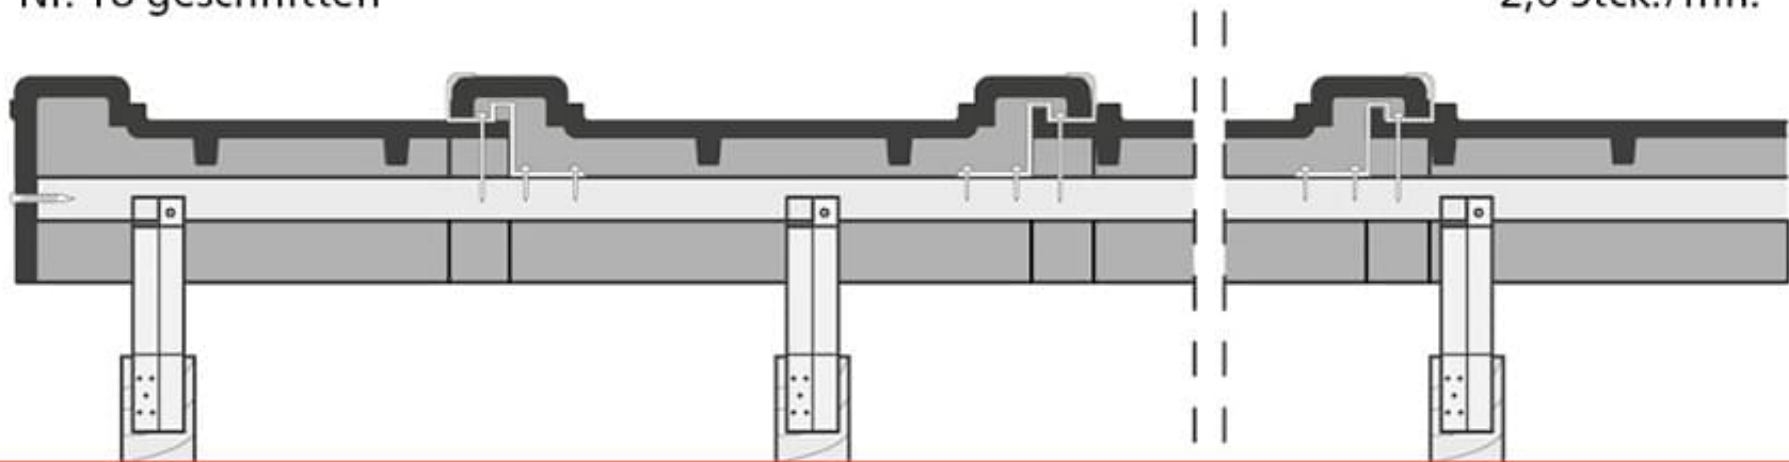


FIRSTLÜFTERZIEGEL NR. 19 LÜ

Firstziegel: 2,8 Stck./lfm.

Firstanfangsziegel

Hauptwetterrichtung


Firstendziegel

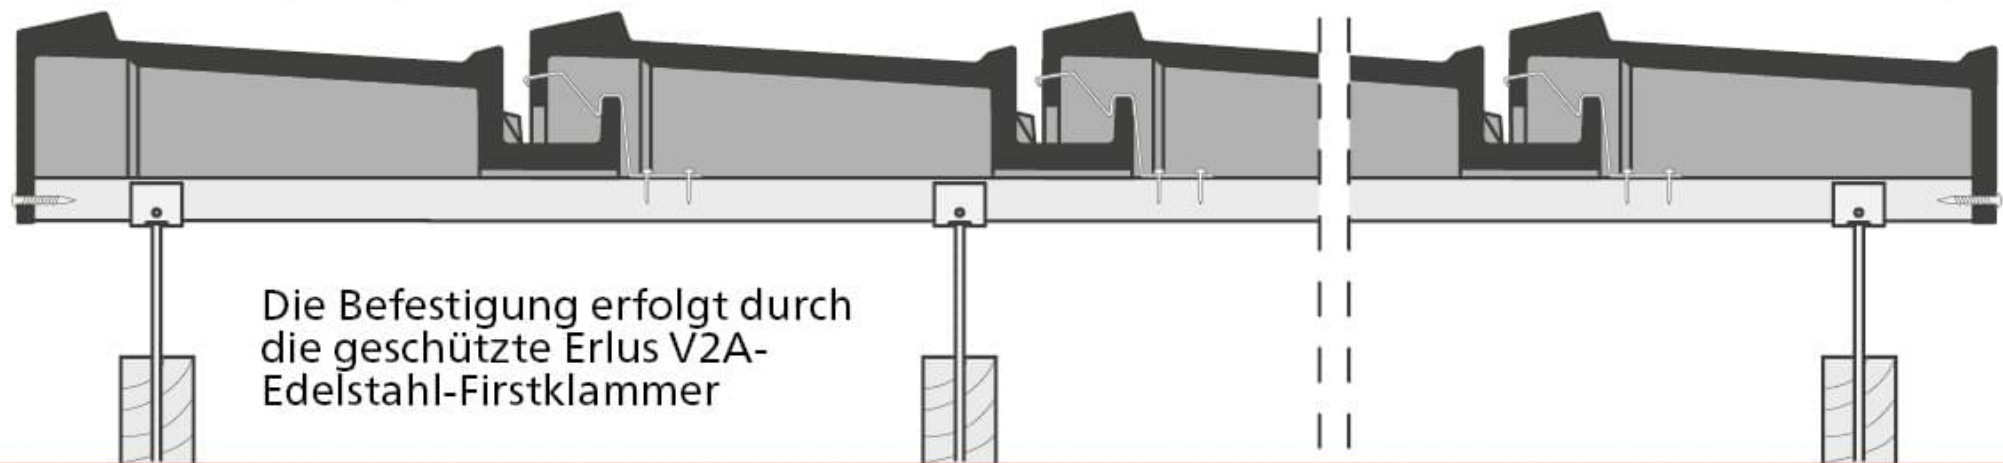

Die Befestigung erfolgt durch die geschützte Erlus V2A-Edelstahl-Firstklammer


LINKER ORTGANG*

*bei flacher Dachneigung Verschraubungsloch im Ortgang dauerelastisch
(z. B. mit Spenglerschrauben) abdichten

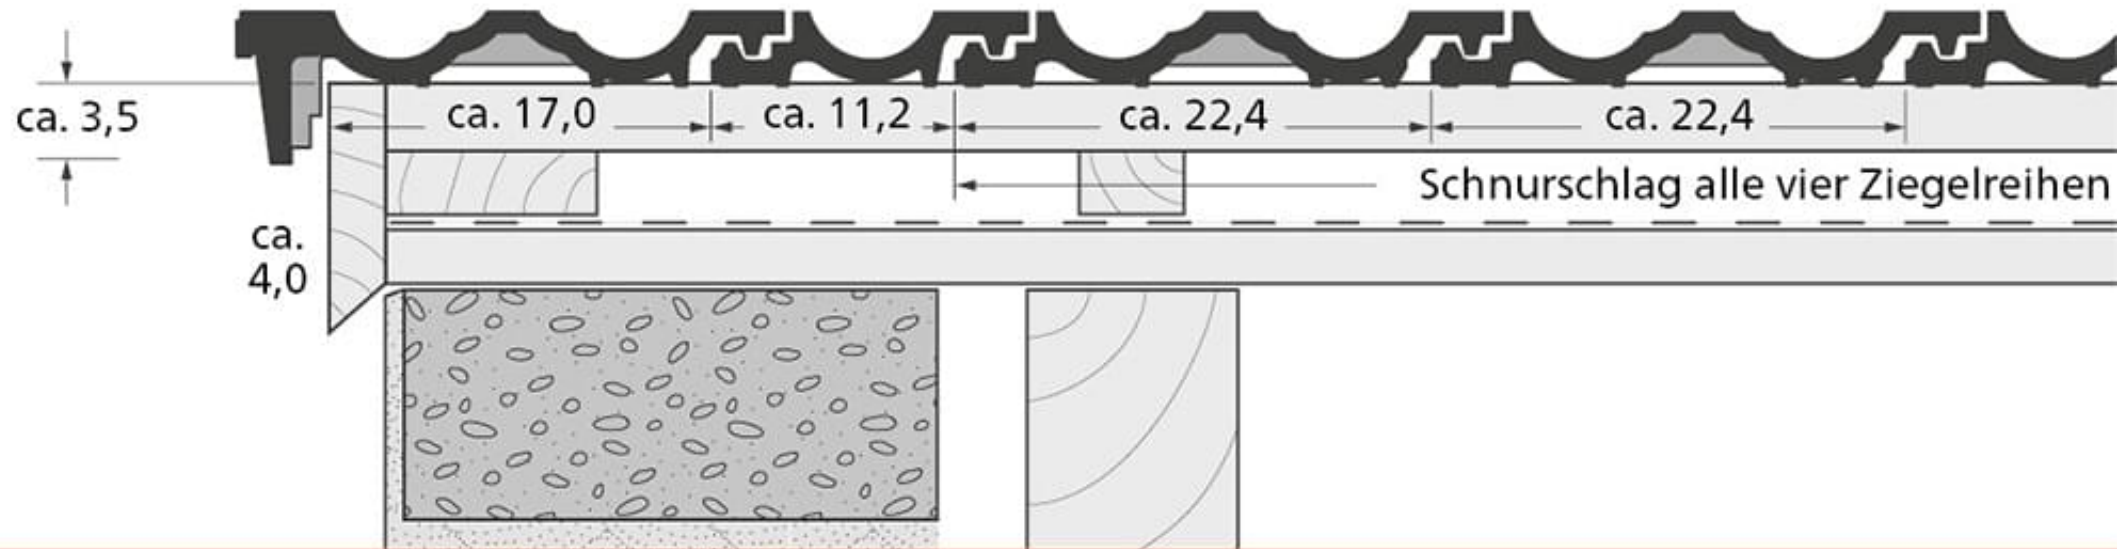


RECHTER ORTGANG*

*bei flacher Dachneigung Verschraubungsloch im Ortgang dauerelastisch
(z. B. mit Spenglerschrauben) abdichten

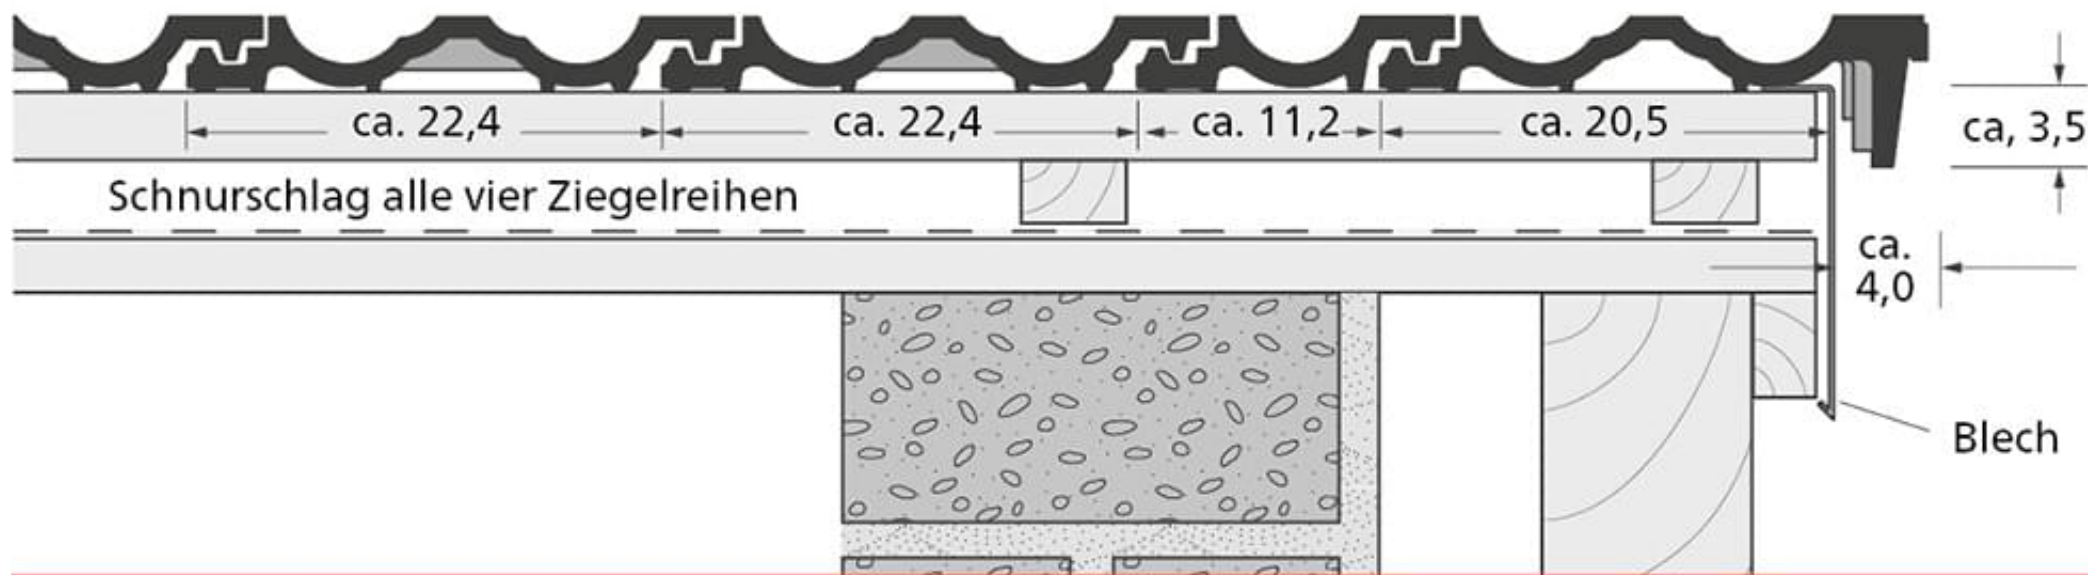

TRAUFE

ERLUS empfiehlt den Einsatz eines Traufbleches.

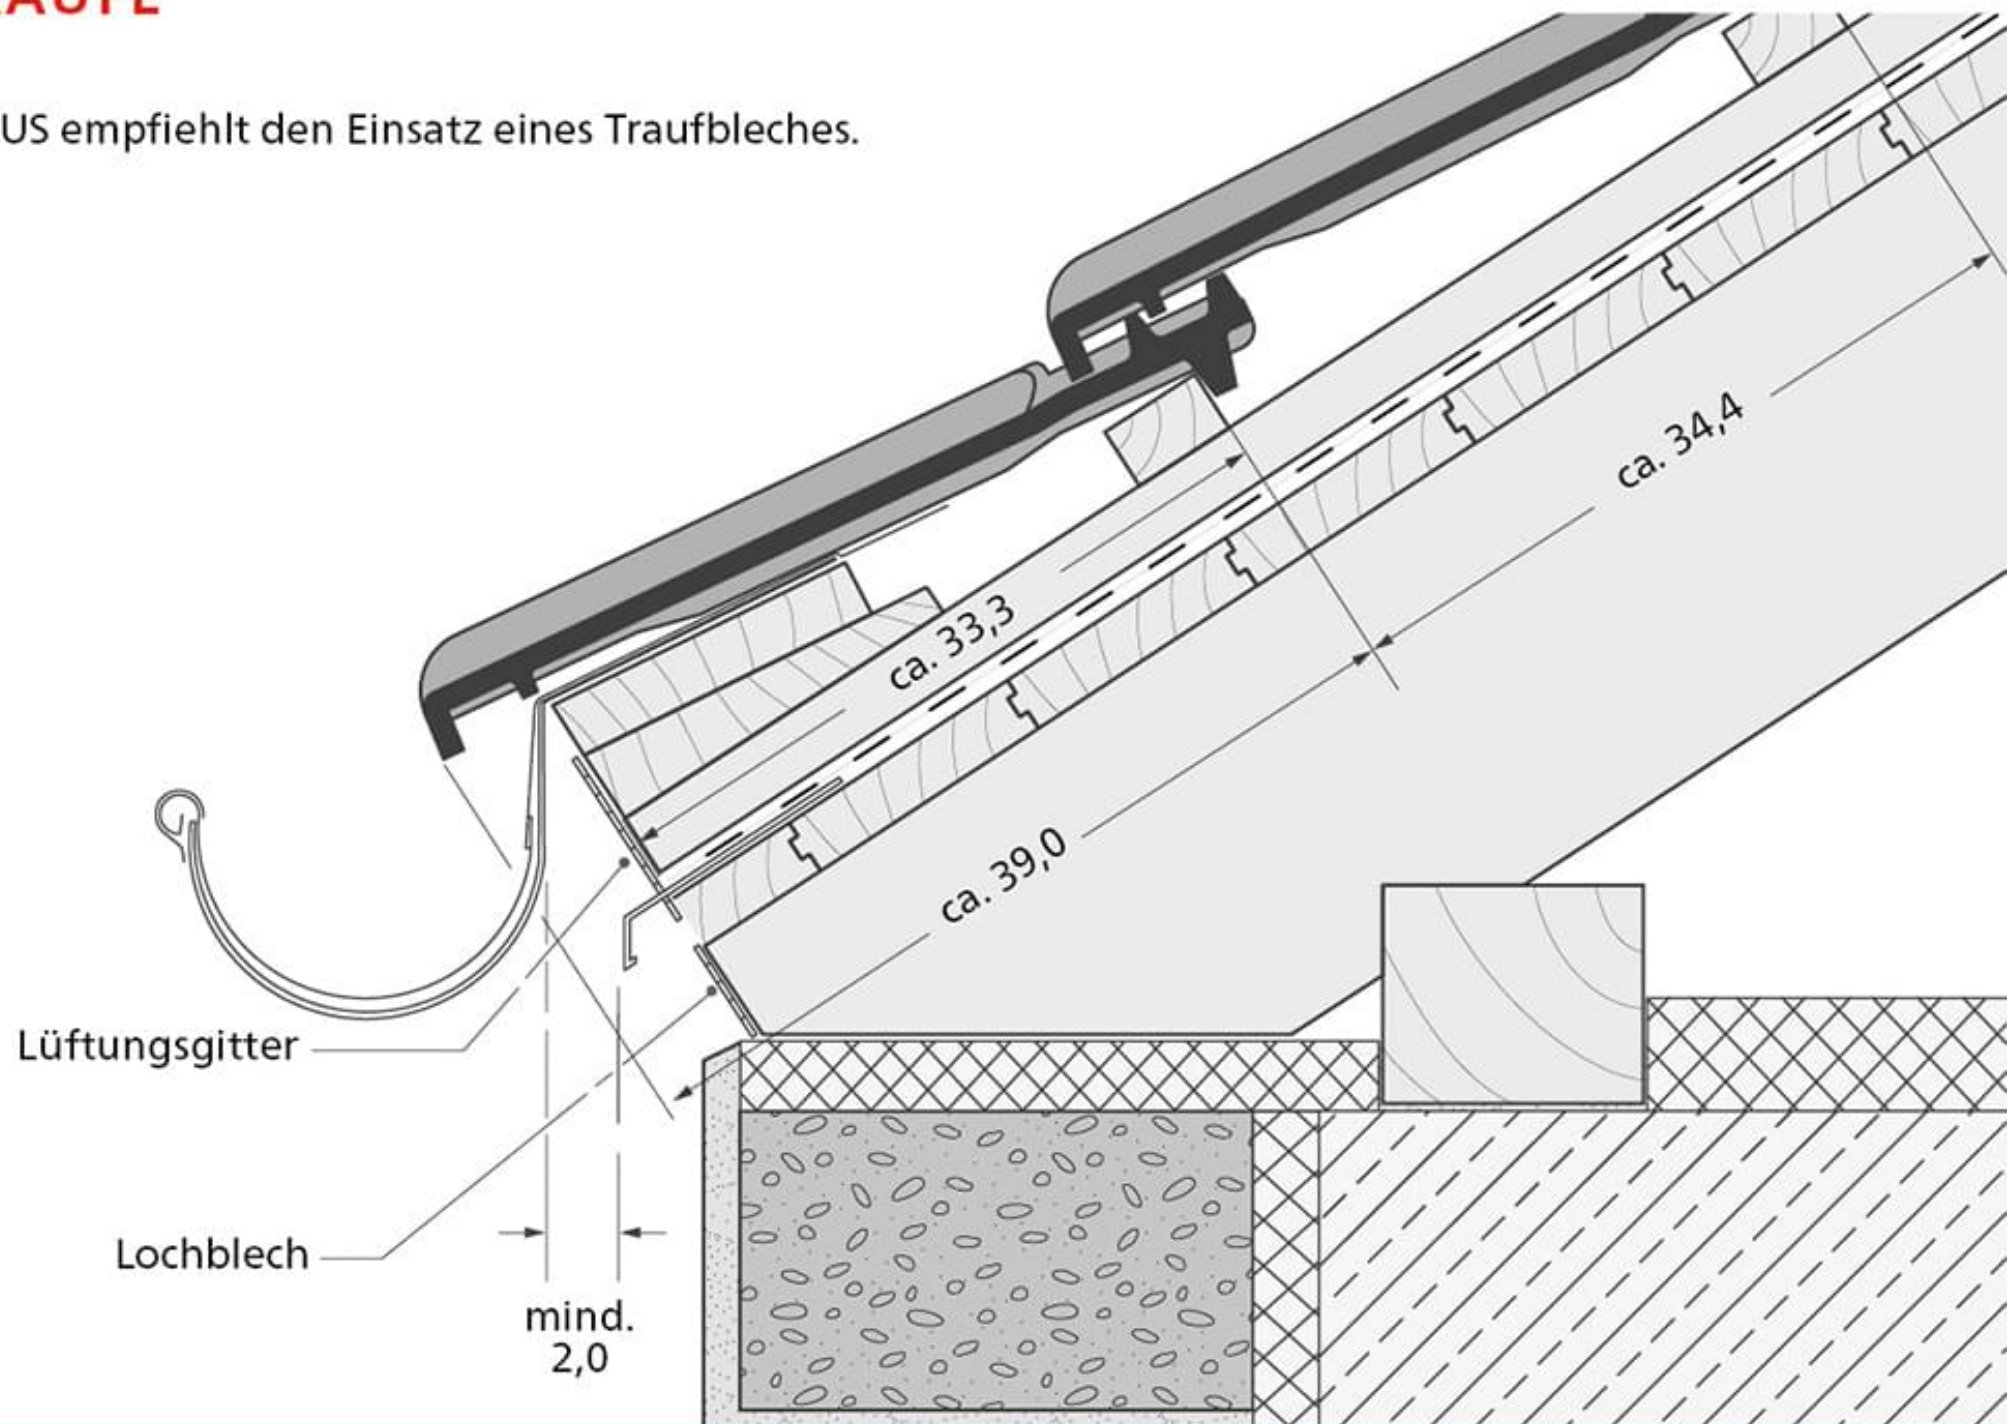

TRAUFE MIT ENTWÄSSERTEM UNTERDACH

ERLUS empfiehlt den Einsatz eines Traufbleches.

