


ERLUS Dachbegehungssystem

LATTWEITE < 37,5 cm

alle Maßangaben in cm

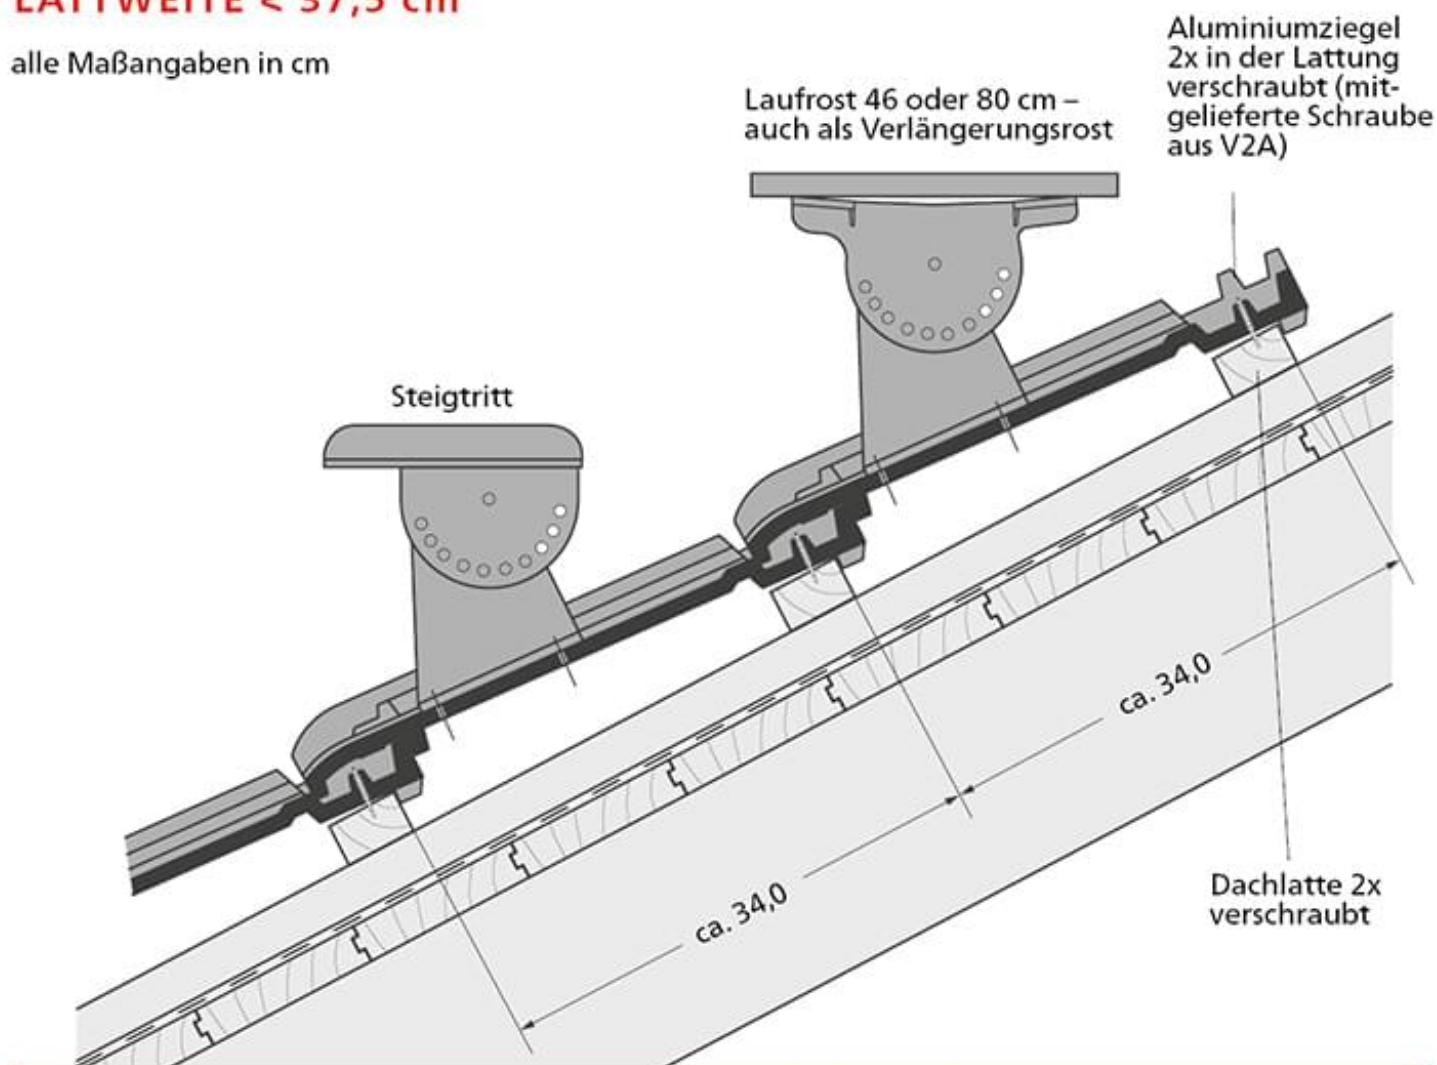

Zeichnung: E58


VERARBEITUNG VON TRITTFLÄCHEN UND ROSTEN NACH DIN 18160-5

ARTIKEL	$\leq 45^\circ$	$\geq 45^\circ$
Trittflächen (Roste 46 cm)	jede 2. Ziegelreihe	jede Ziegelreihe
Einzeltritt (Steigtritt)	jede Ziegelreihe	jede Ziegelreihe

aus nicht rostendem Stahl/Alu, geprüft nach DIN EN 516,

keine Stützlatte erforderlich

FIRSTLÜFTERZIEGEL NR. 19 LÜ MIT FIRSTANSCHLUSSZIEGEL

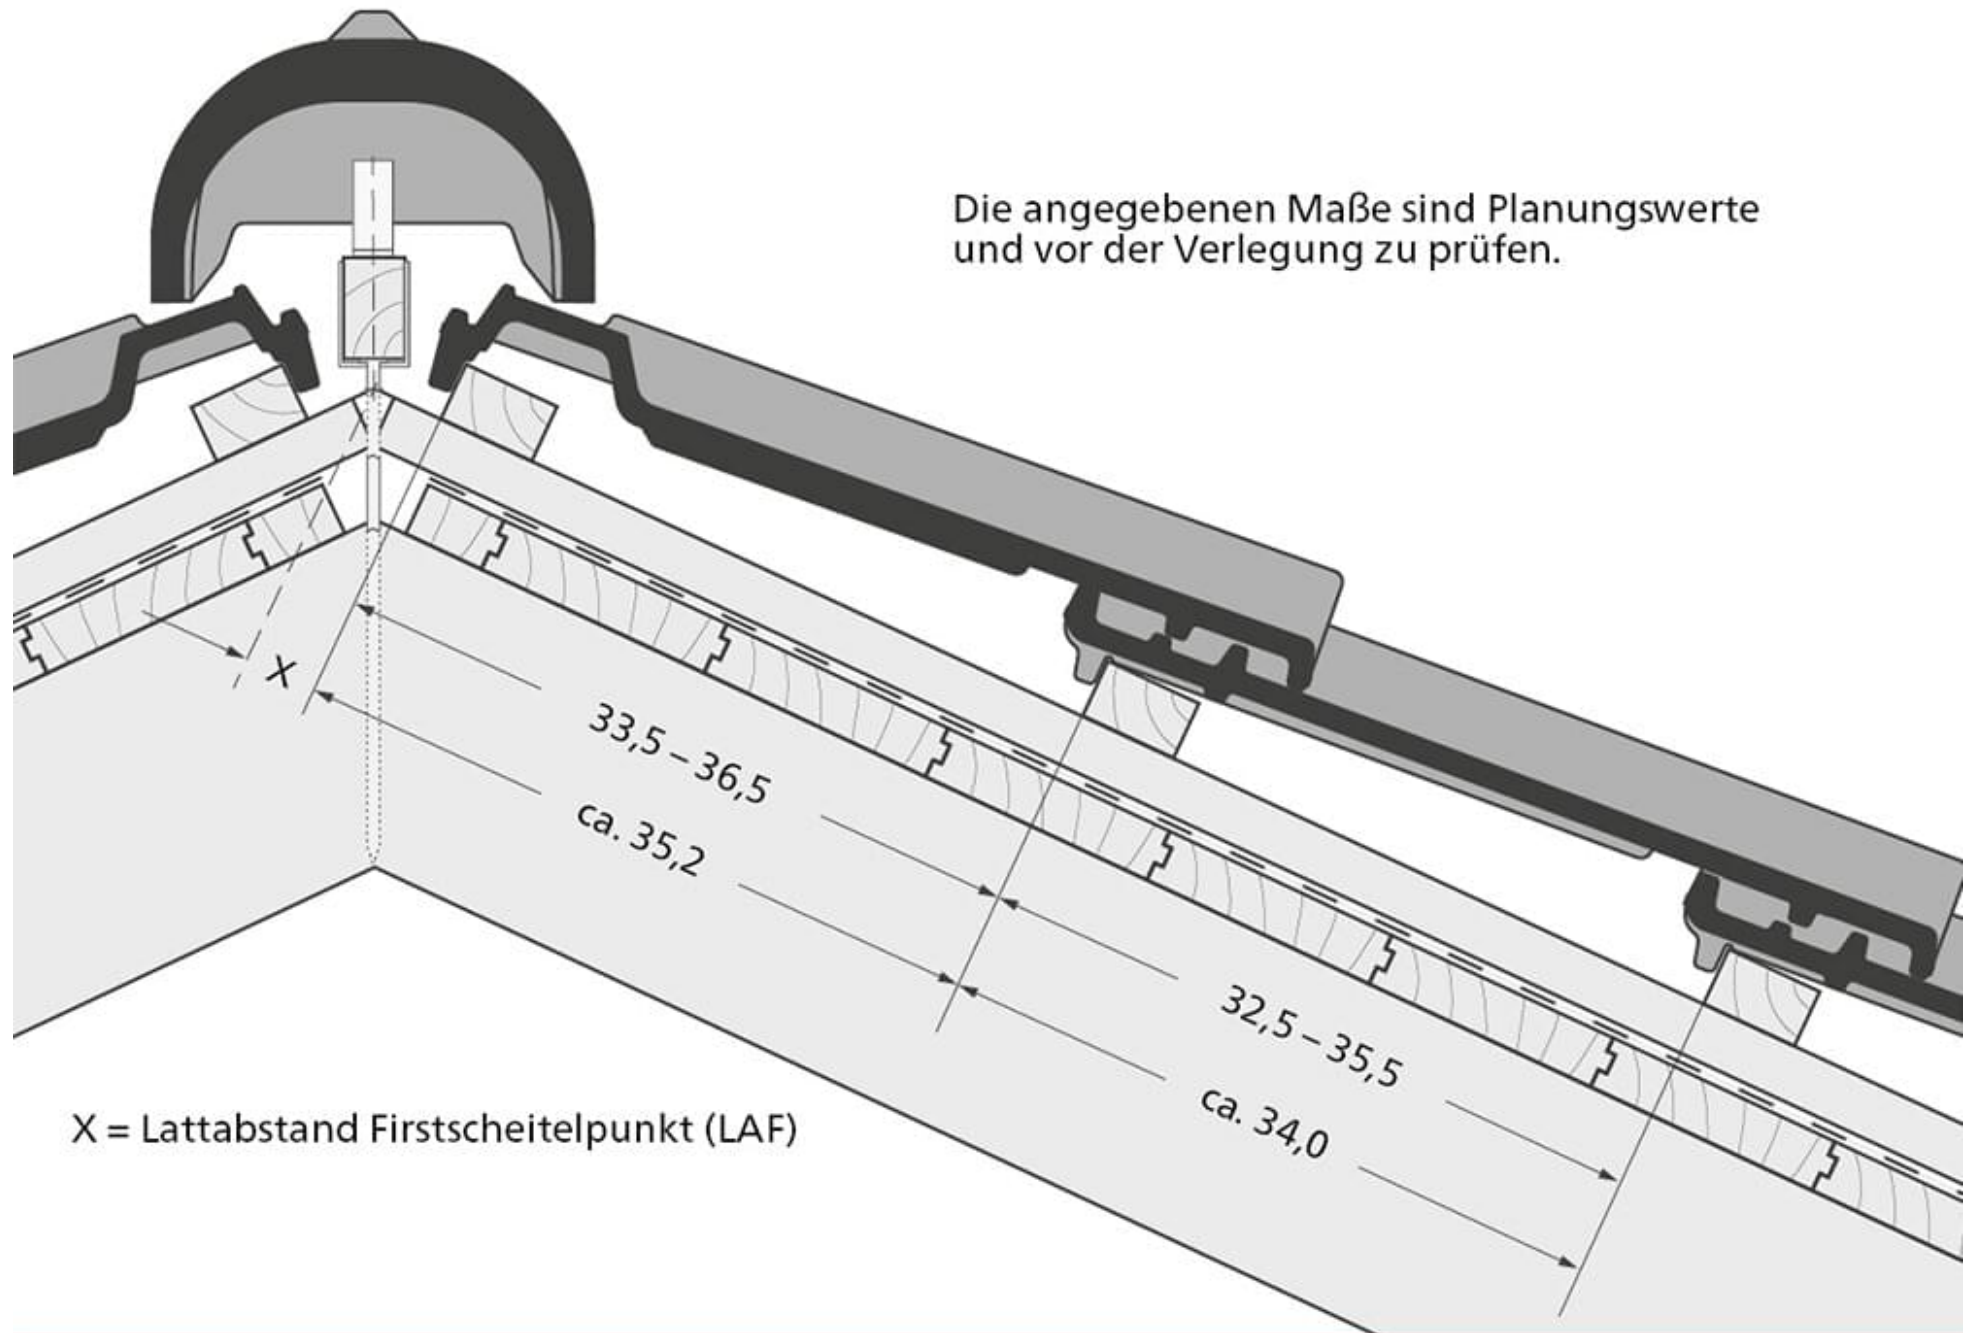


FIRSTLÜFTERZIEGEL NR. 19 LÜ

Firstziegel: 2,8 Stck./lfm.

Firstanfangsziegel


Hauptwetterrichtung

Firstendziegel

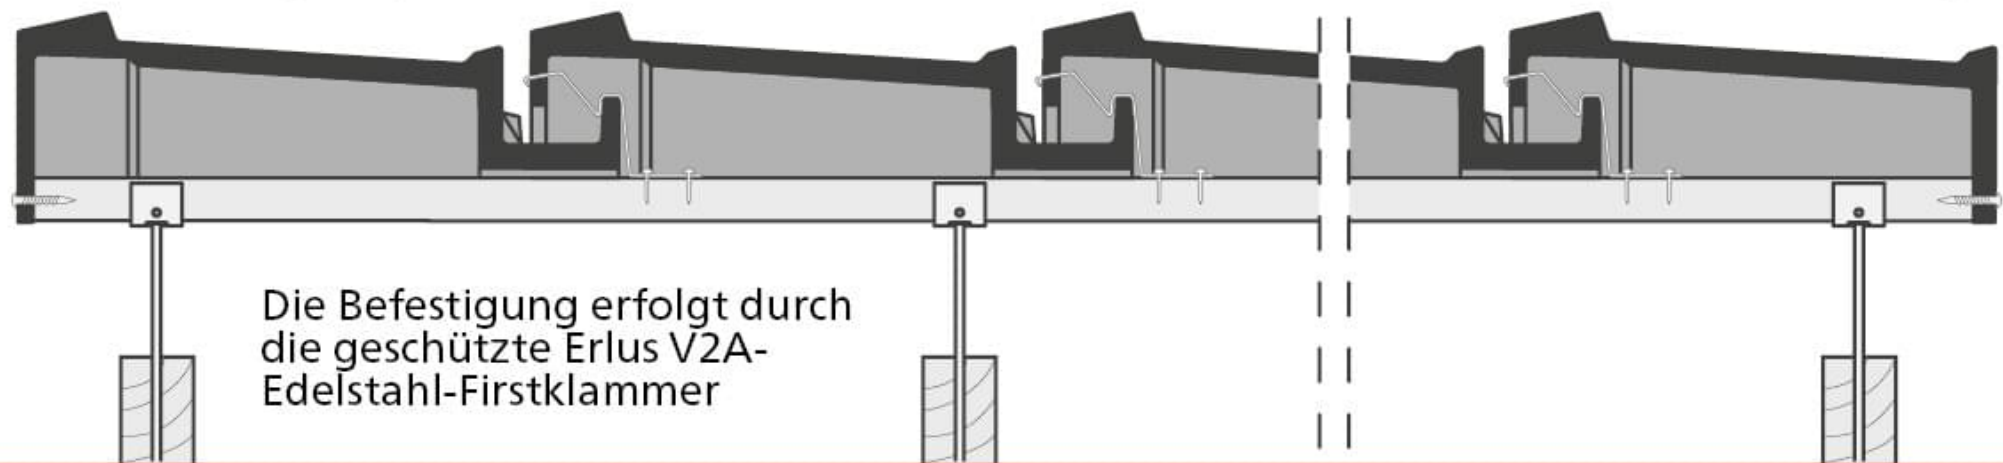


Die Befestigung erfolgt durch die geschützte Erlus V2A-Edelstahl-Firstklammer

FIRSTZIEGEL NR. 15

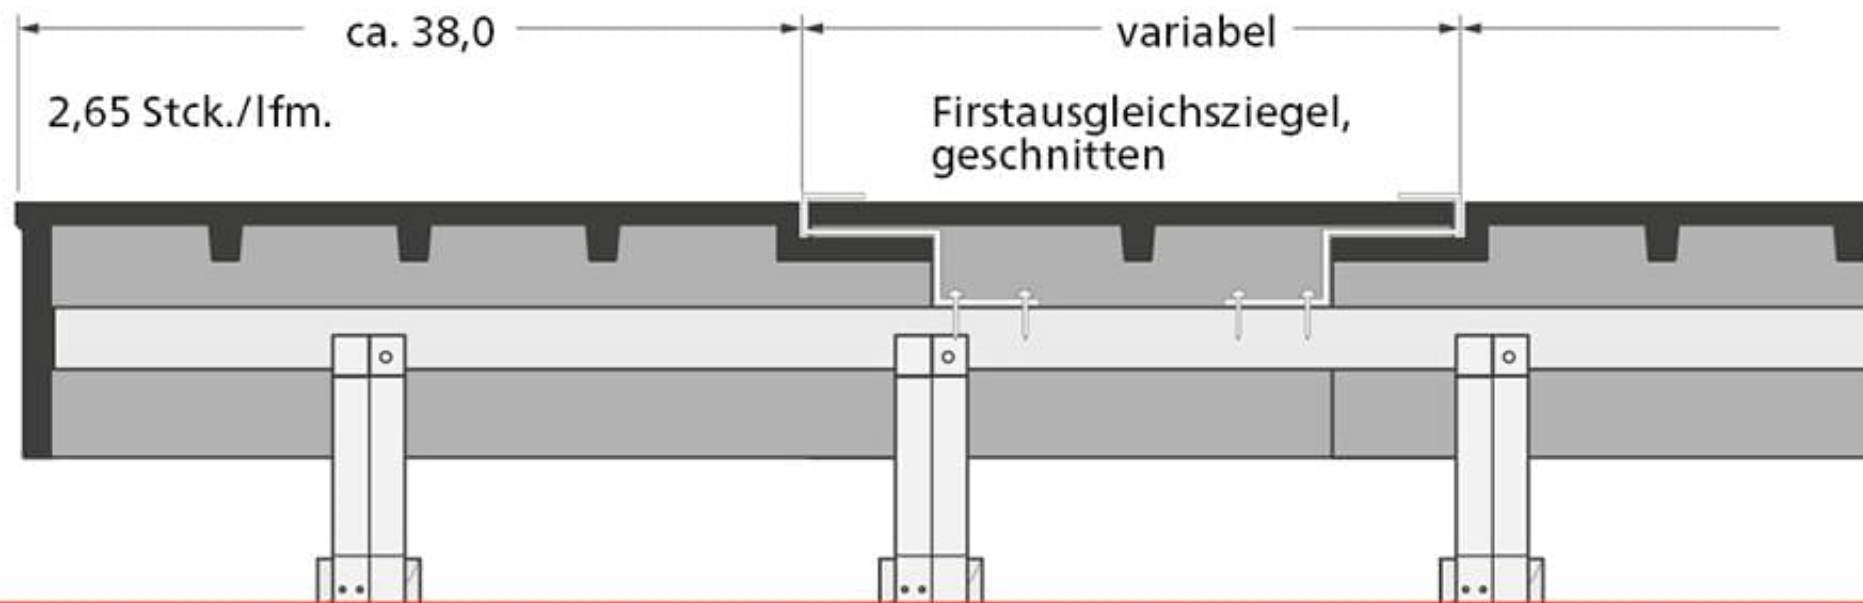


LINKER ORTGANG*

*bei flacher Dachneigung Verschraubungsloch im Ortgang dauerelastisch
(z. B. mit Spenglerschrauben) abdichten

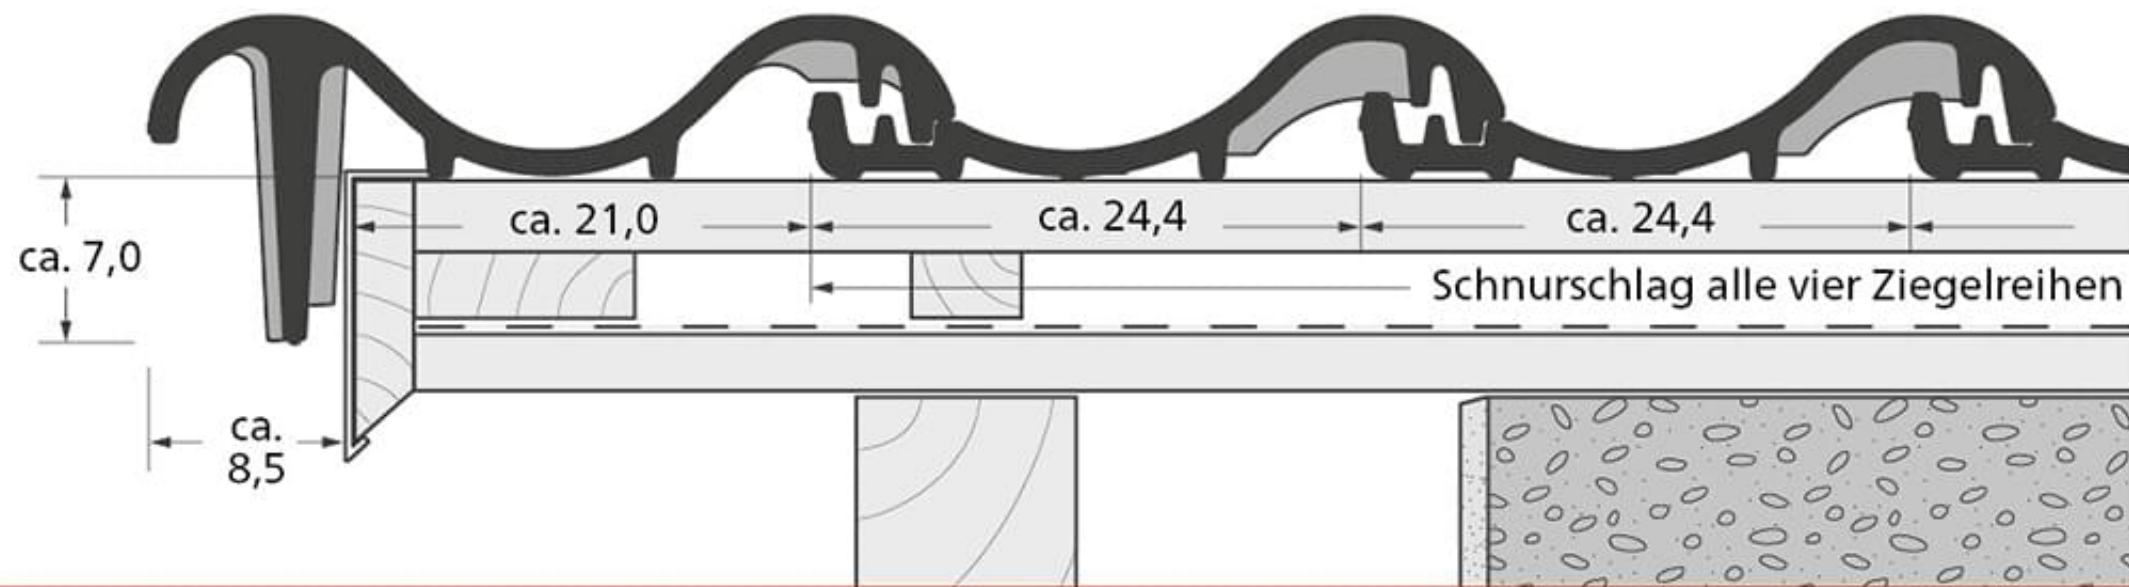


RECHTER ORTGANG*

*bei flacher Dachneigung Verschraubungsloch im Ortgang dauerelastisch
(z. B. mit Spenglerschrauben) abdichten

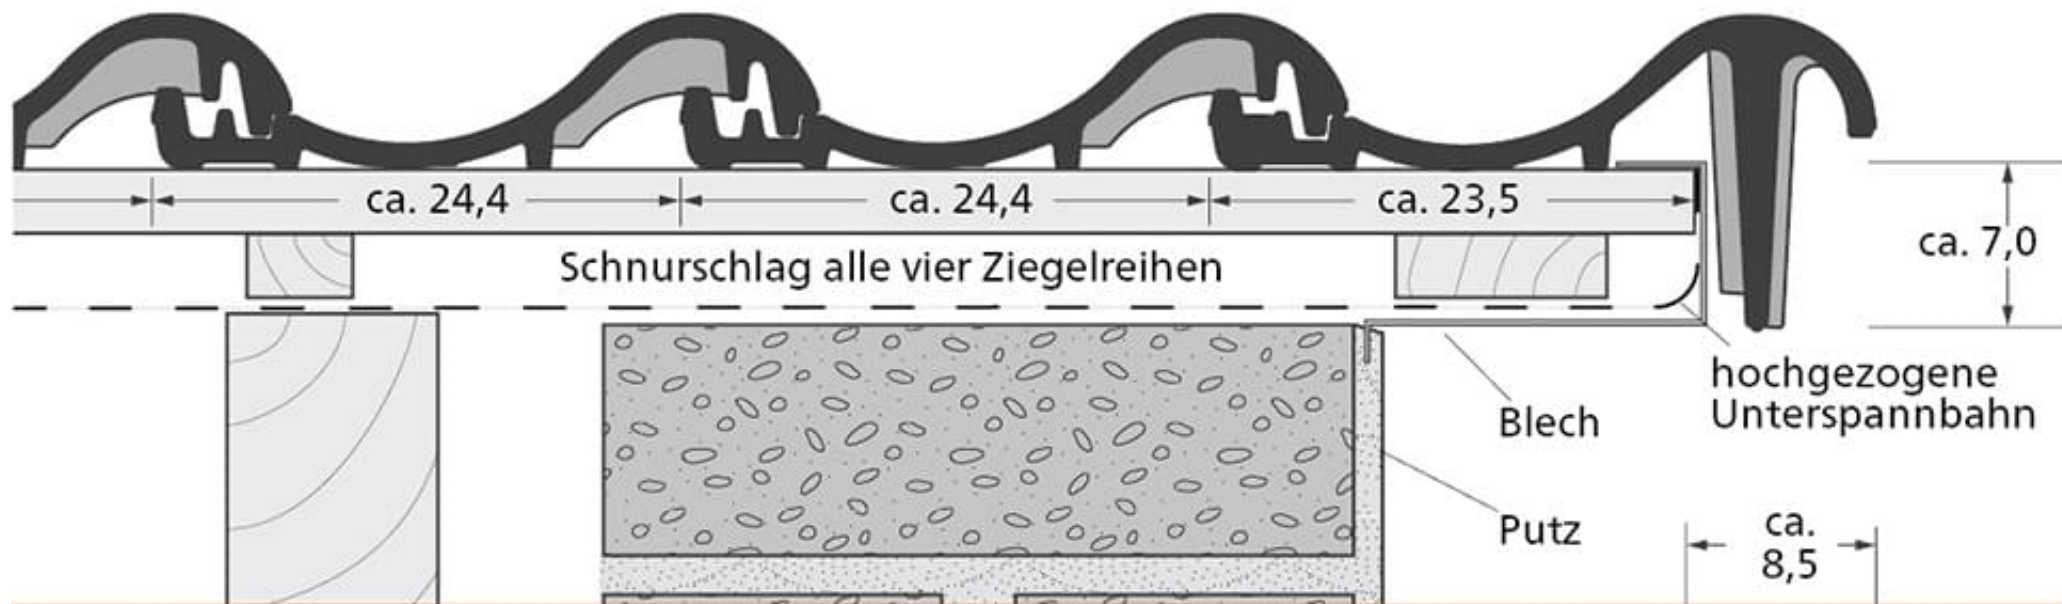

TRAUFE MIT ENTWÄSSERTEM UNTERDACH

ERLUS empfiehlt den Einsatz eines Traufbleches.

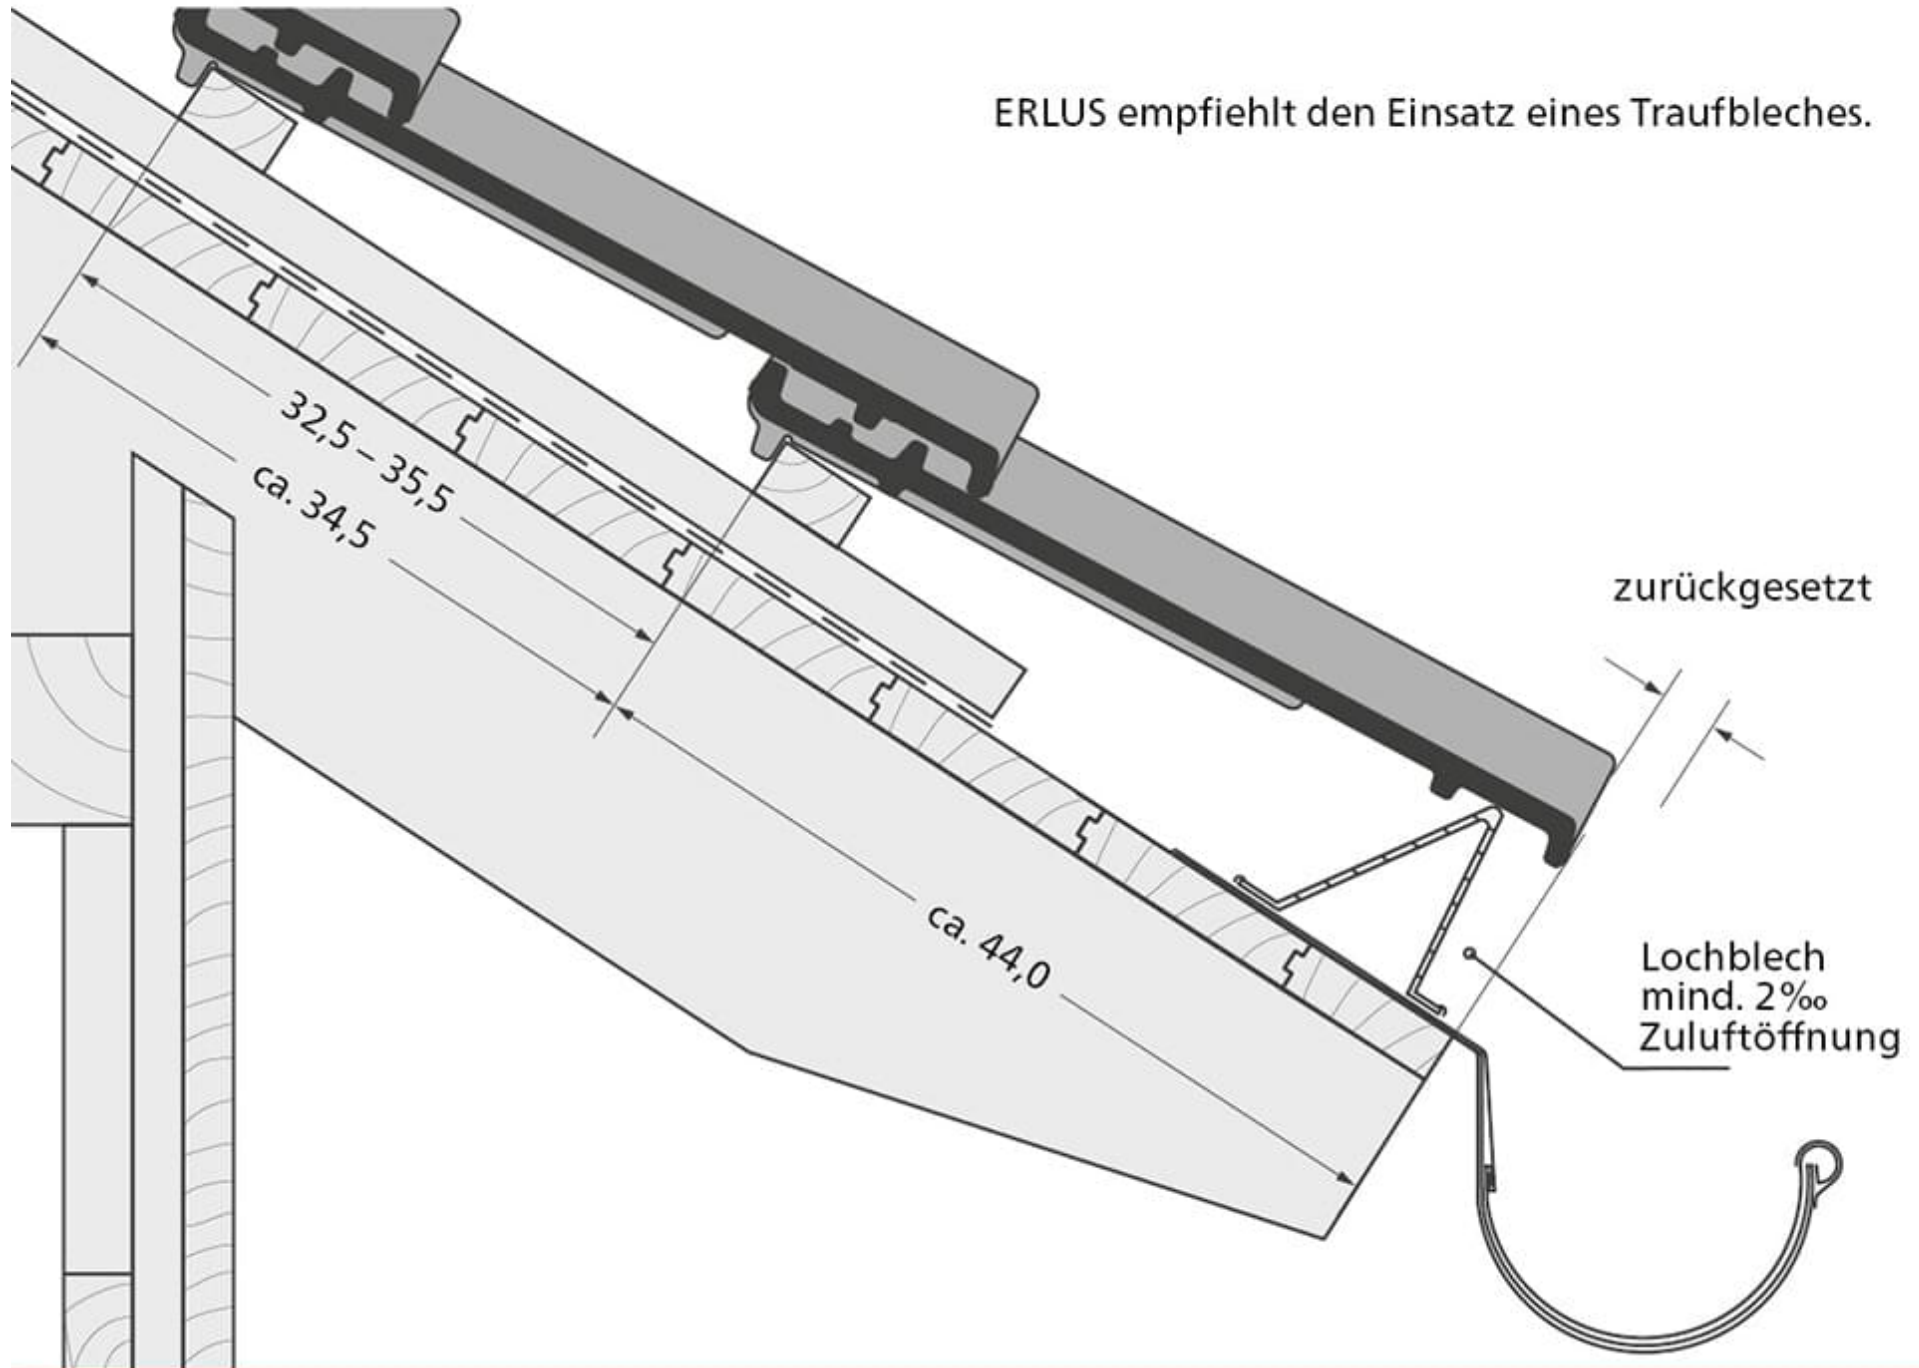

TRAUFE MIT AUFSPARRENDÄMMUNG

ERLUS empfiehlt den Einsatz eines Traufbleches.

