


FIRSTLÜFTERZIEGEL NR. 17 MIT FIRSTANSCHLUSSZIEGEL

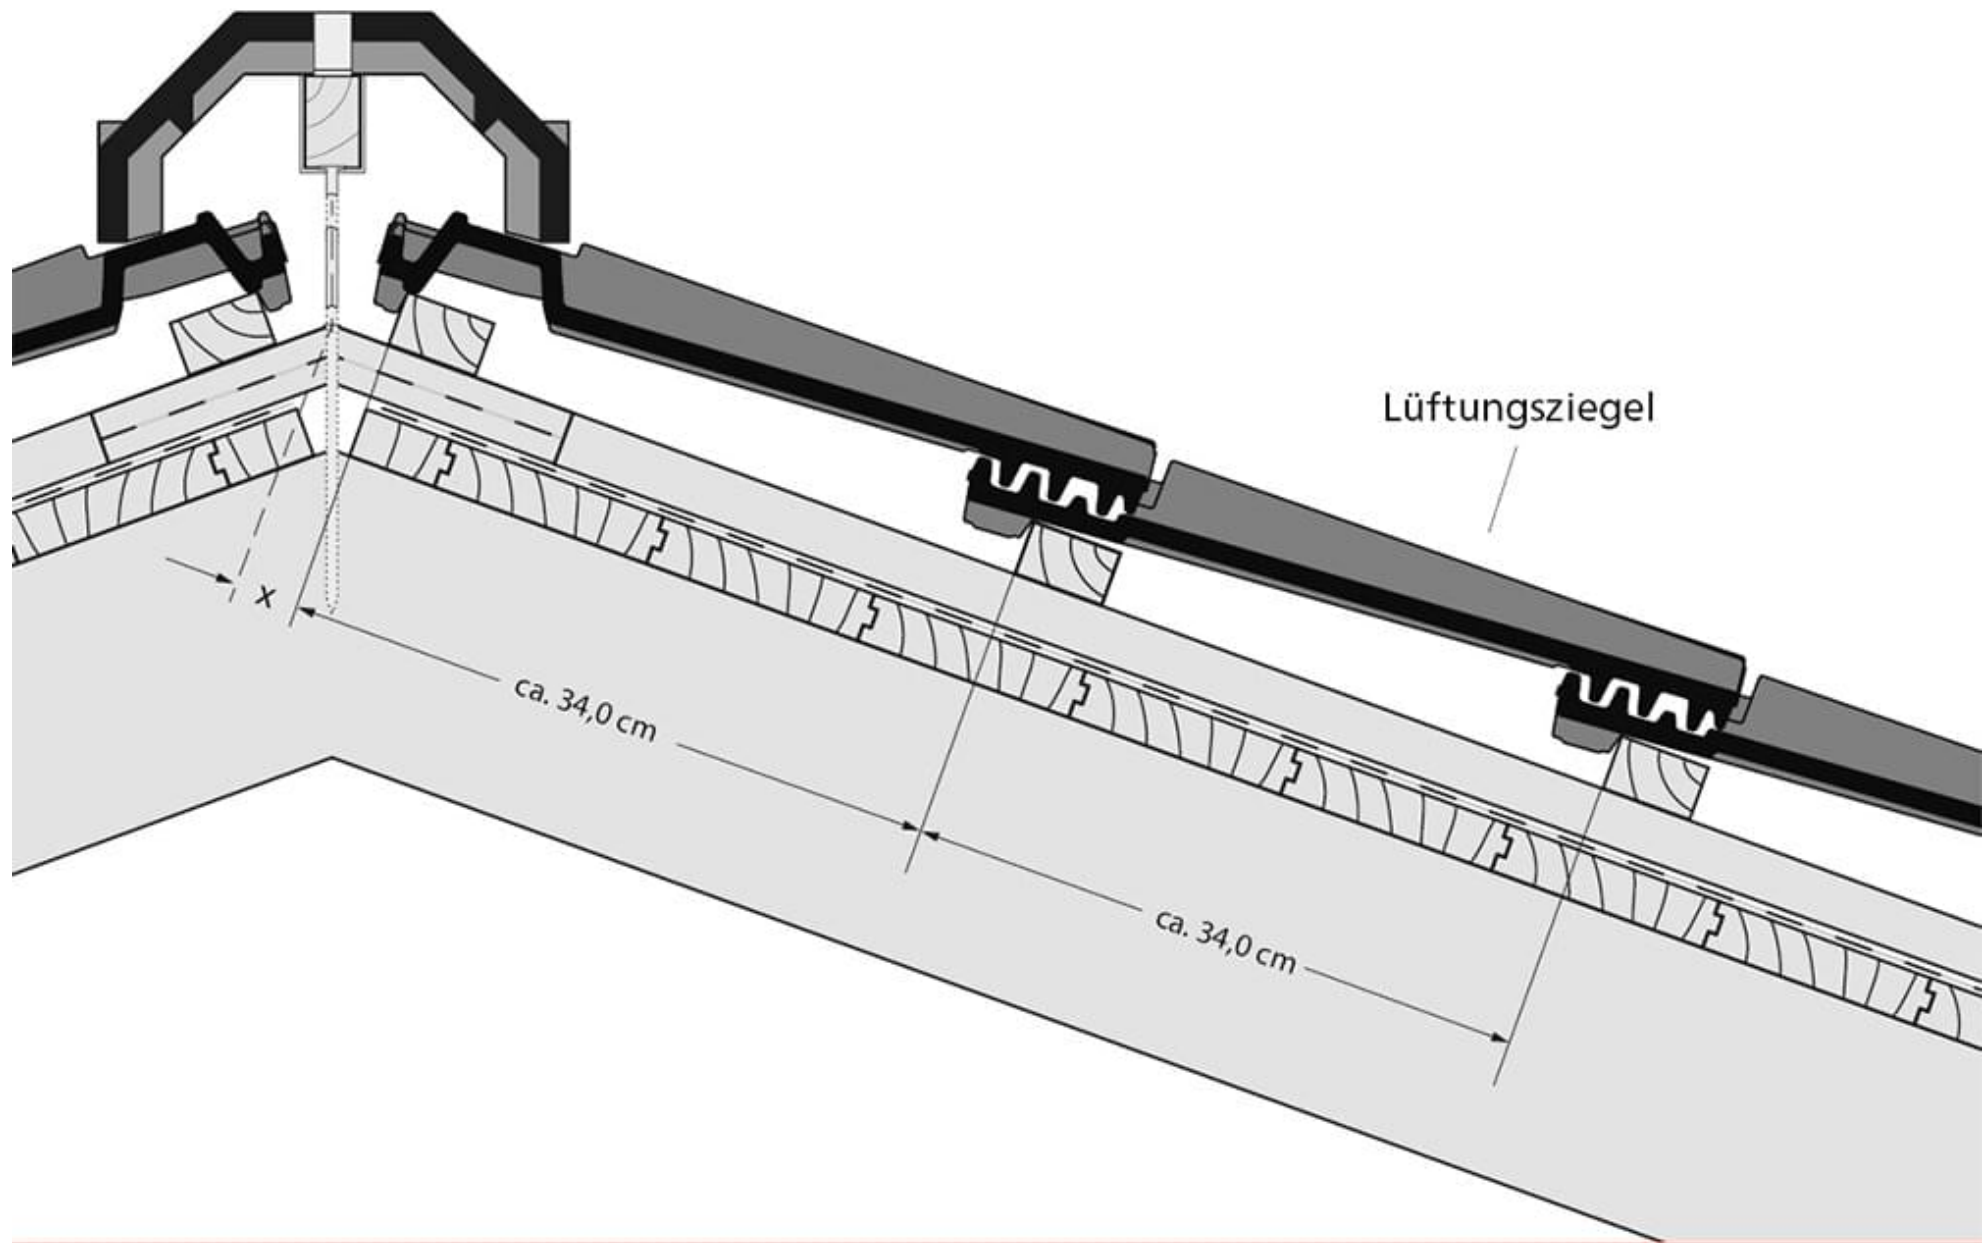


FIRSTLÜFTERZIEGEL NR. 17 LÜ

Für die funktions- und flugschneesichere Unterdrucklüftung bis 10 m Sparrenlänge
2,5 Stck./lfm.


ca. 3,5 cm
verschiebbar/lfm.

Hauptwetterrichtung

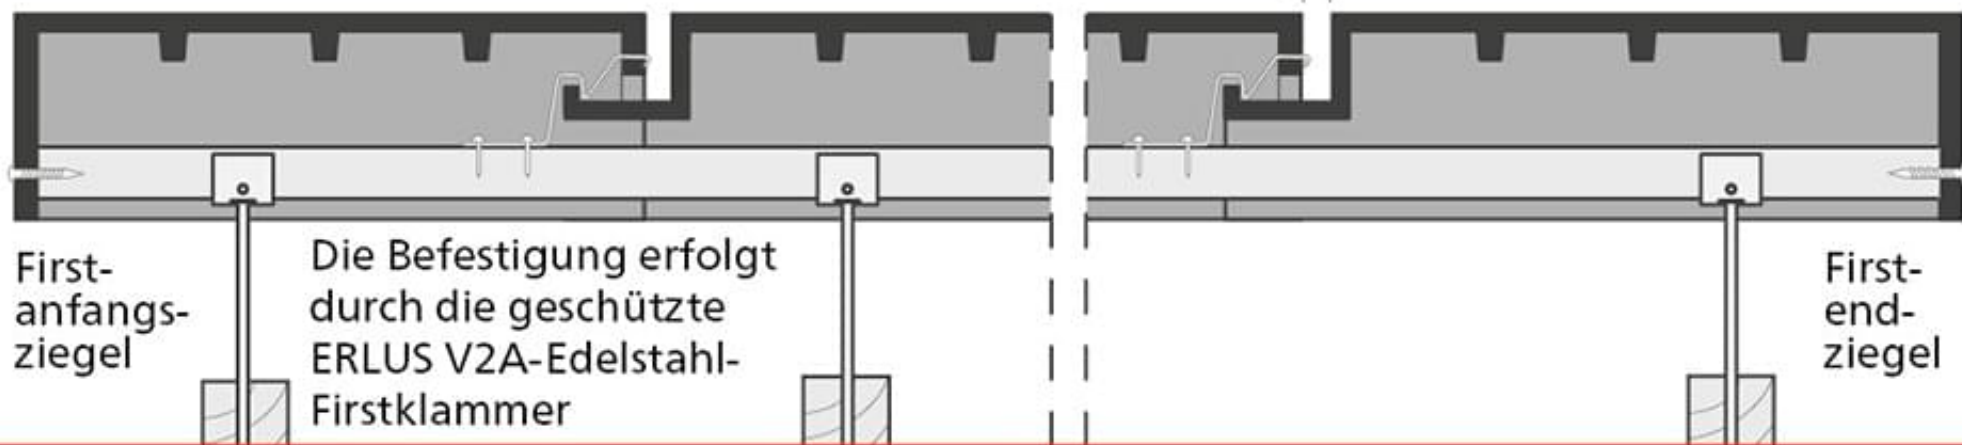


LINKER ORTGANG*

*Die Karat RS Ortgänge werden bei flachen Dachneigungen durch die verstärkten Aufhängenasen geschraubt. Hierbei kann je nach Lattenquerschnitt ein Vorbohren notwendig sein.

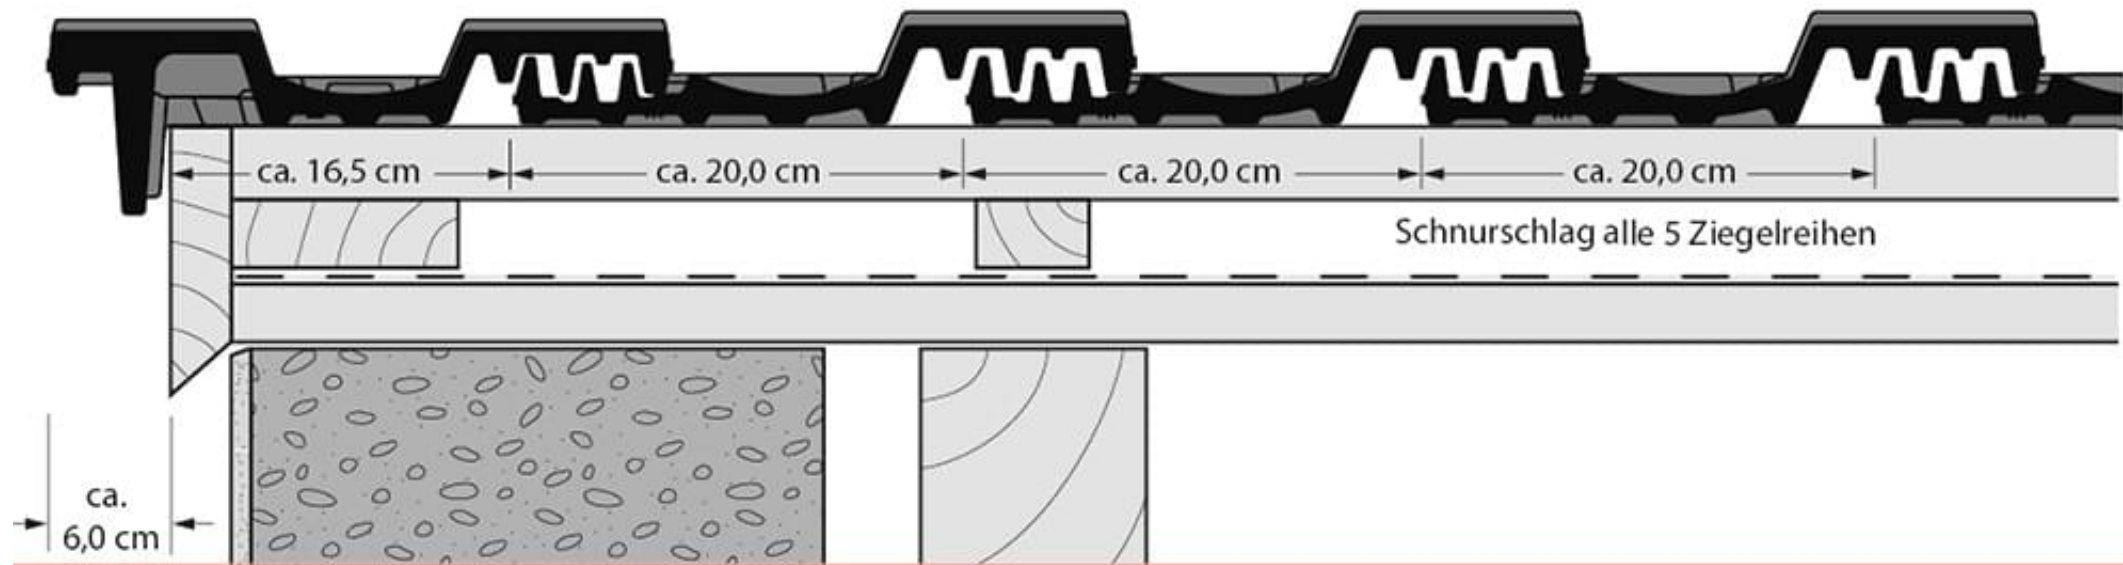


RECHTER ORTGANG*

*Die Karat RS Ortgänge werden bei flachen Dachneigungen durch die verstärkten Aufhängen-nasen geschraubt. Hierbei kann je nach Lattenquerschnitt ein vorbohren notwendig sein.

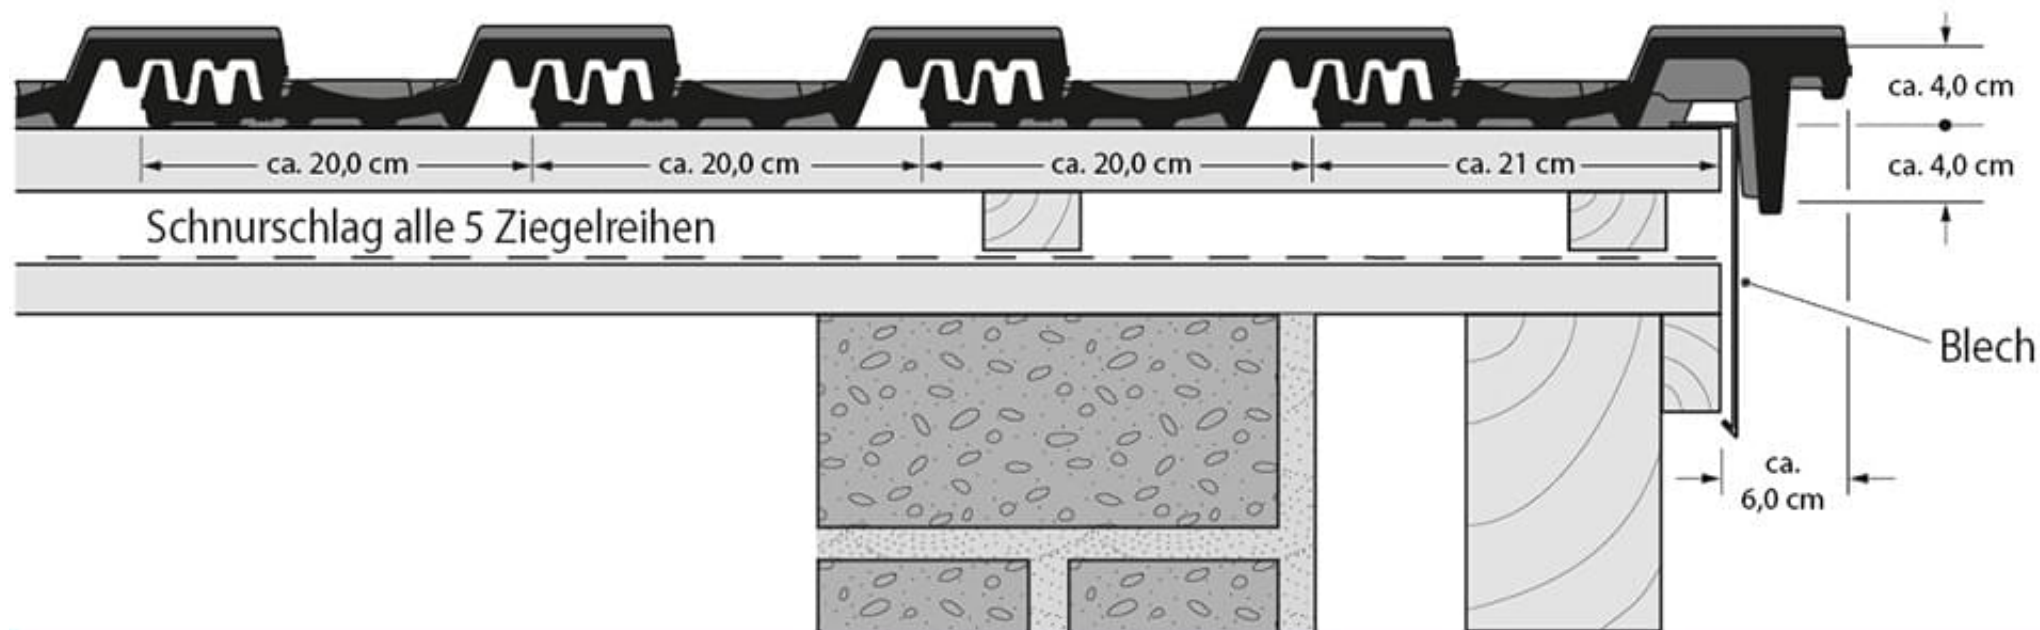

PULTDACH

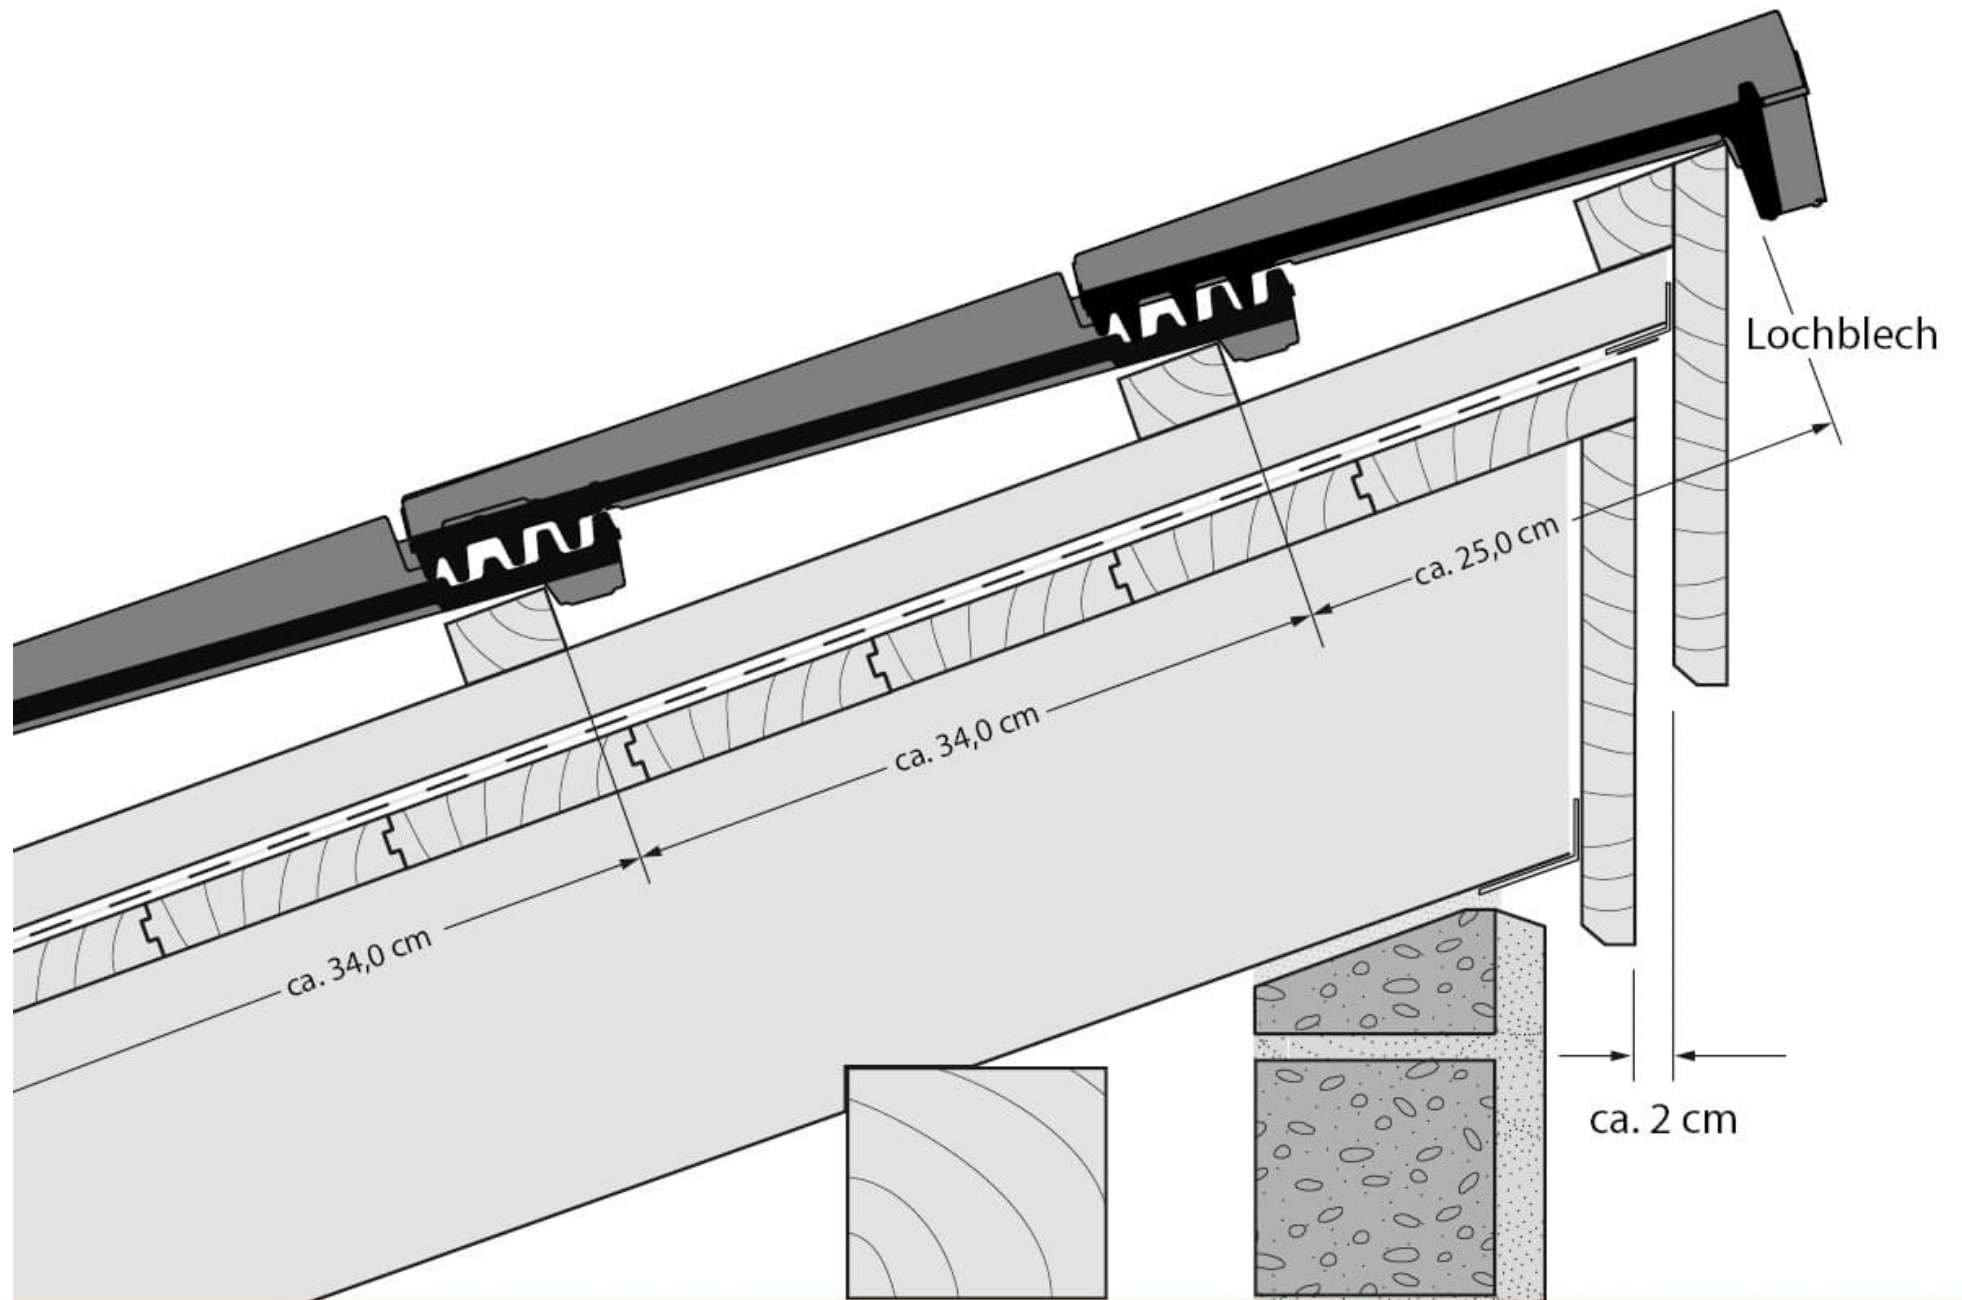

KNAPPE TRAUFEN

ERLUS empfiehlt den Einsatz eines Traufbleches.

