


FIRSTLÜFTERZIEGEL NR. 17 LÜ MIT FIRSTANSCHLUSSZIEGEL, TROCKEN VERLEGT

Die angegebenen Maße sind Planungswerte
und vor der Verlegung zu prüfen.

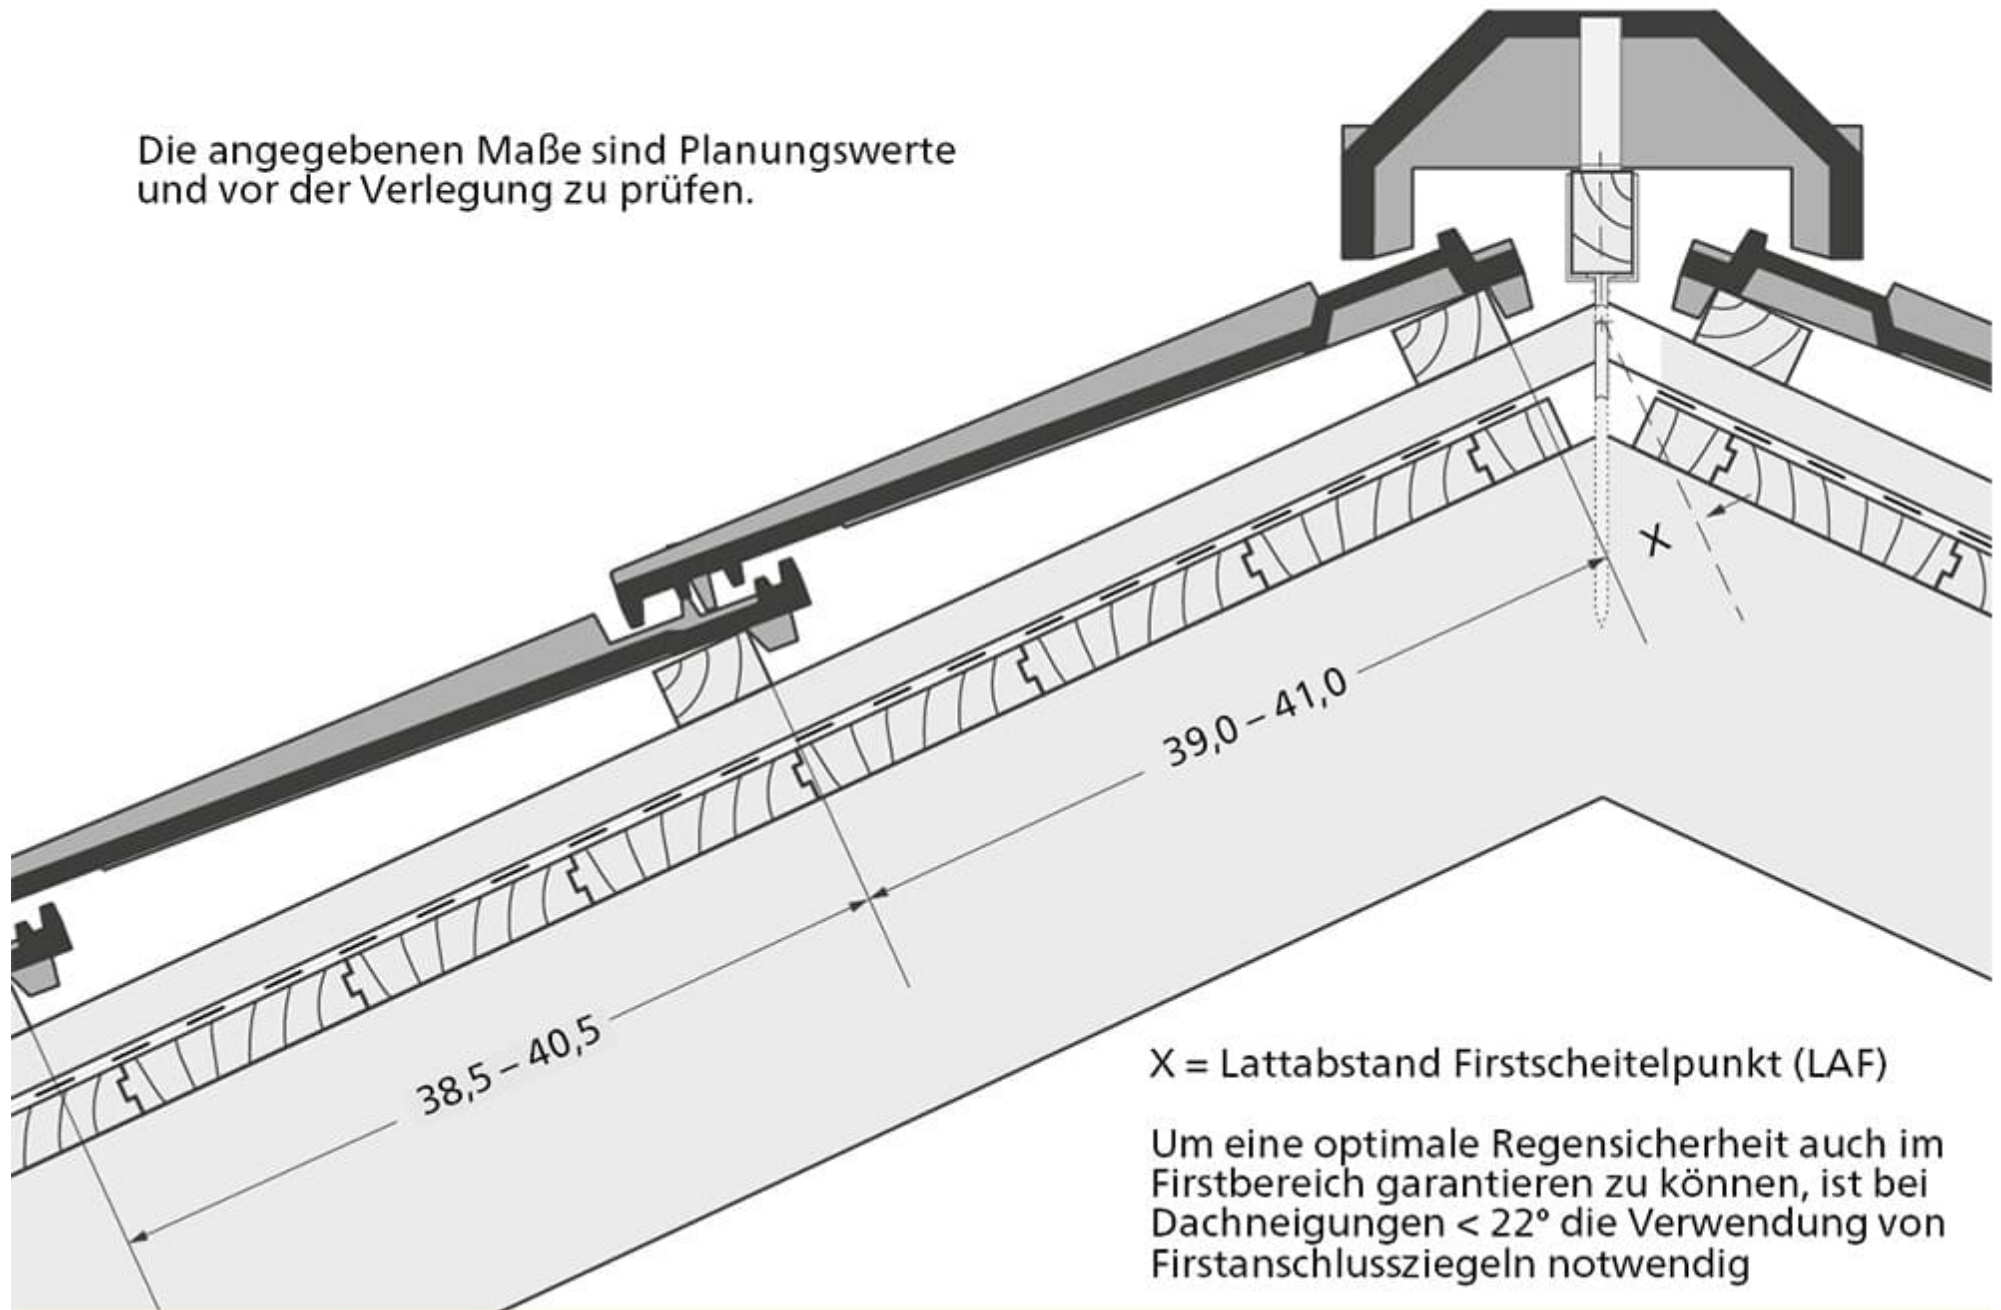

X = Lattabstand Firstscheitelpunkt (LAF)


Um eine optimale Regensicherheit auch im Firstbereich garantieren zu können, ist bei Dachneigungen $< 22^\circ$ die Verwendung von Firstanschlussziegeln notwendig

FIRSTLÜFTERZIEGEL NR. 17 LÜ

Für die funktions- und flugschneesichere Unterdrucklüftung bis 10 m Sparrenlänge
2,5 Stck./lfm.


ca. 3,5 cm
verschiebbar/lfm.

Hauptwetterrichtung

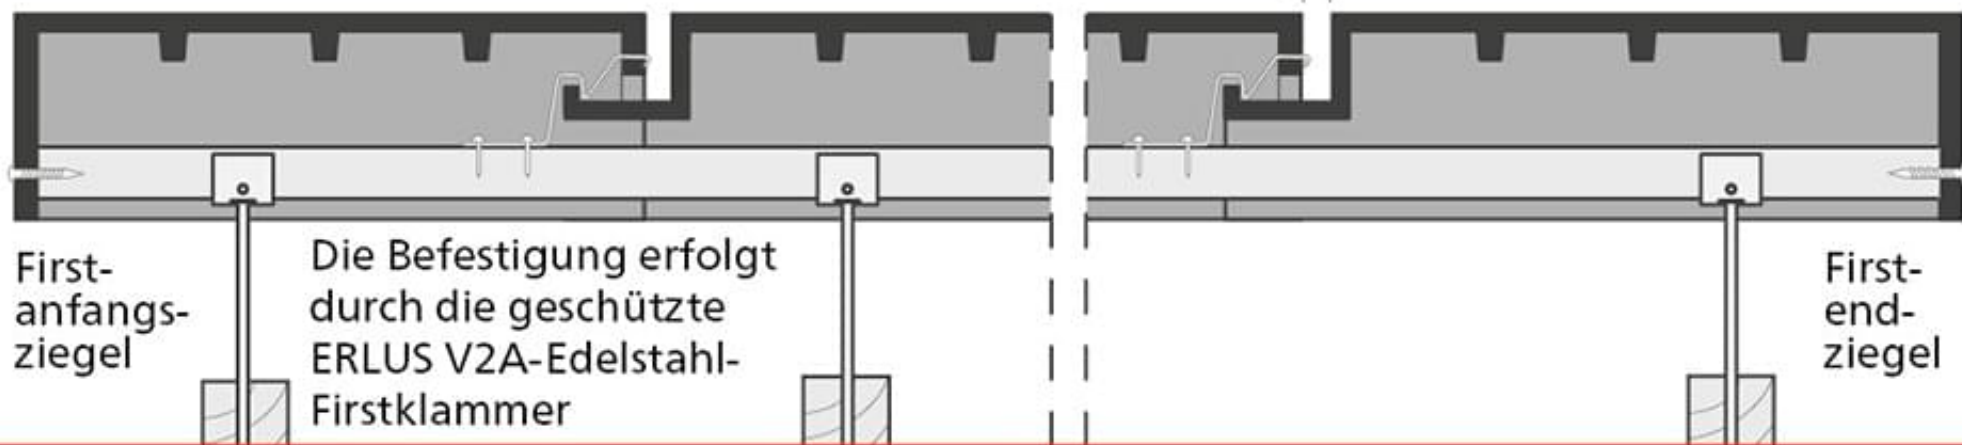


LINKER ORTGANG*

*bei flacher Dachneigung Verschraubungsloch im Ortgang dauerelastisch (z. B. mit Spenglerschrauben) abdichten

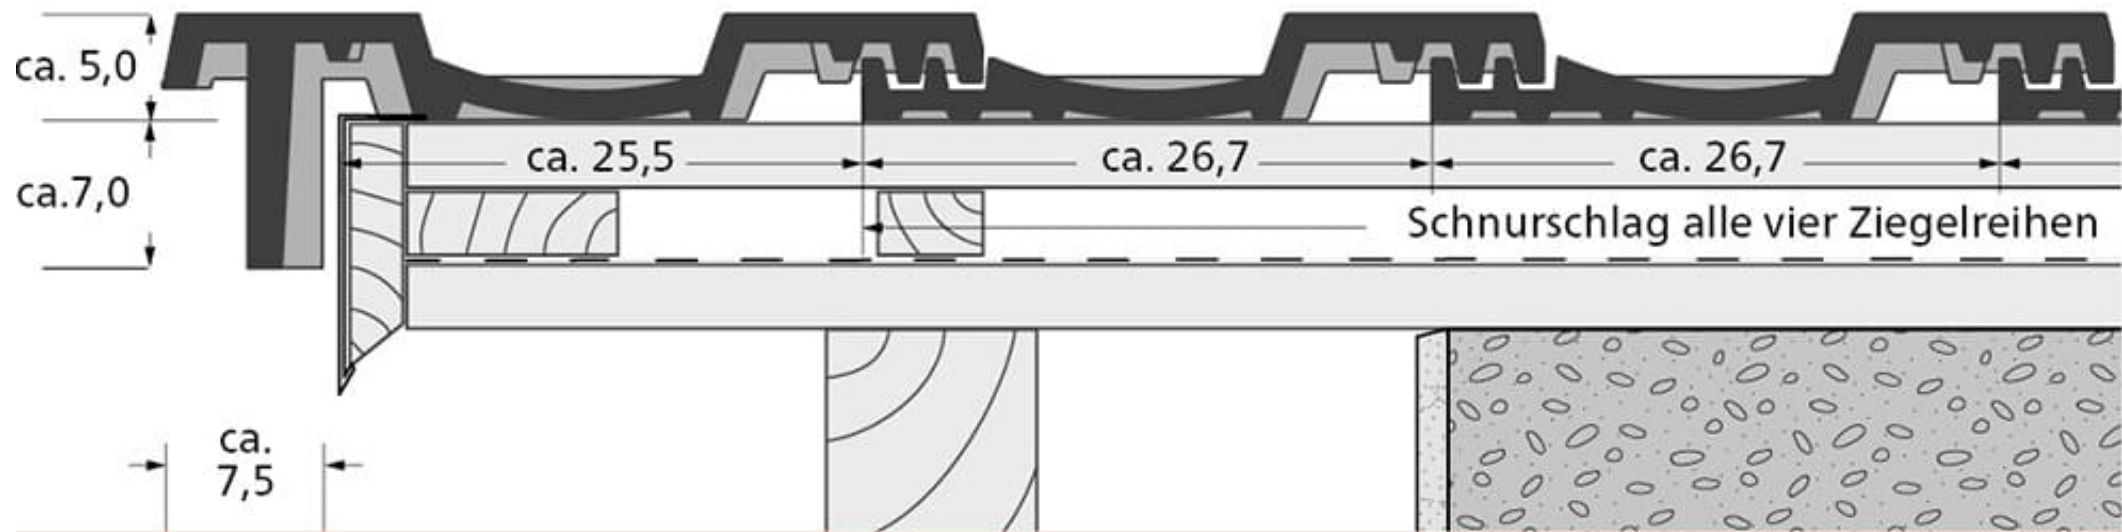


RECHTER ORTGANG*

*bei flacher Dachneigung Verschraubungsloch im Ortgang dauerelastisch (z. B. mit Spenglerschrauben) abdichten

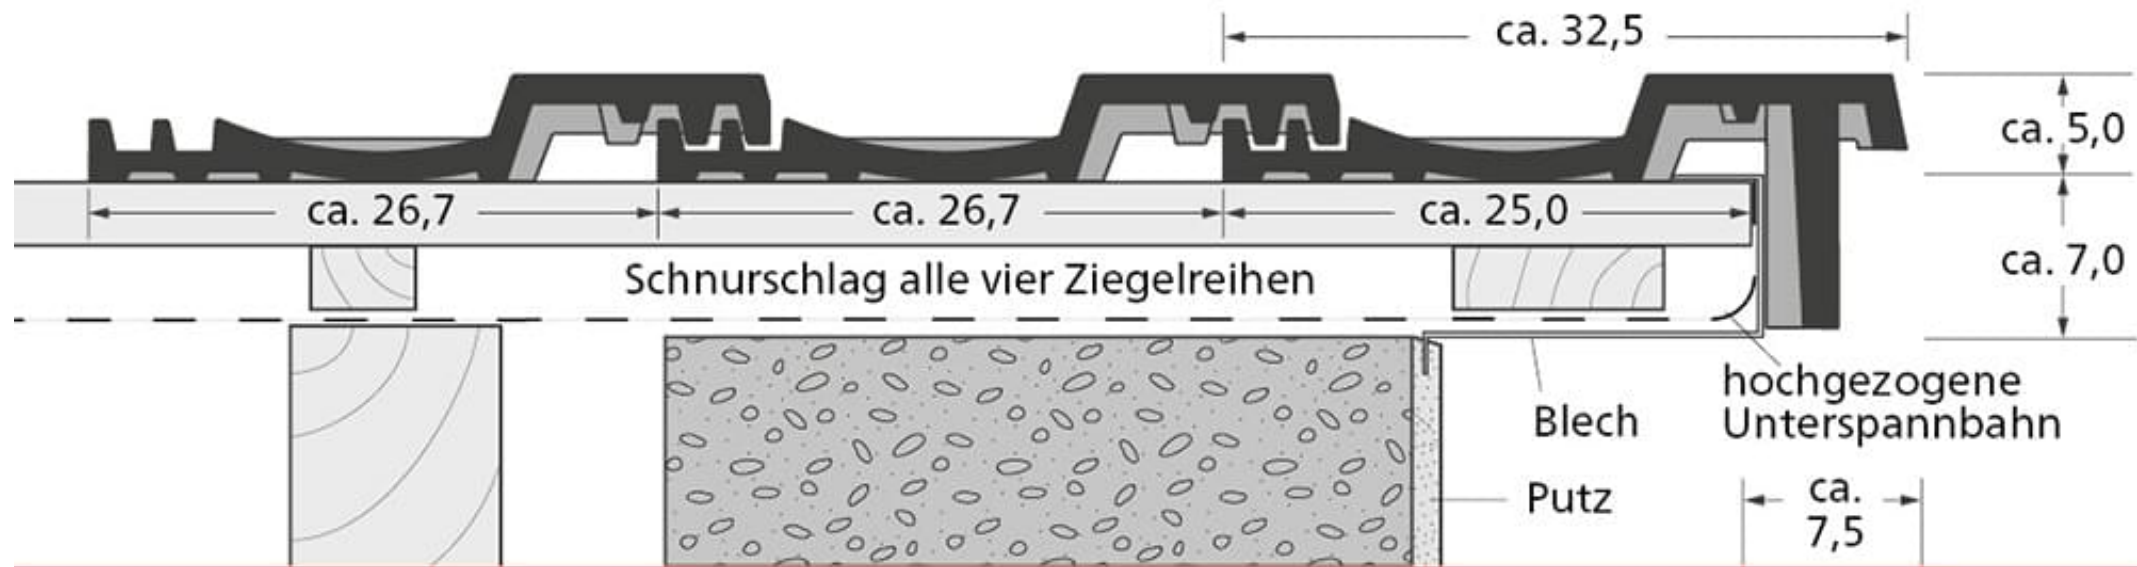


ÜBERSTEHENDE TRAUFE MIT AUFSPARRENDÄMMUNG

ERLUS empfiehlt den Einsatz eines Traufbleches.

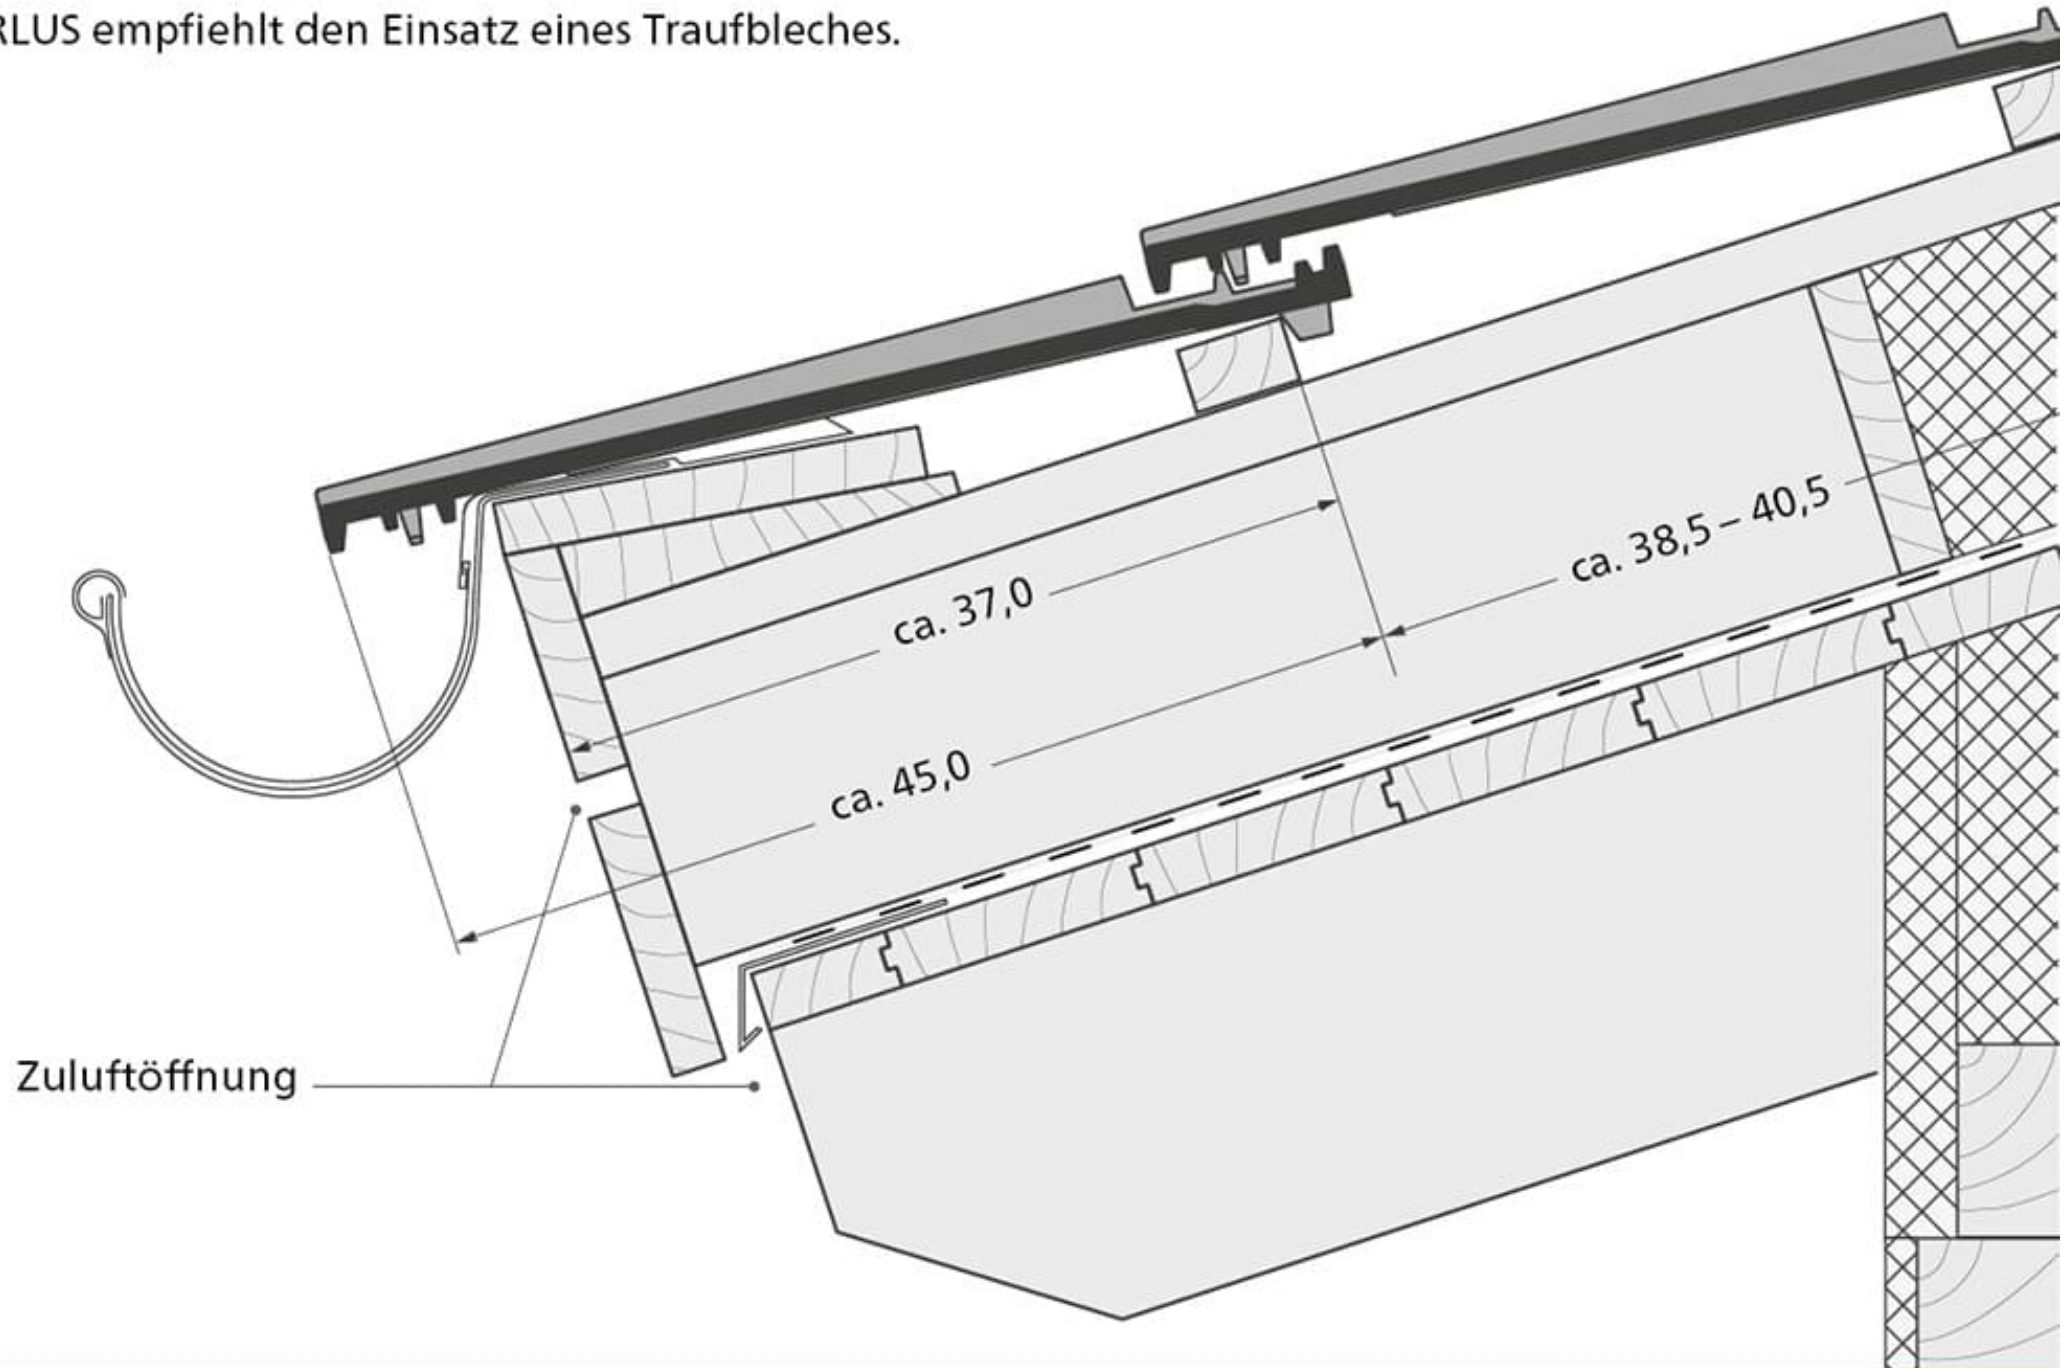


TRAUFE MIT UMLAUFENDEN BRETTABSCHLUSS

ERLUS empfiehlt den Einsatz eines Traufbleches.

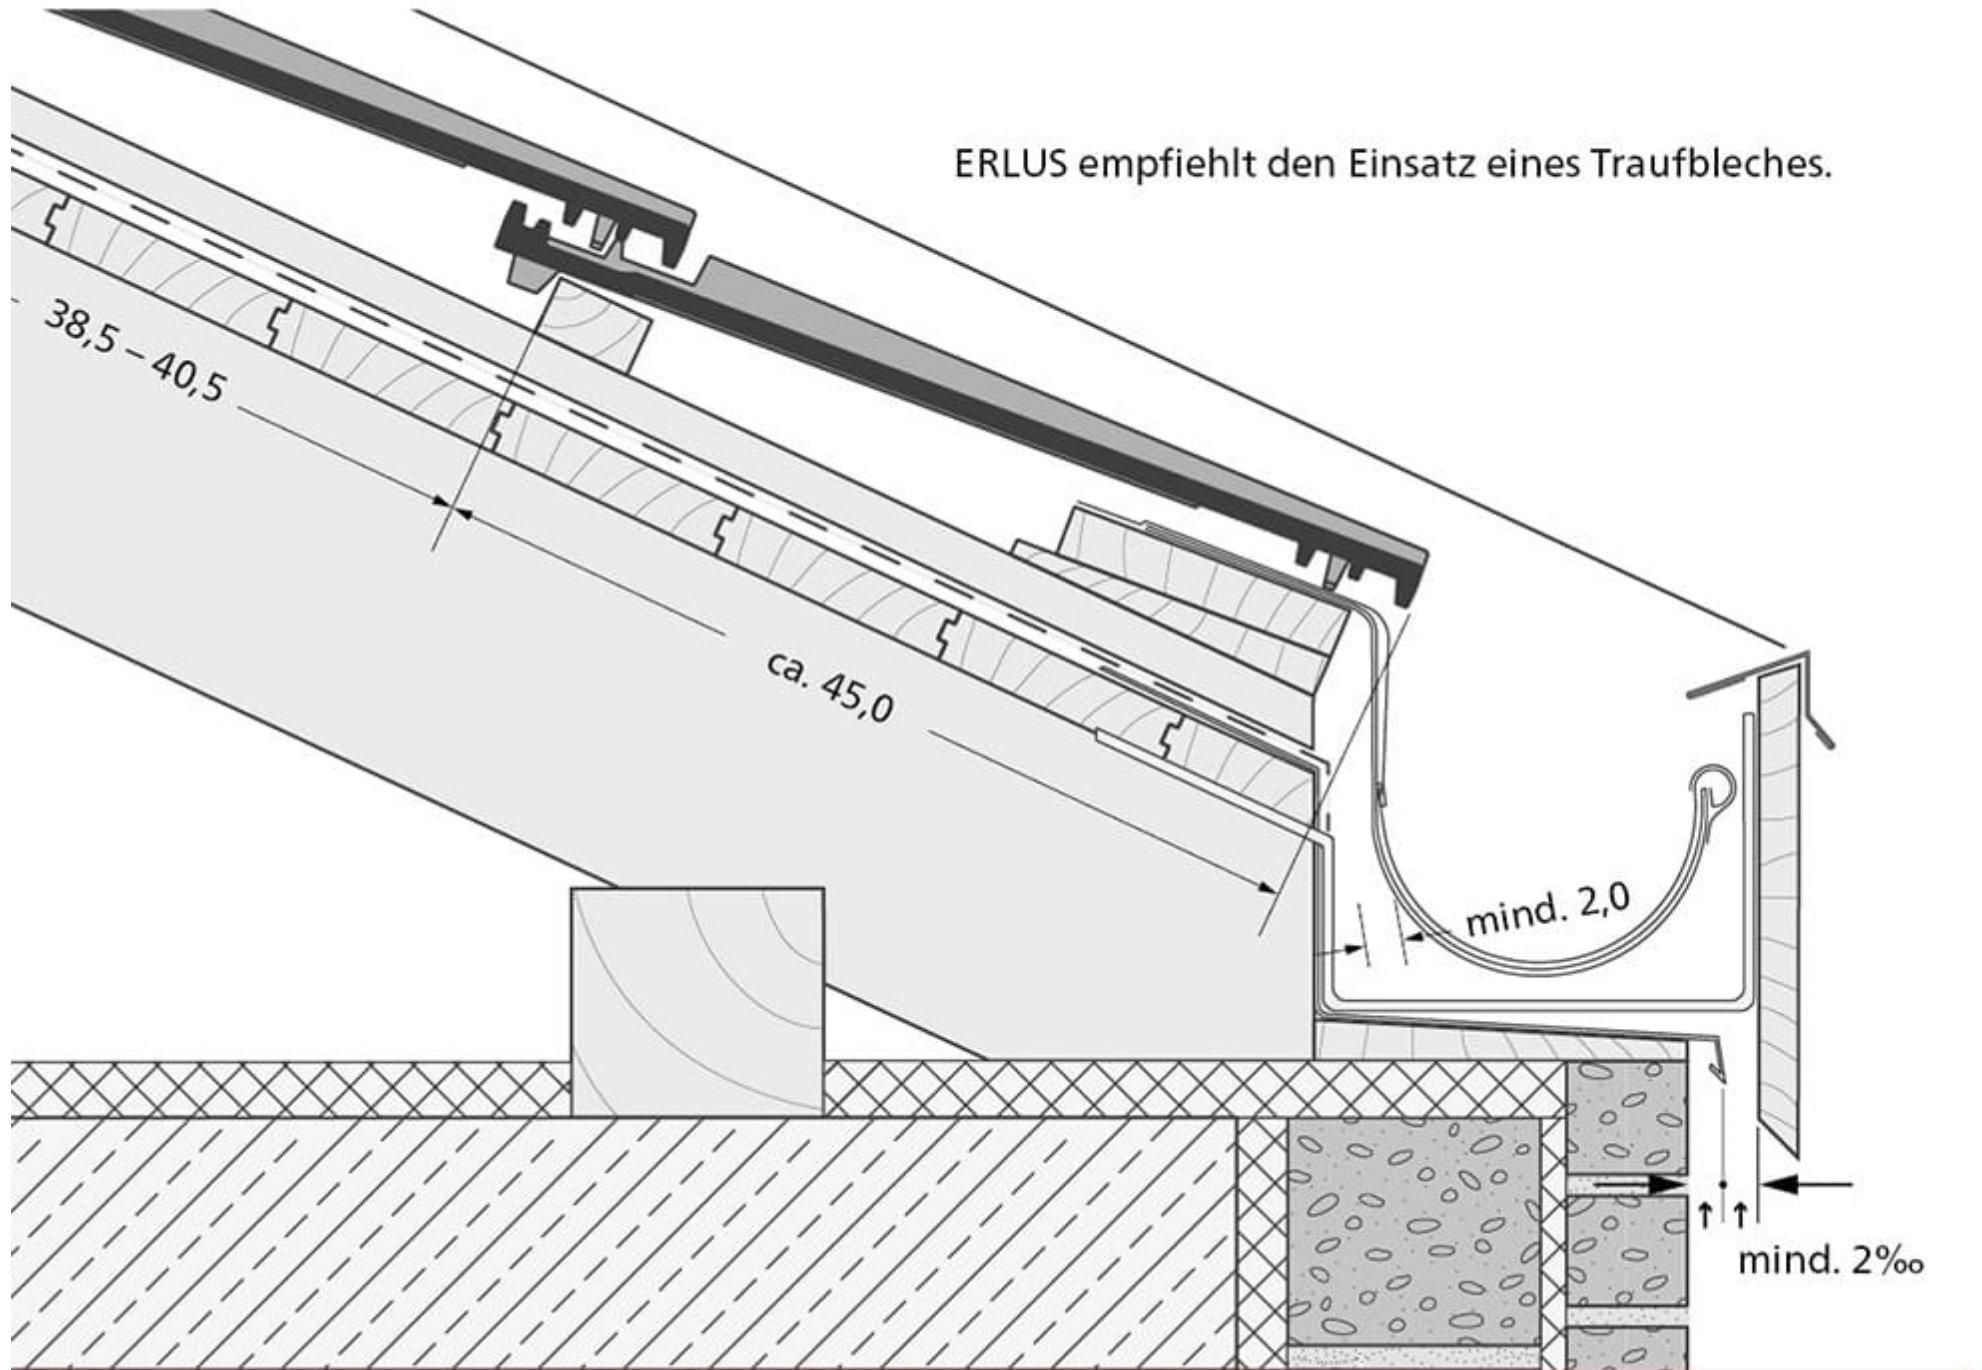

ERLUS Dachbegehungssystem

LATTWEITE > 37,5 cm

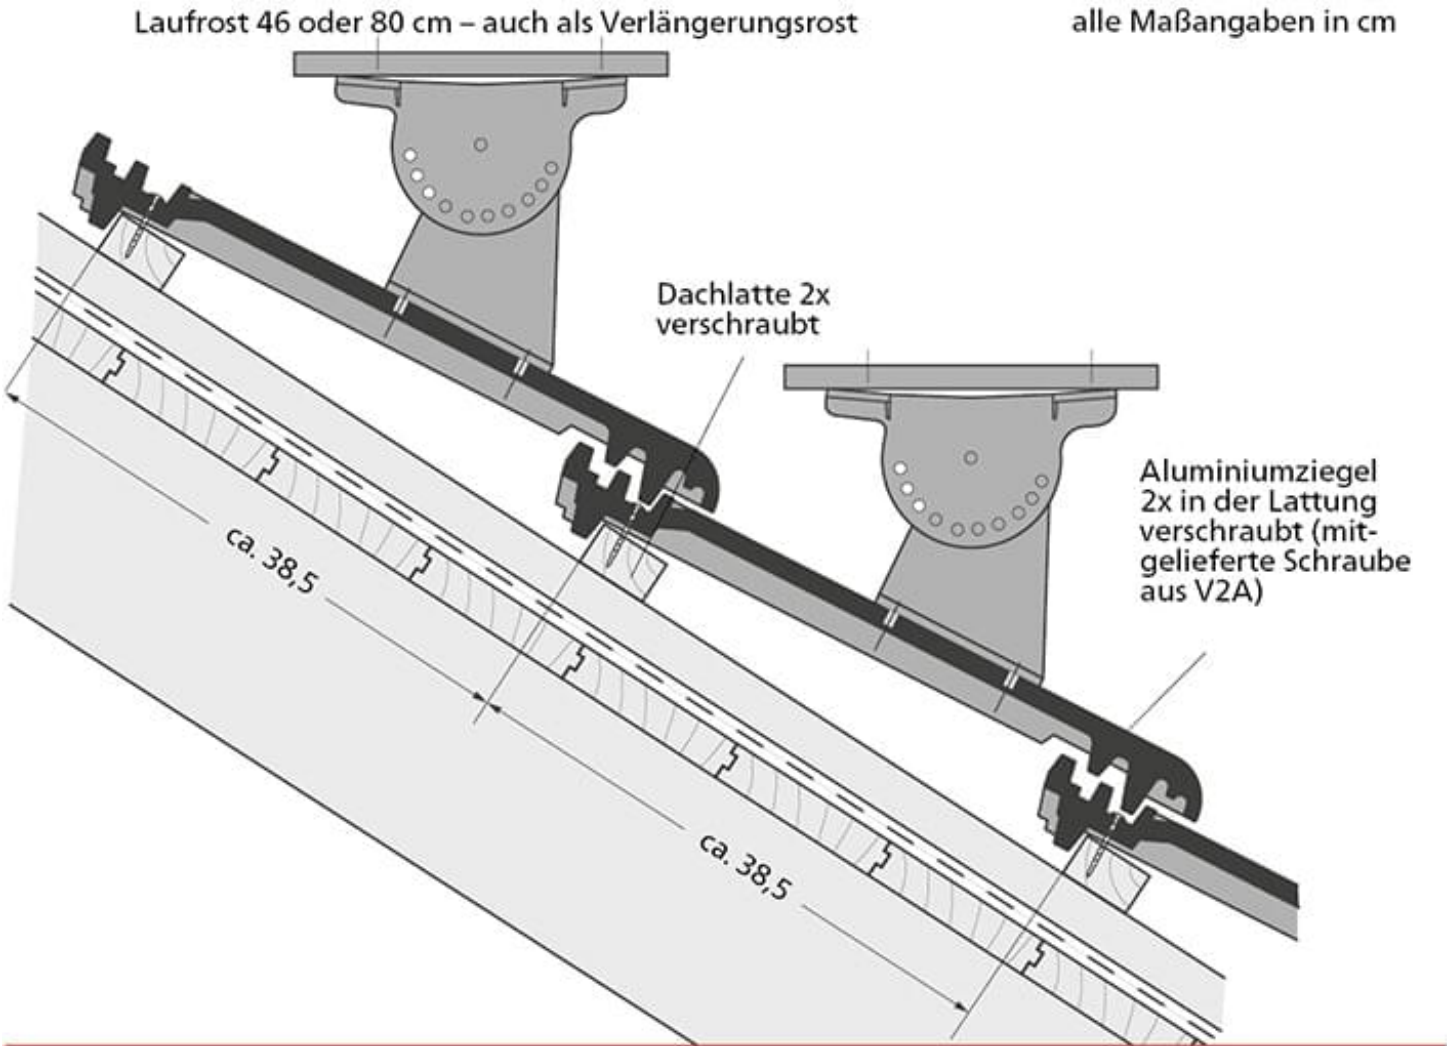

VERARBEITUNG VON TRITTFLÄCHEN UND ROSTEN NACH DIN 18160-5

Zeichnung: Linea

ARTIKEL	≤ 45°	≥ 45°
Trittflächen (Roste 46 cm)	jede Ziegelreihe	jede Ziegelreihe
Einzeltritt (Steigtritt)	jede Ziegelreihe	jede Ziegelreihe

aus nicht rostendem Stahl/Alu, geprüft nach DIN EN 516,
keine Stützlaten erforderlich