



FIRSTLÜFTERZIEGEL NR. 19 LÜ MIT FIRSTANSCHLUSSZIEGELN

(vollkeramische Lüftung bis 10 m Sparrenlänge)

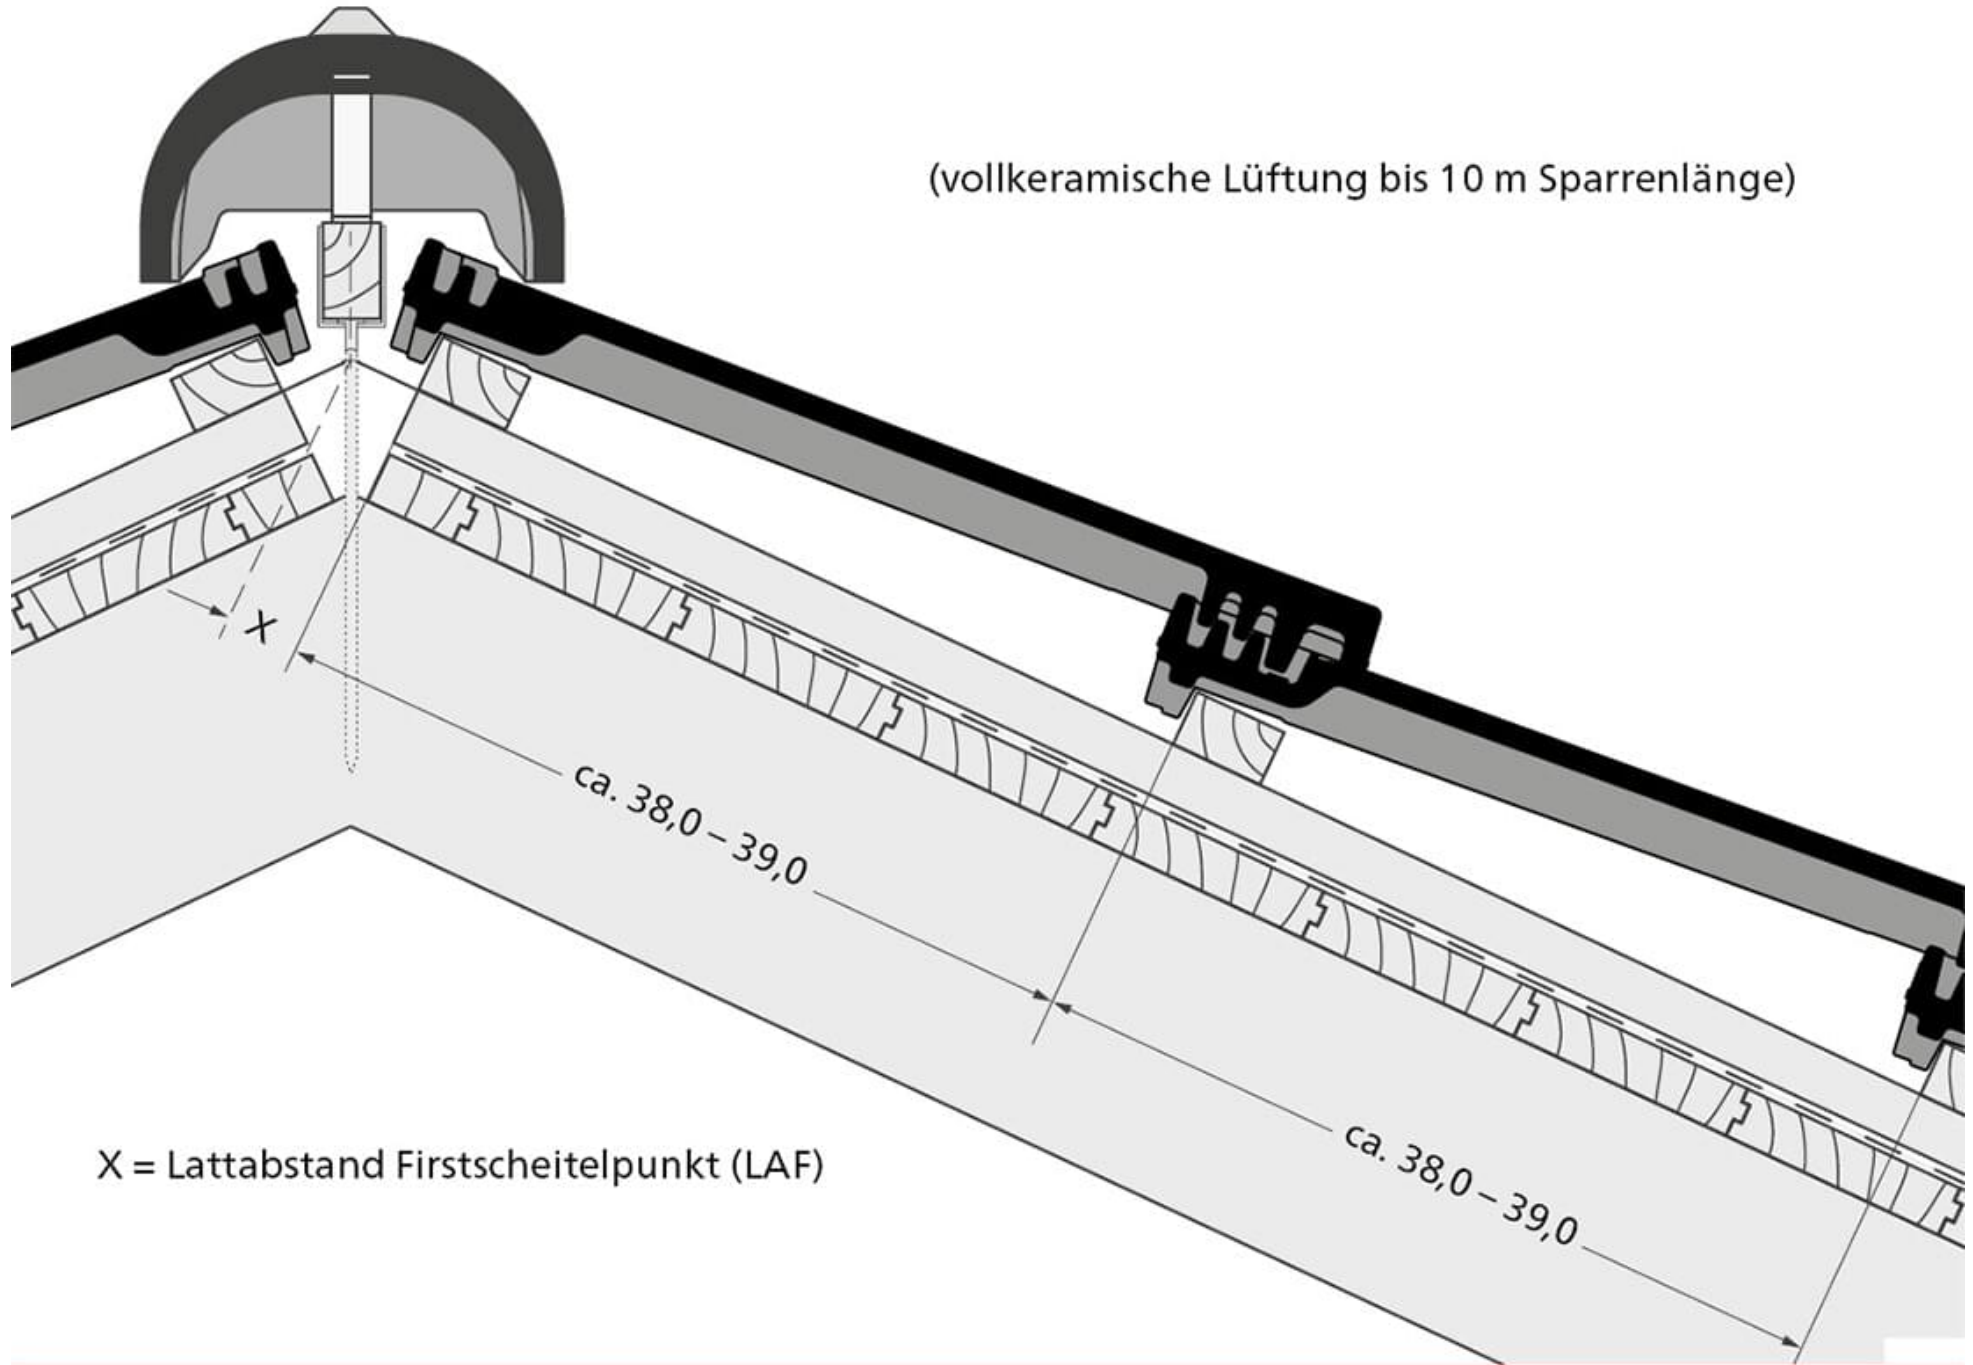

ERLUS Dachbegehungssystem

LATTWEITE > 37,5 cm

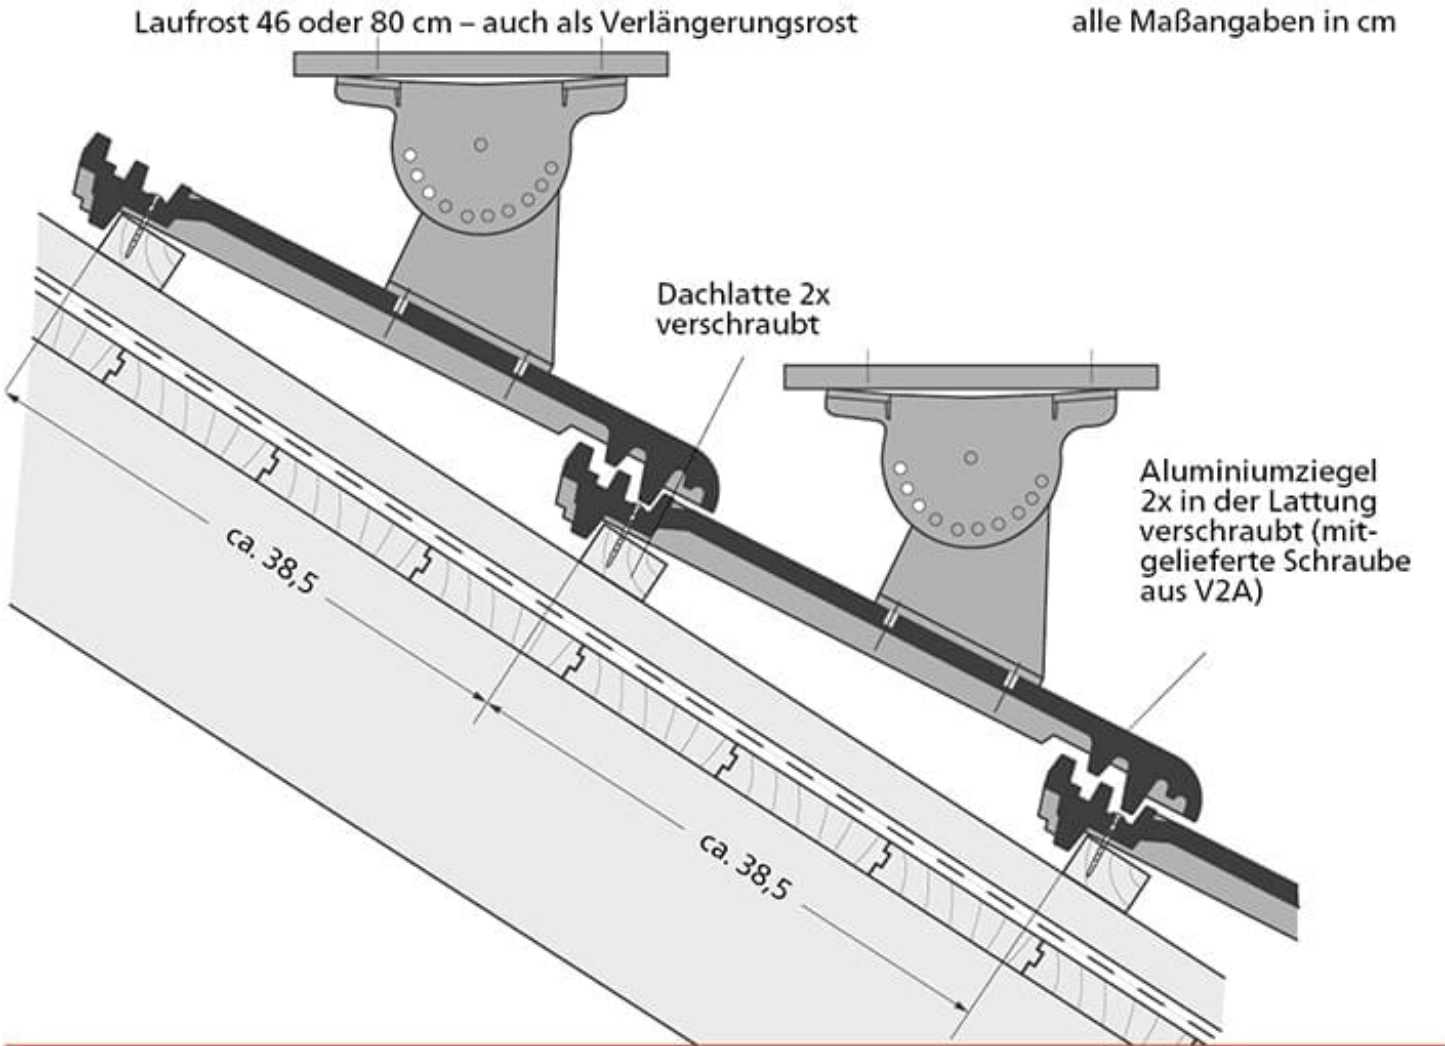

VERARBEITUNG VON TRITTFLÄCHEN UND ROSTEN NACH DIN 18160-5


Zeichnung: Linea

ARTIKEL	≤ 45°	≥ 45°
Trittflächen (Roste 46 cm)	jede Ziegelreihe	jede Ziegelreihe
Einzeltritt (Steigtritt)	jede Ziegelreihe	jede Ziegelreihe

aus nicht rostendem Stahl/Alu, geprüft nach DIN EN 516,
keine Stützlaten erforderlich


LINKER ORTGANG*

- * Um die Ortgänge auch bei flachen Dachneigungen regensicher fixieren zu können, werden die Level RS® Ortgänge durch die verstärkten kopfseitigen Aufhängenasen geschraubt. Hierbei kann je nach Holzquerschnitt ein Vorbohren der Latten notwendig werden.

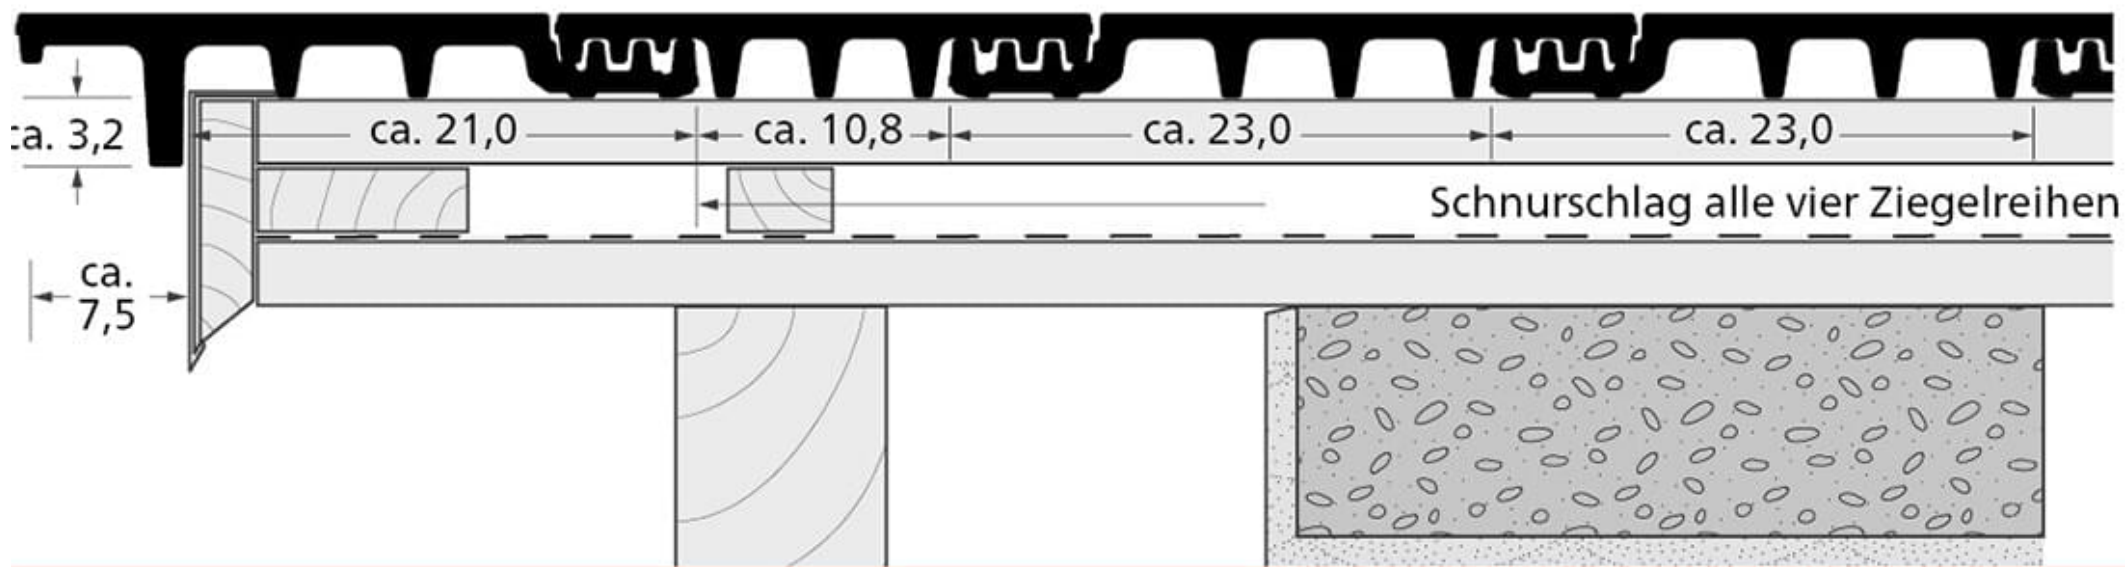


HALBER LINKER ORTGANG*

mit Doppelwulst

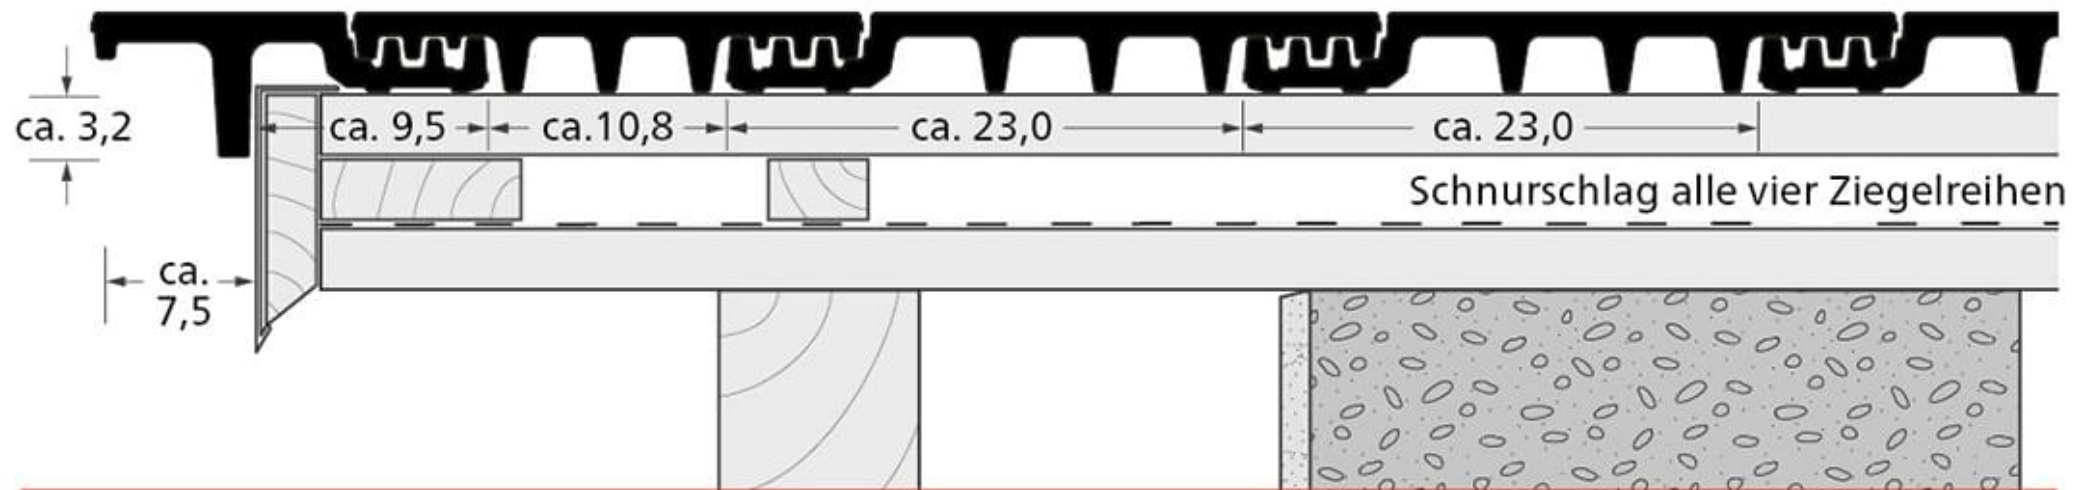


HALBER RECHTER ORTGANG*

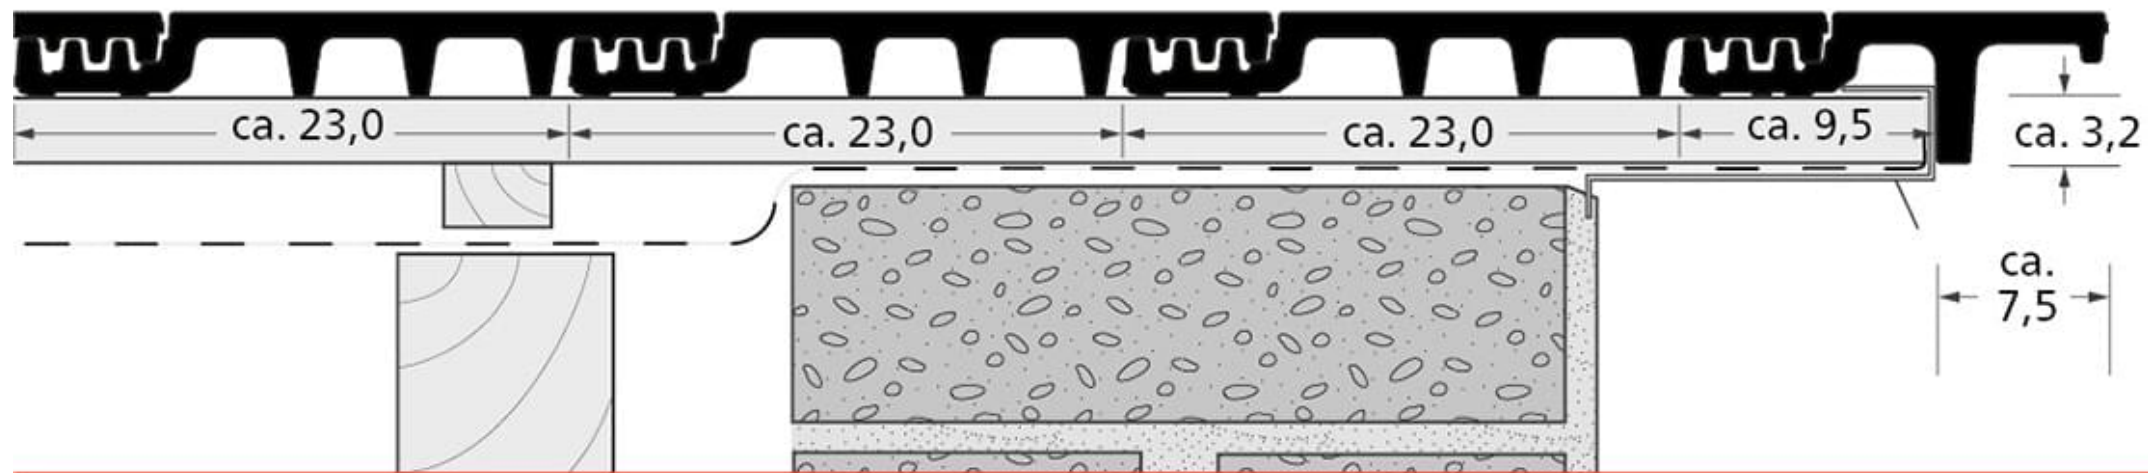

ÜBERSTEHENDE TRAUFE MIT AUFSPARRENDÄMMUNG

ERLUS empfiehlt den Einsatz eines Traufbleches.

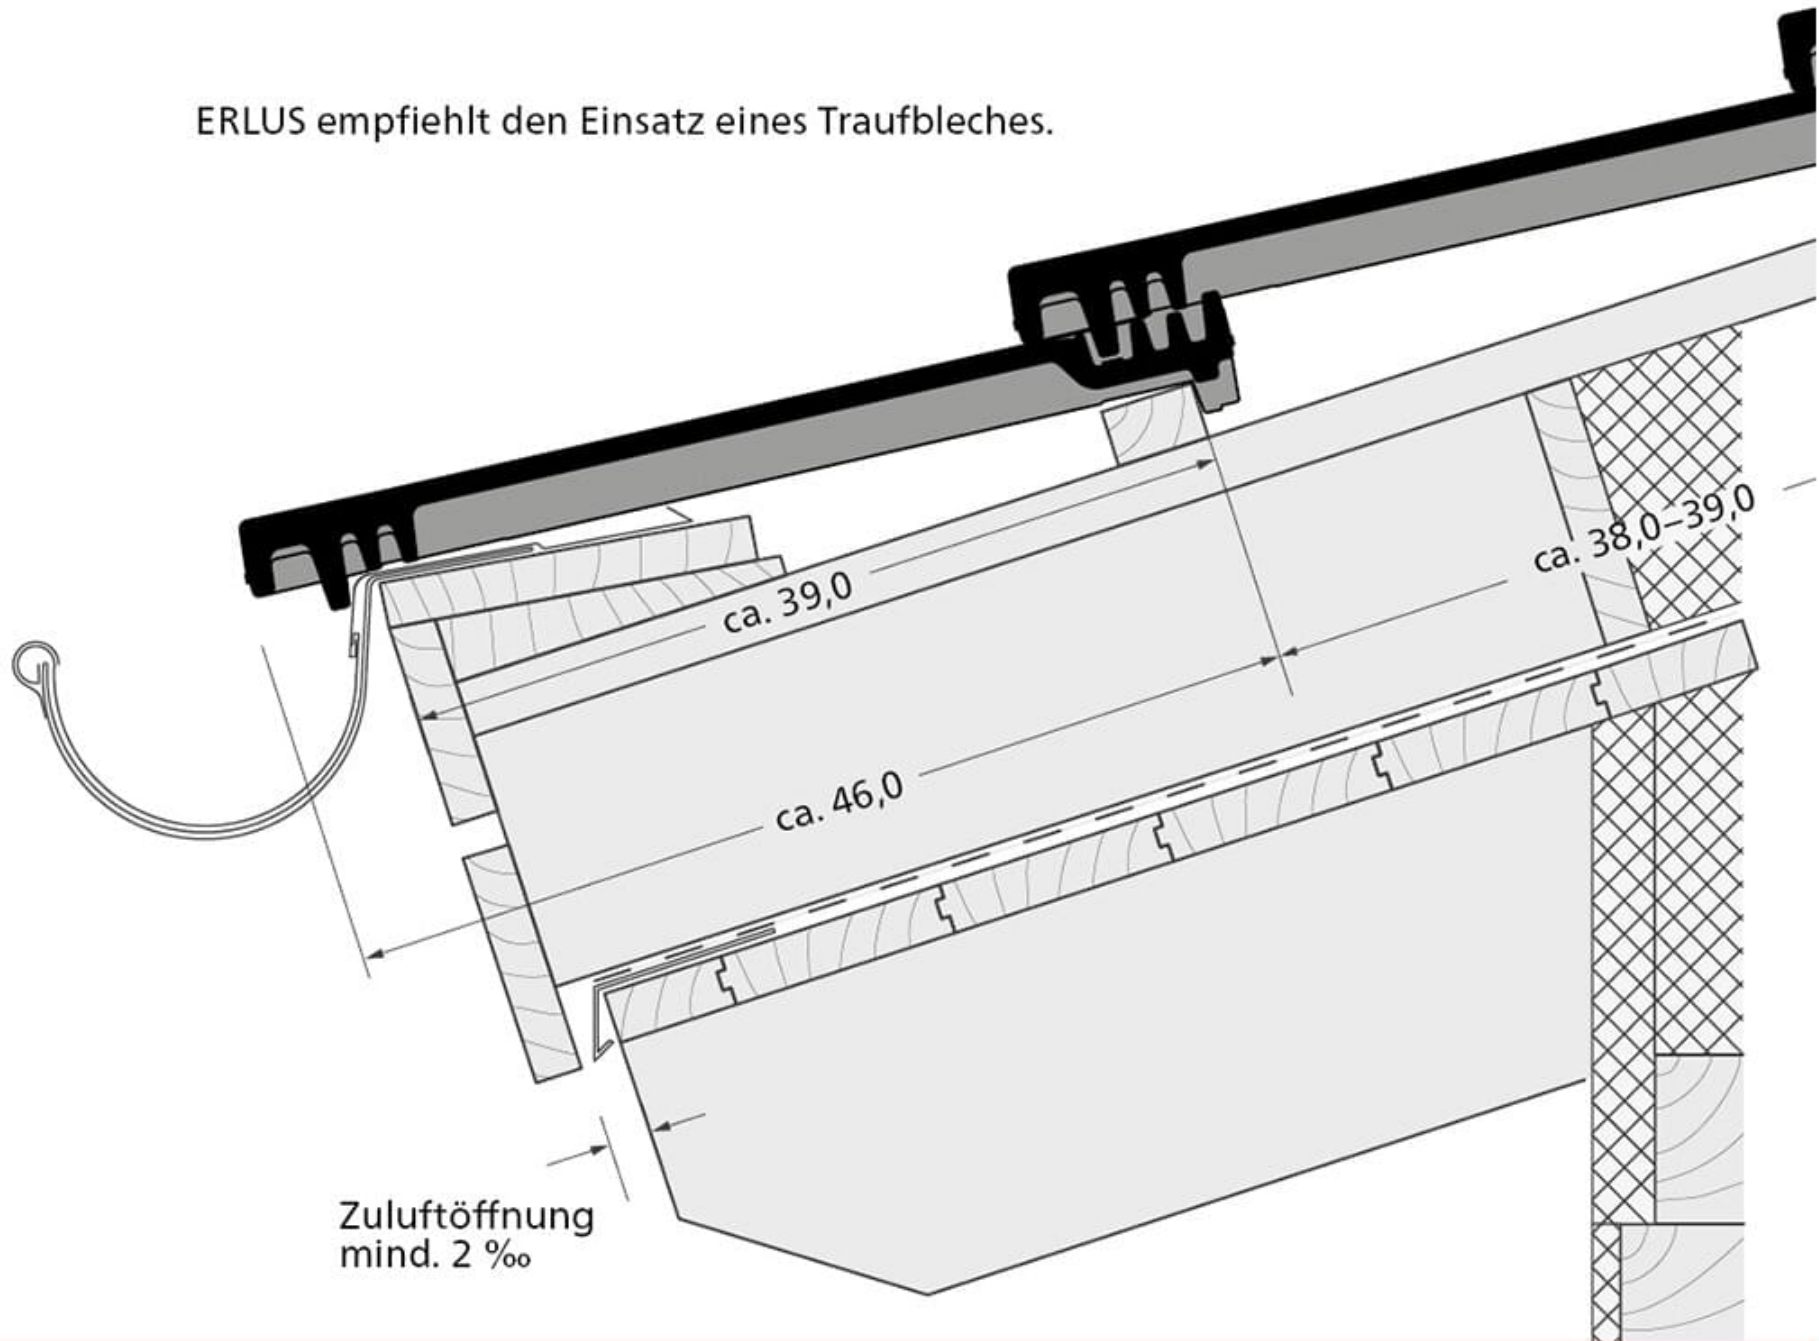

PULTDACH

