


FIRSTLÜFTERZIEGEL NR. 19 LÜ MIT FIRSTANSCHLUSSZIEGEL

Die angegebenen Maße sind Planungswerte
und vor der Verlegung zu prüfen.


(vollkeramische Lüftung bis 10 m Sparrenlänge)

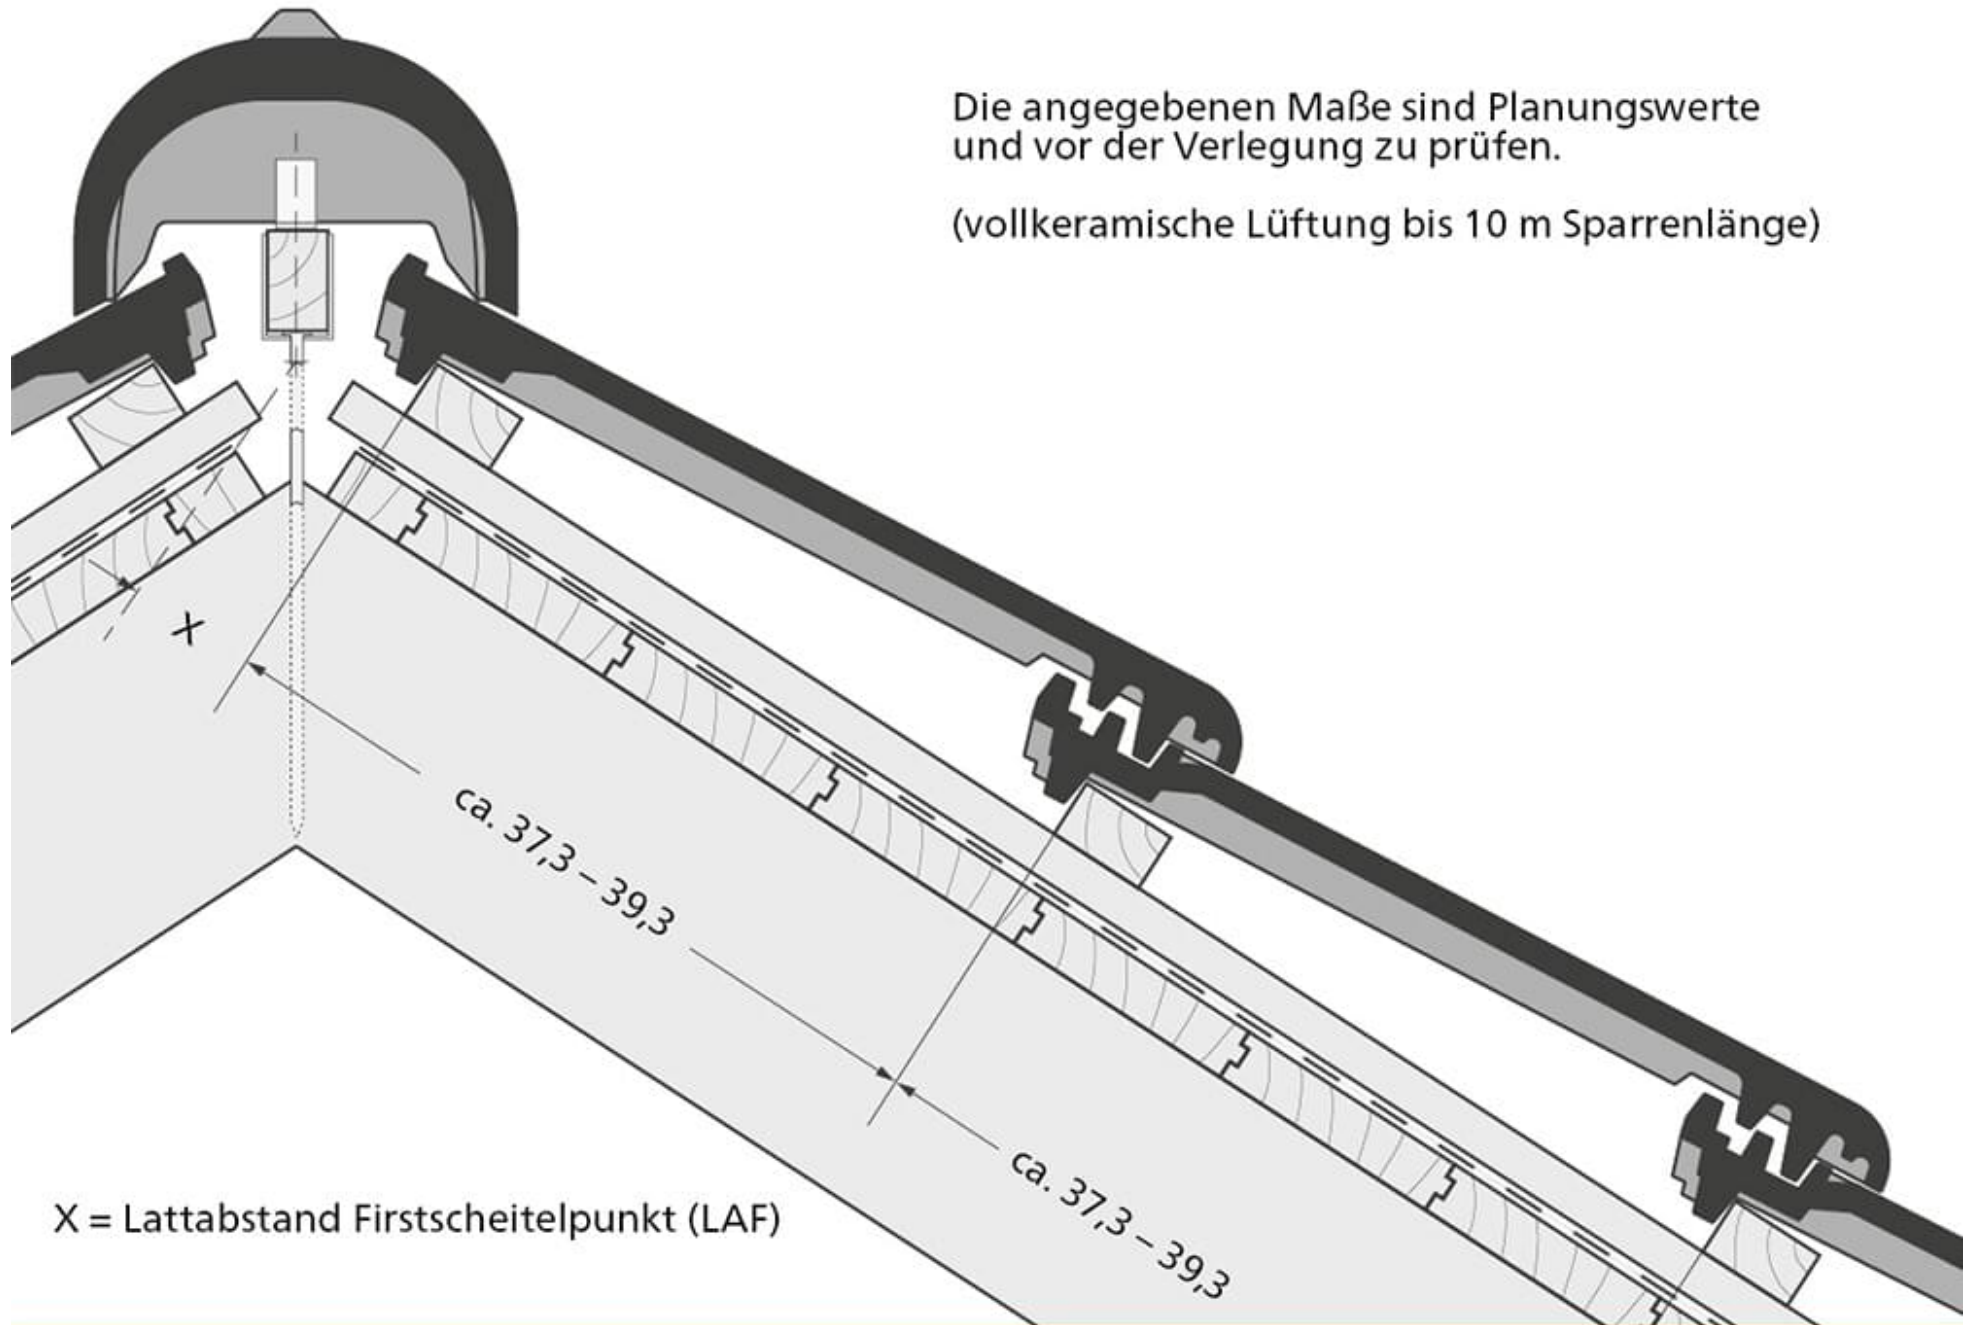

X = Lattabstand Firstscheitelpunkt (LAF)

ERLUS Dachbegehungssystem

LATTWEITE > 37,5 cm

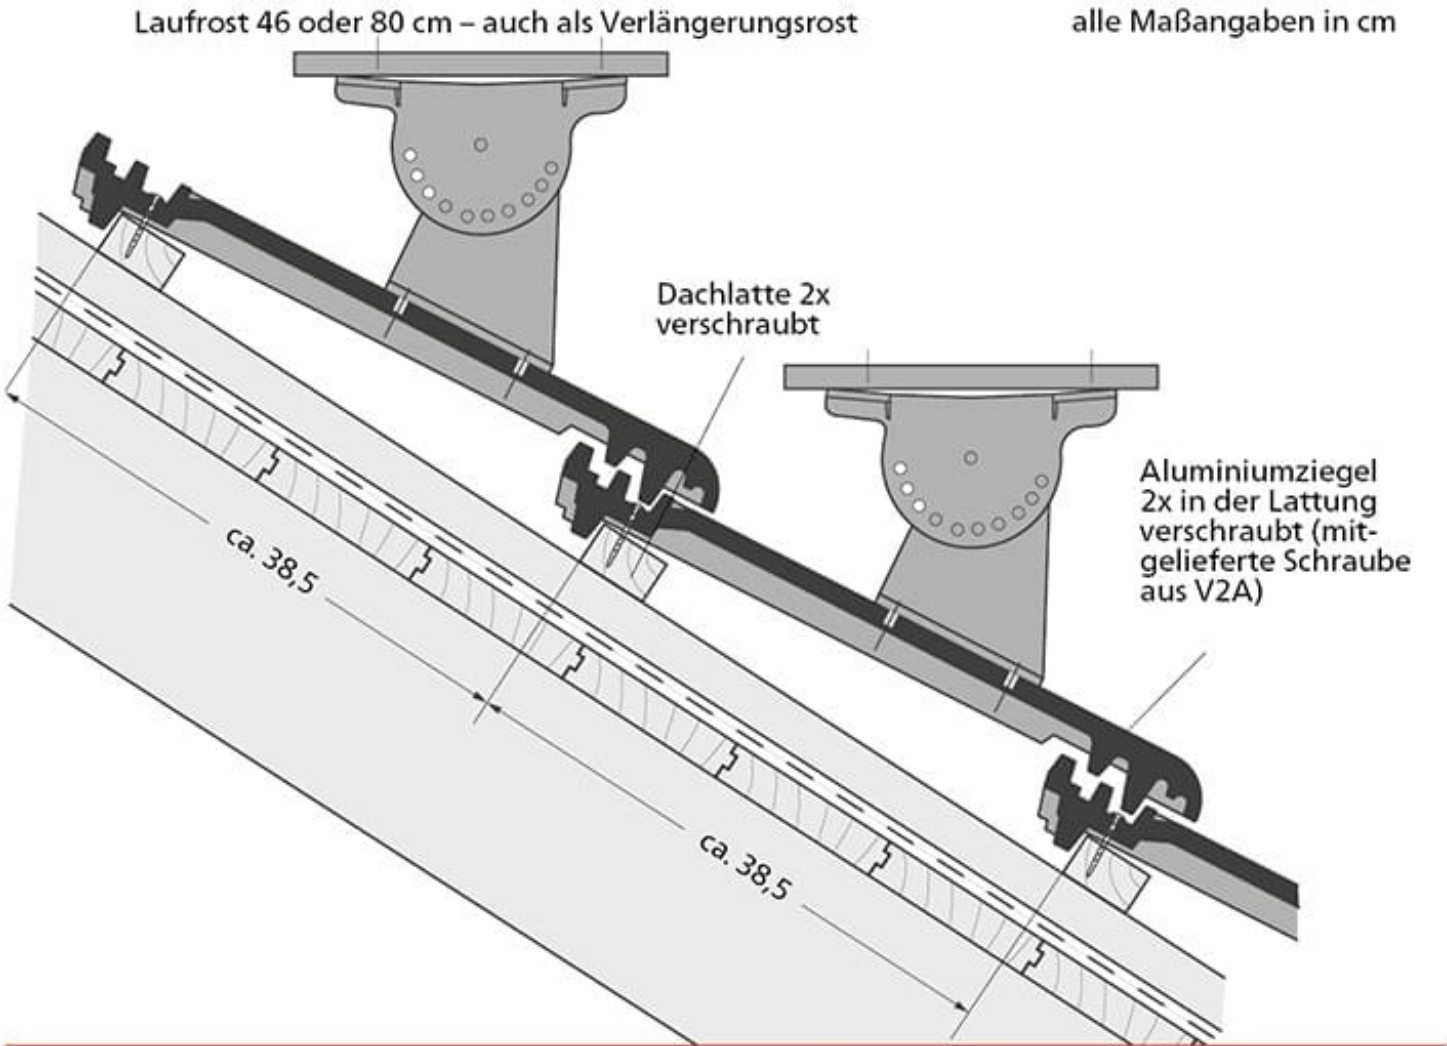

VERARBEITUNG VON TRITTFLÄCHEN UND ROSTEN NACH DIN 18160-5


Zeichnung: Linea

ARTIKEL	≤ 45°	≥ 45°
Trittflächen (Roste 46 cm)	jede Ziegelreihe	jede Ziegelreihe
Einzeltritt (Steigtritt)	jede Ziegelreihe	jede Ziegelreihe

aus nicht rostendem Stahl/Alu, geprüft nach DIN EN 516,
keine Stützplatten erforderlich


LINKER ORTGANG*

*bei flacher Dachneigung Verschraubungsloch im Ortgang dauerelastisch
(z. B. mit Spenglerschrauben) abdichten

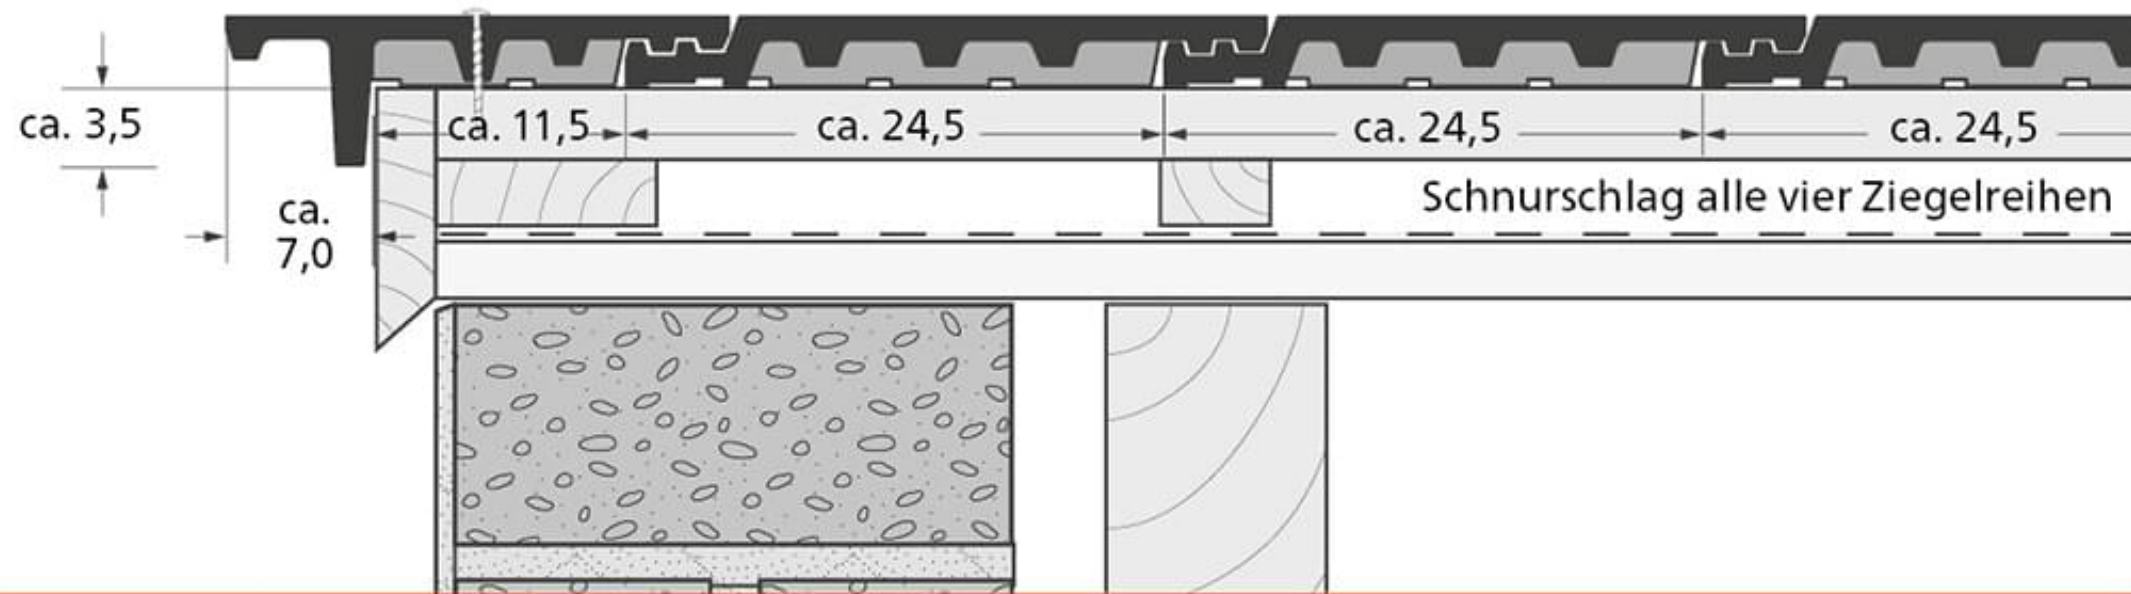

RECHTER ORTGANG*


*bei flacher Dachneigung Verschraubungsloch im Ortgang dauerelastisch
(z. B. mit Spenglerschrauben) abdichten

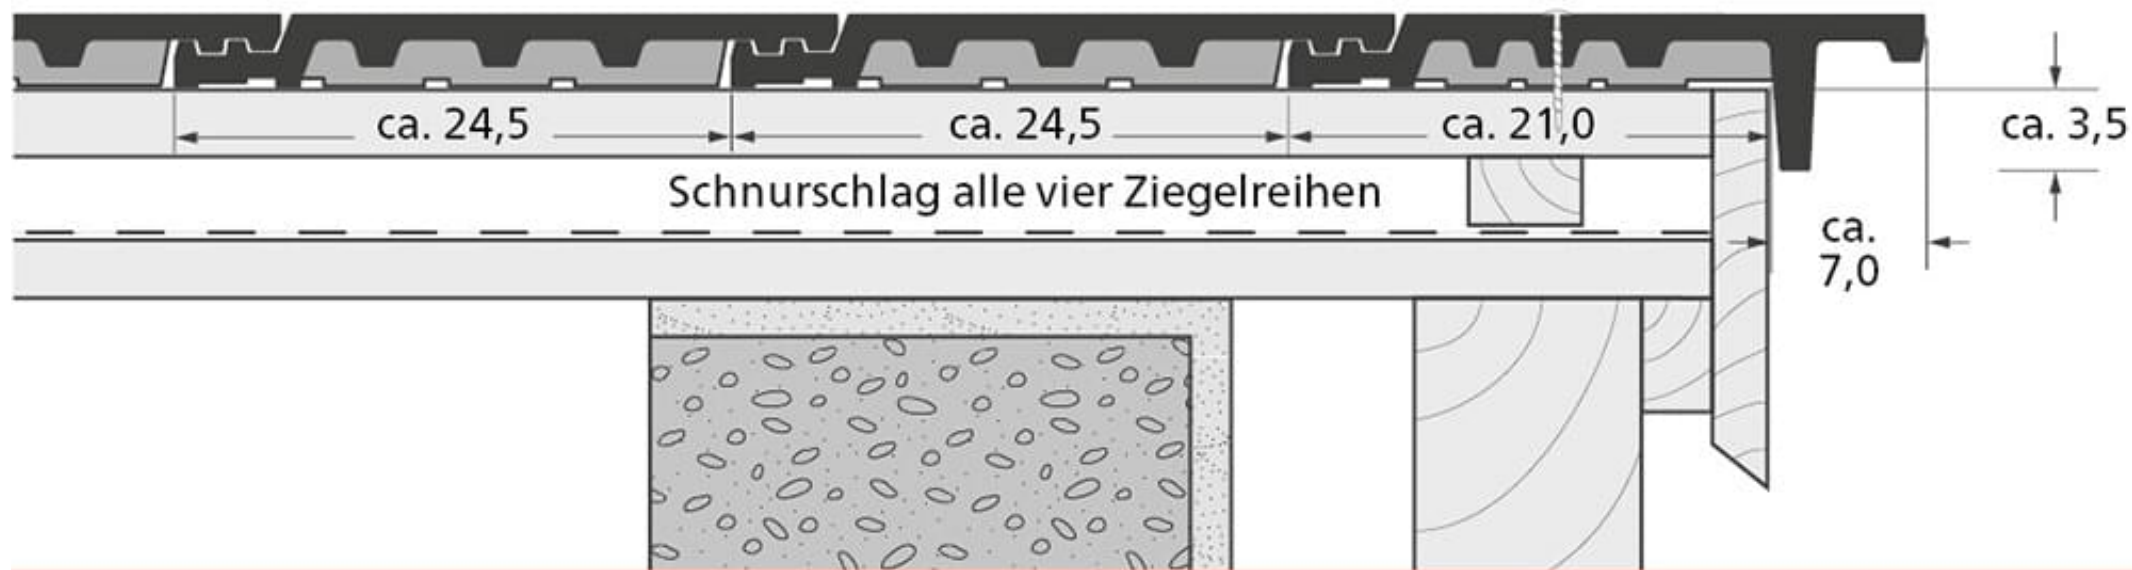

HALBER LINKER ORTGANG*


mit Doppelwulst

* Um die halben Ortgänge auch bei flachen Dachneigungen regensicher fixieren zu können, werden die Level RS® Ortgänge durch die verstärkten kopfseitigen Aufhängenasen geschraubt. Hierbei kann je nach Holzquerschnitt ein Vorbohren der Latten notwendig werden.

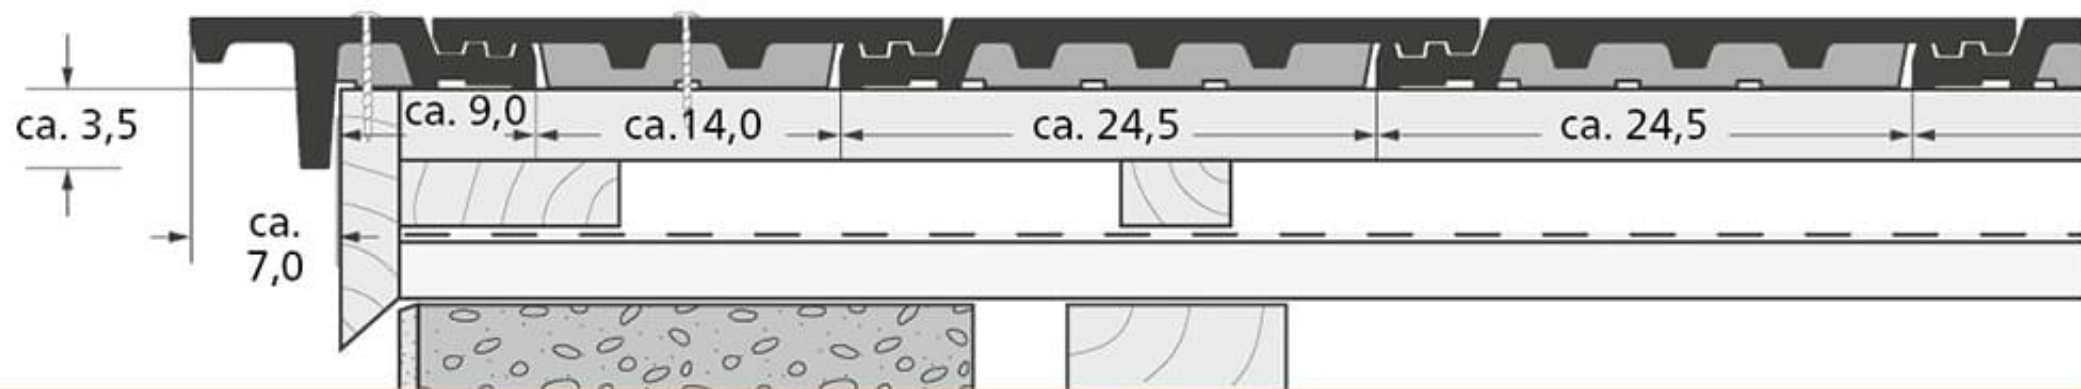


HALBER RECHTER ORTGANG*

* Um die halben Ortgänge auch bei flachen Dachneigungen regensicher fixieren zu können, werden die Level RS® Ortgänge durch die verstärkten kopfseitigen Aufhängenasen geschraubt. Hierbei kann je nach Holzquerschnitt ein Vorbohren der Latten notwendig werden.

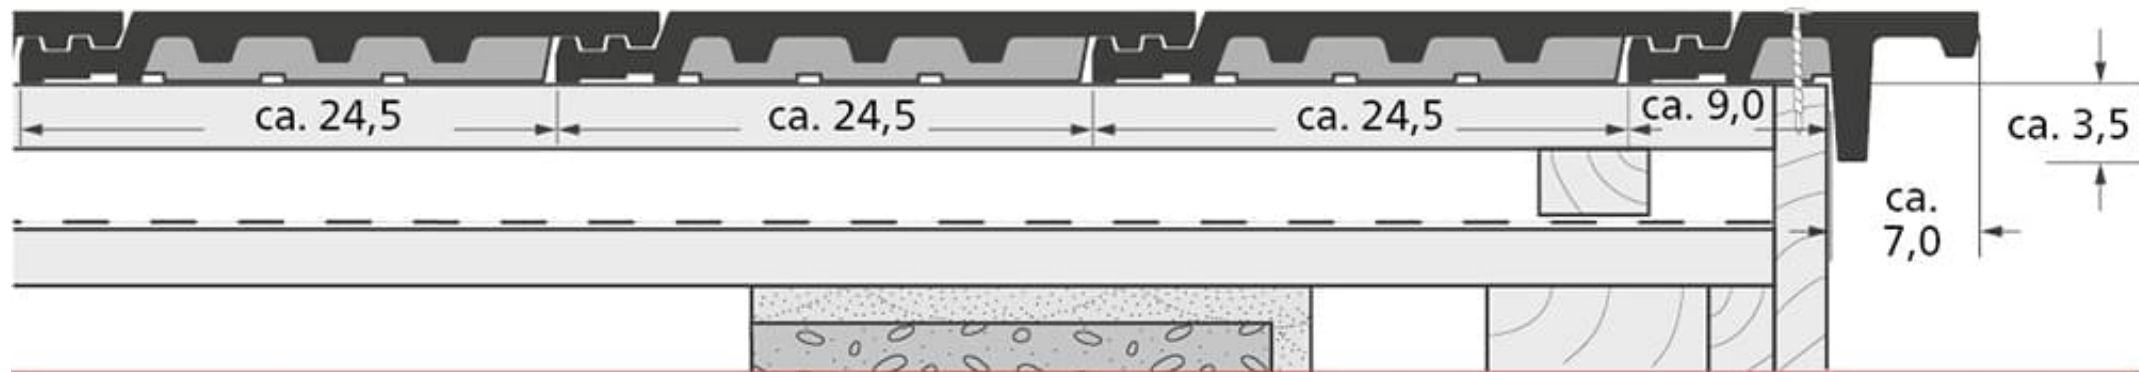

PULTDACH

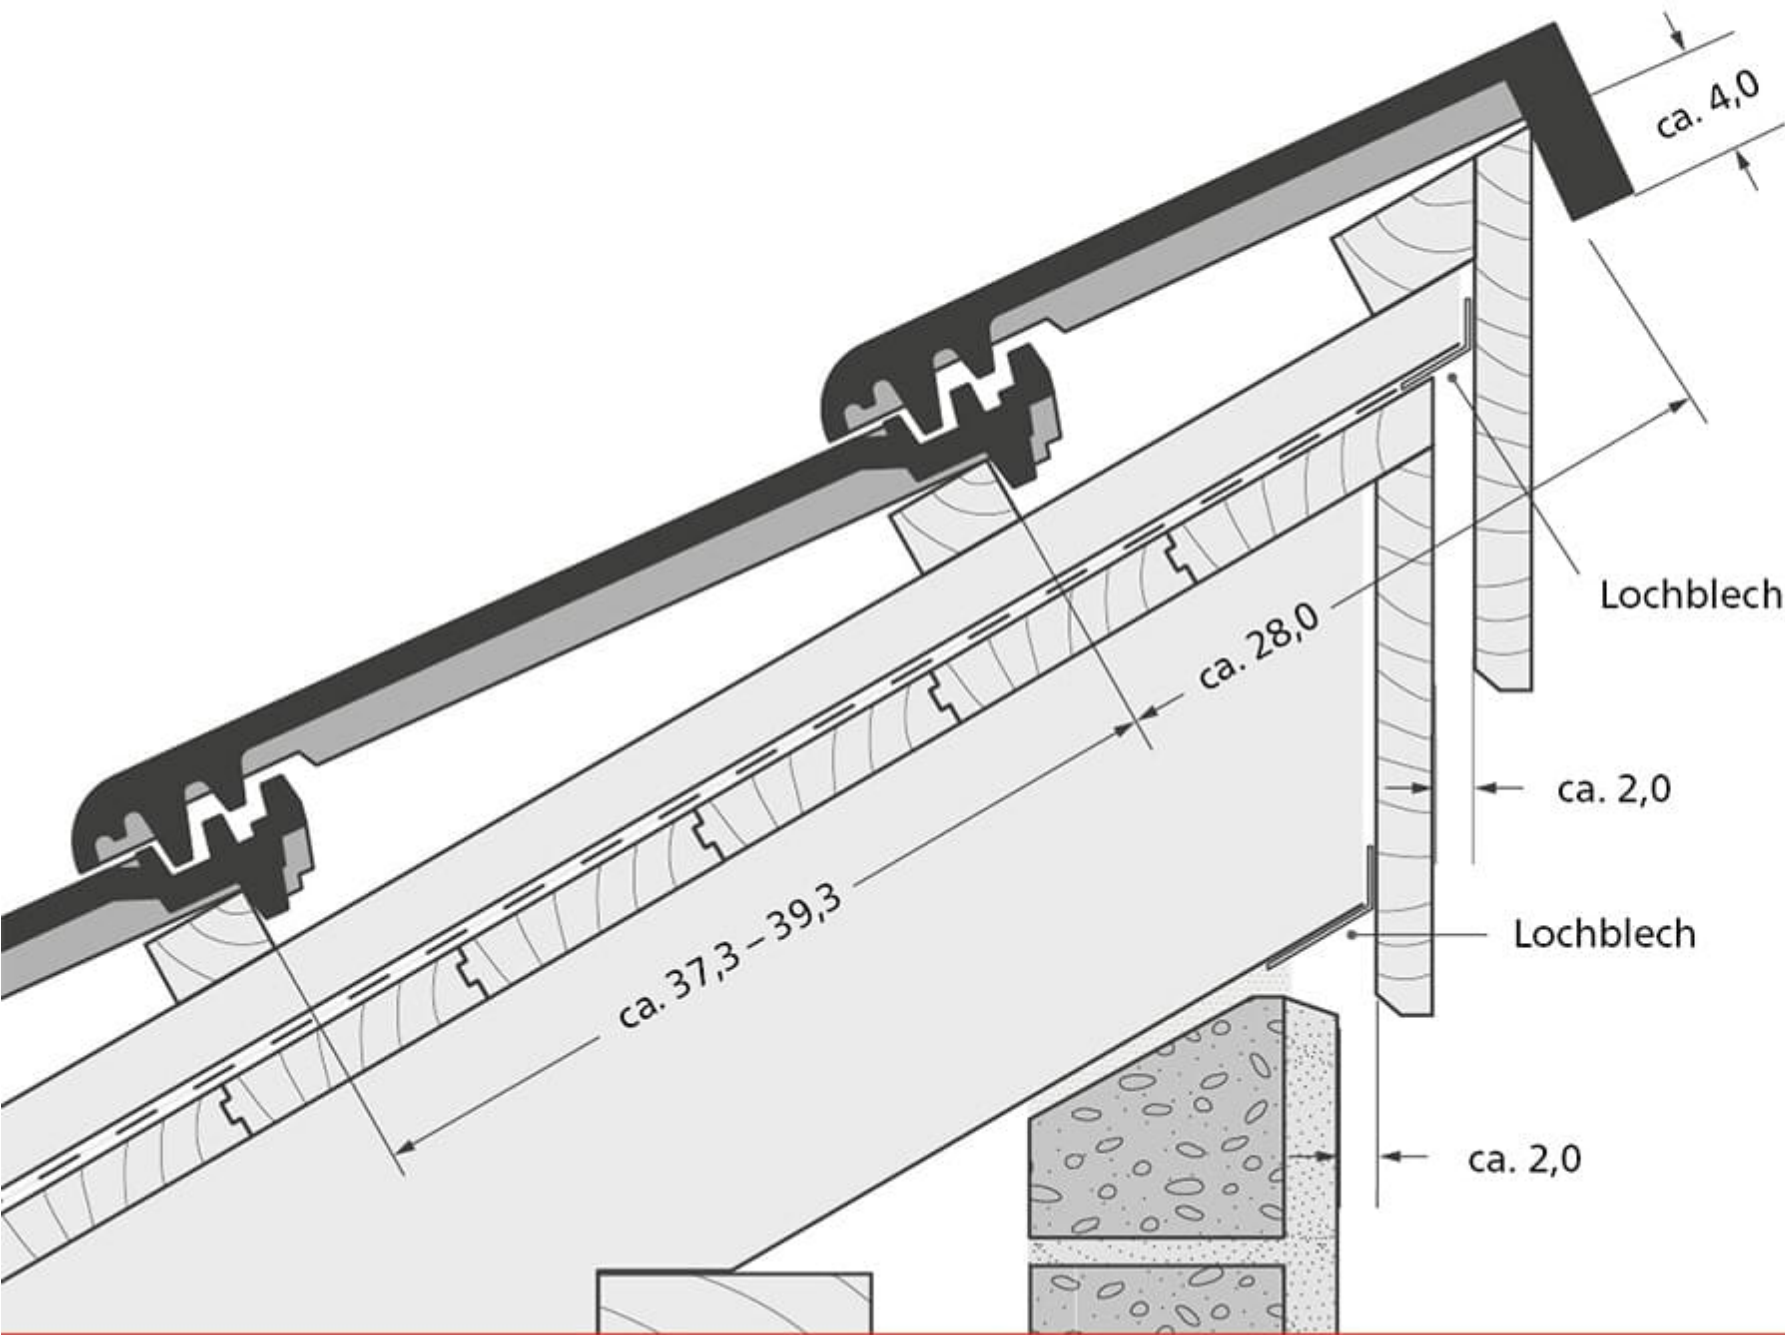

ÜBERSTEHENDE TRAUFE MIT AUFSPARRENDÄMMUNG

ERLUS empfiehlt den Einsatz eines Traufbleches.

