


FIRSTZIEGEL NR. 21 MIT FLÄCHENZIEGEL

ERLUS First- und Gratlüfterband aus Alu ist zur Erhöhung der Flugschneesicherheit notwendig.

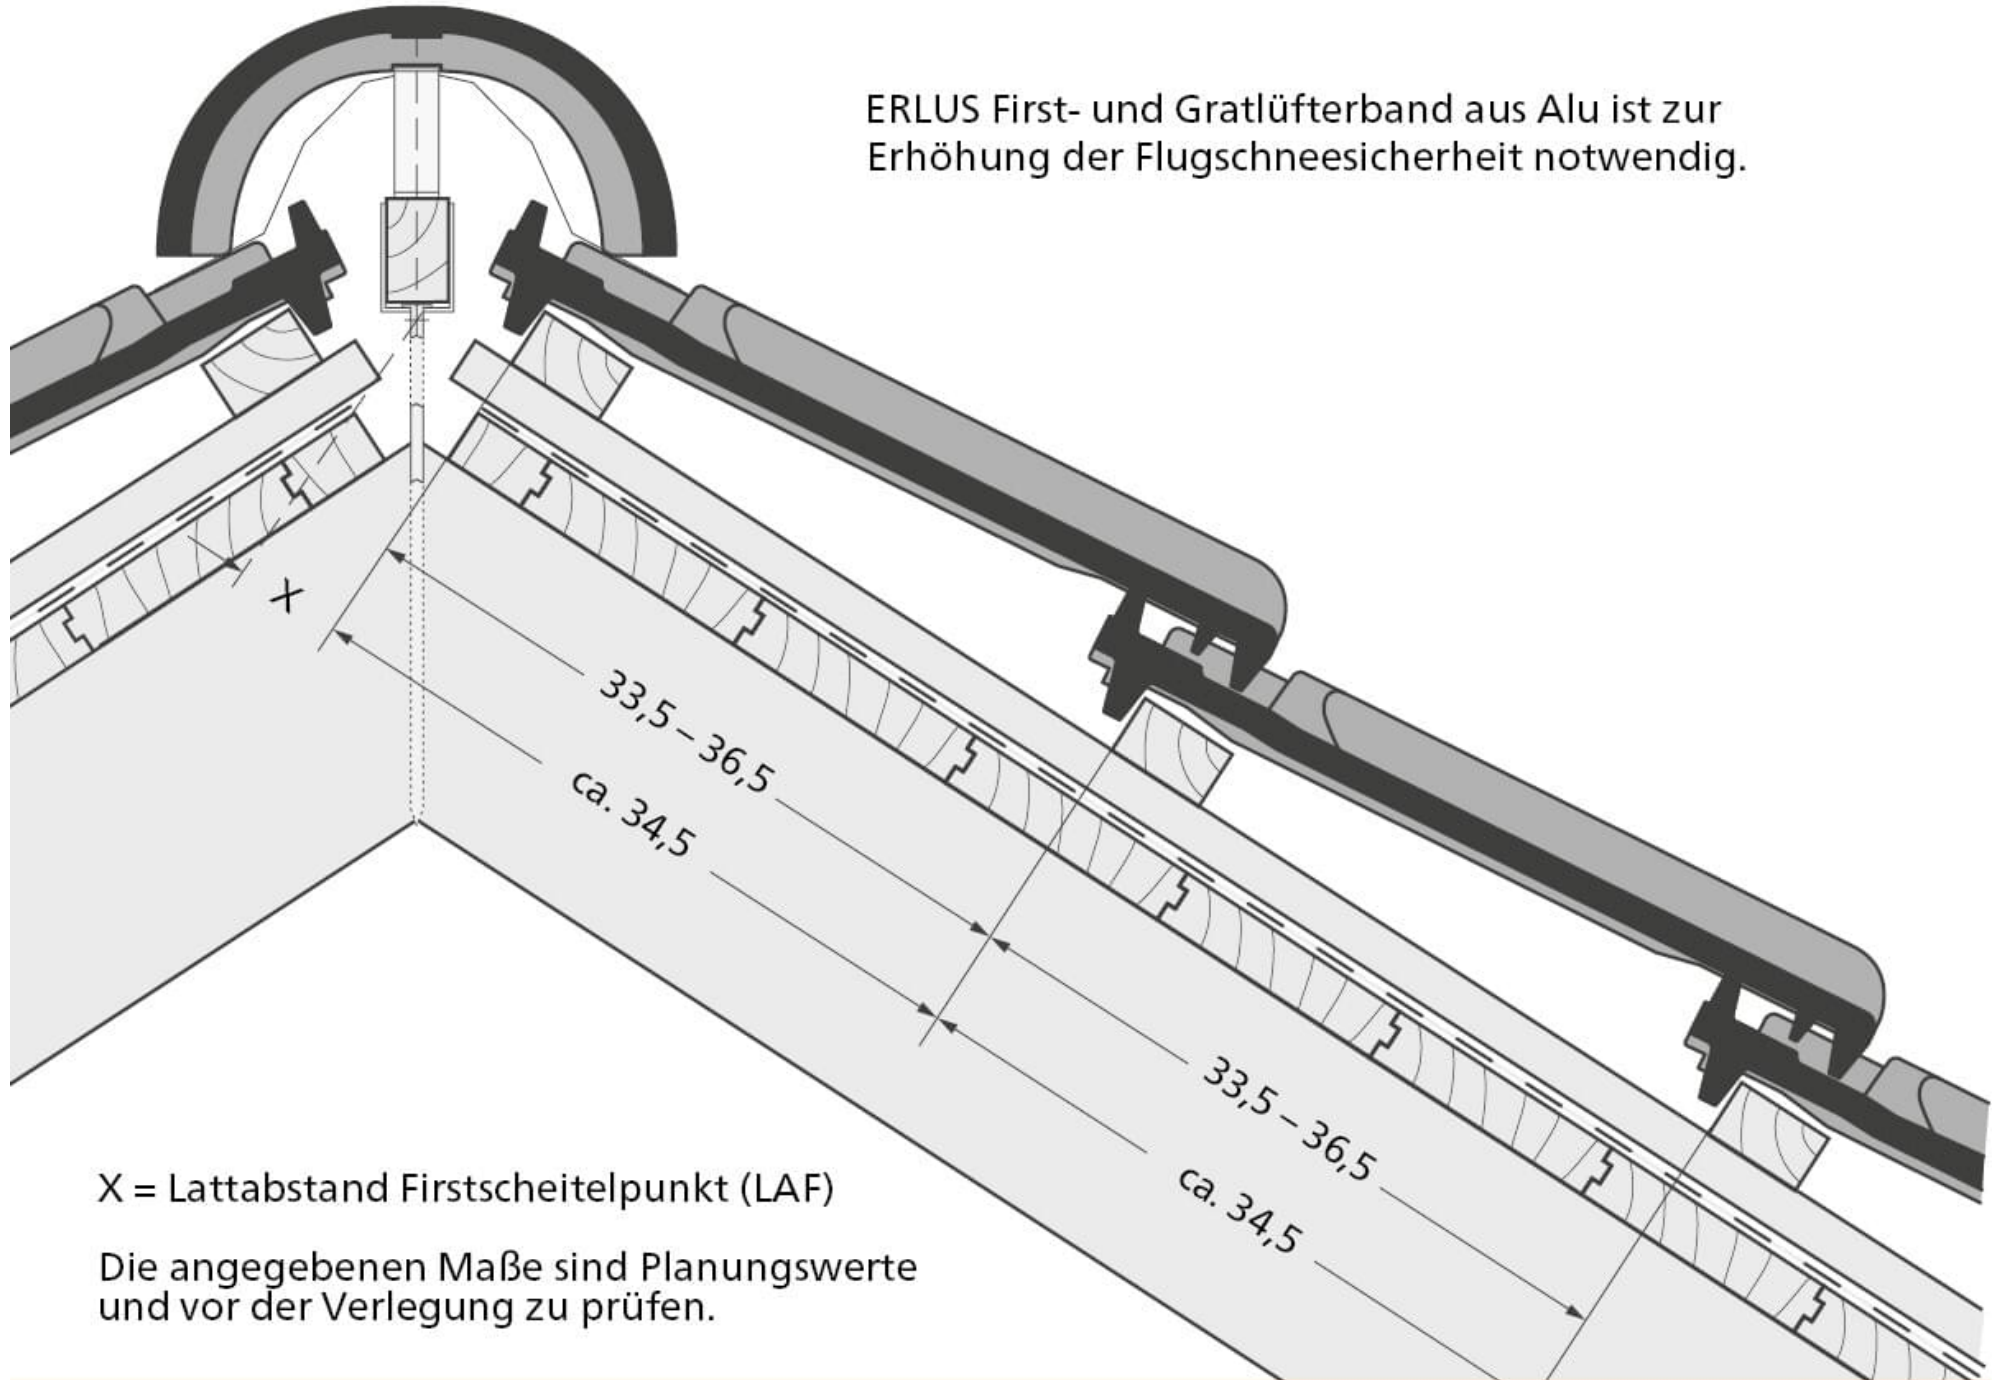


X = Lattabstand Firstscheitelpunkt (LAF)

Die angegebenen Maße sind Planungswerte und vor der Verlegung zu prüfen.

ERLUS Dachbegehungssystem

LATTWEITE < 37,5 cm

alle Maßangaben in cm

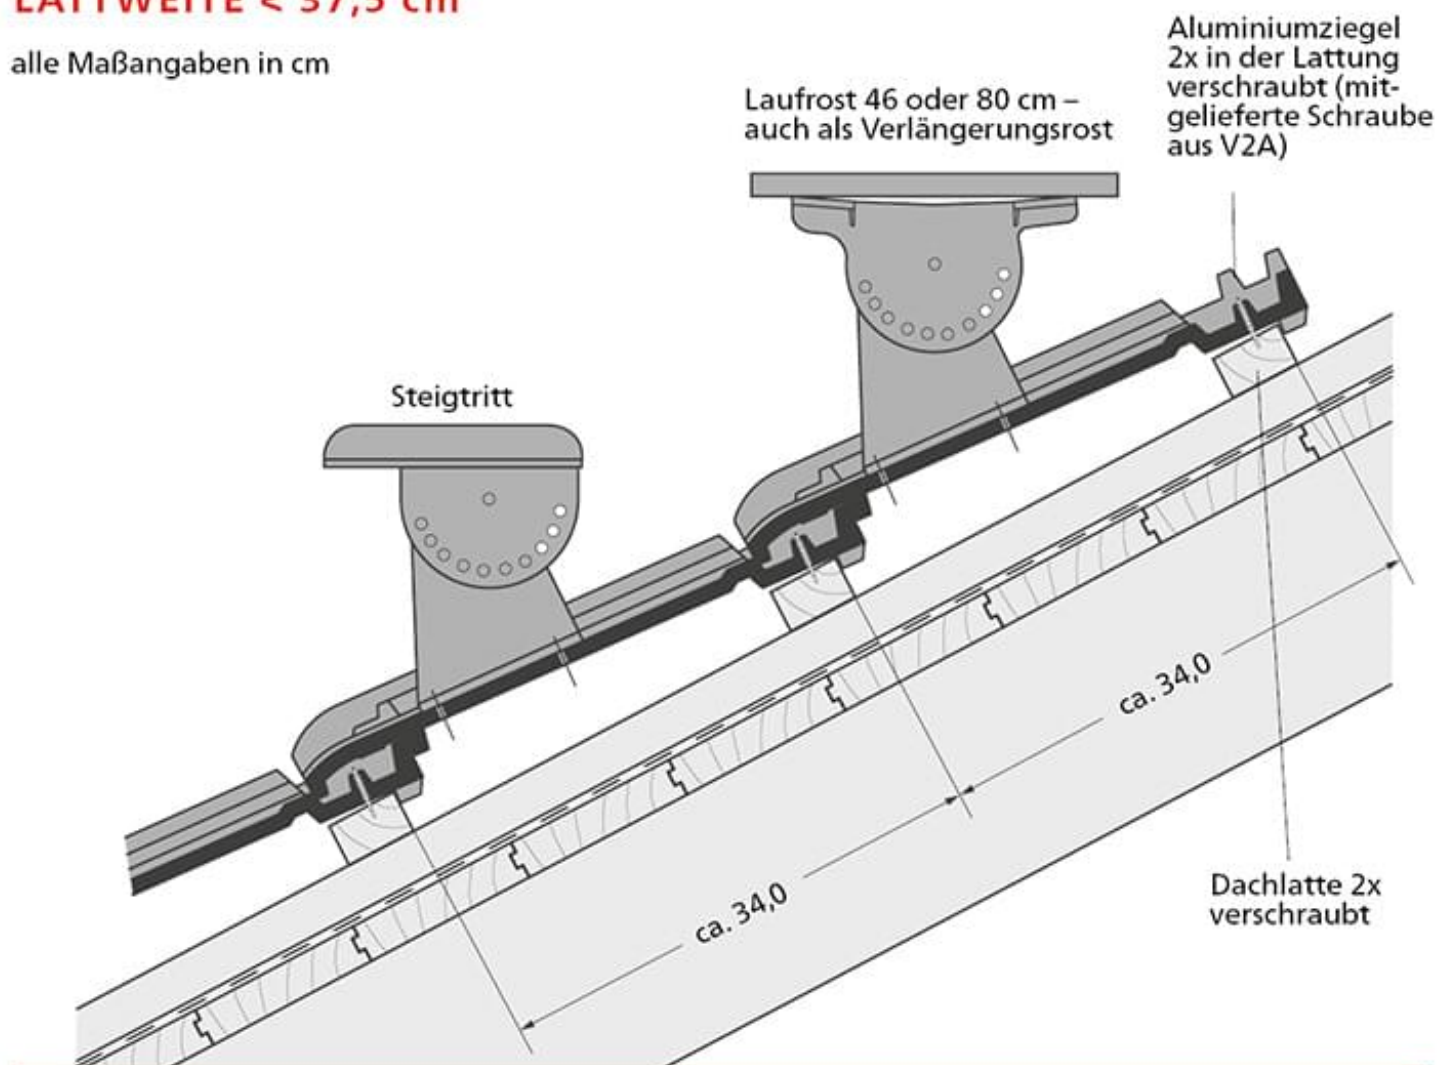

Zeichnung: E58

VERARBEITUNG VON TRITTFLÄCHEN UND ROSTEN NACH DIN 18160-5


ARTIKEL	$\leq 45^\circ$	$\geq 45^\circ$
Trittflächen (Roste 46 cm)	jede 2. Ziegelreihe	jede Ziegelreihe
Einzeltritt (Steigtritt)	jede Ziegelreihe	jede Ziegelreihe

aus nicht rostendem Stahl/Alu, geprüft nach DIN EN 516,

keine Stützlaten erforderlich


LINKER ORTGANG*

*bei flacher Dachneigung Verschraubungsloch im Ortgang dauerelastisch
(z. B. mit Spenglerschrauben) abdichten

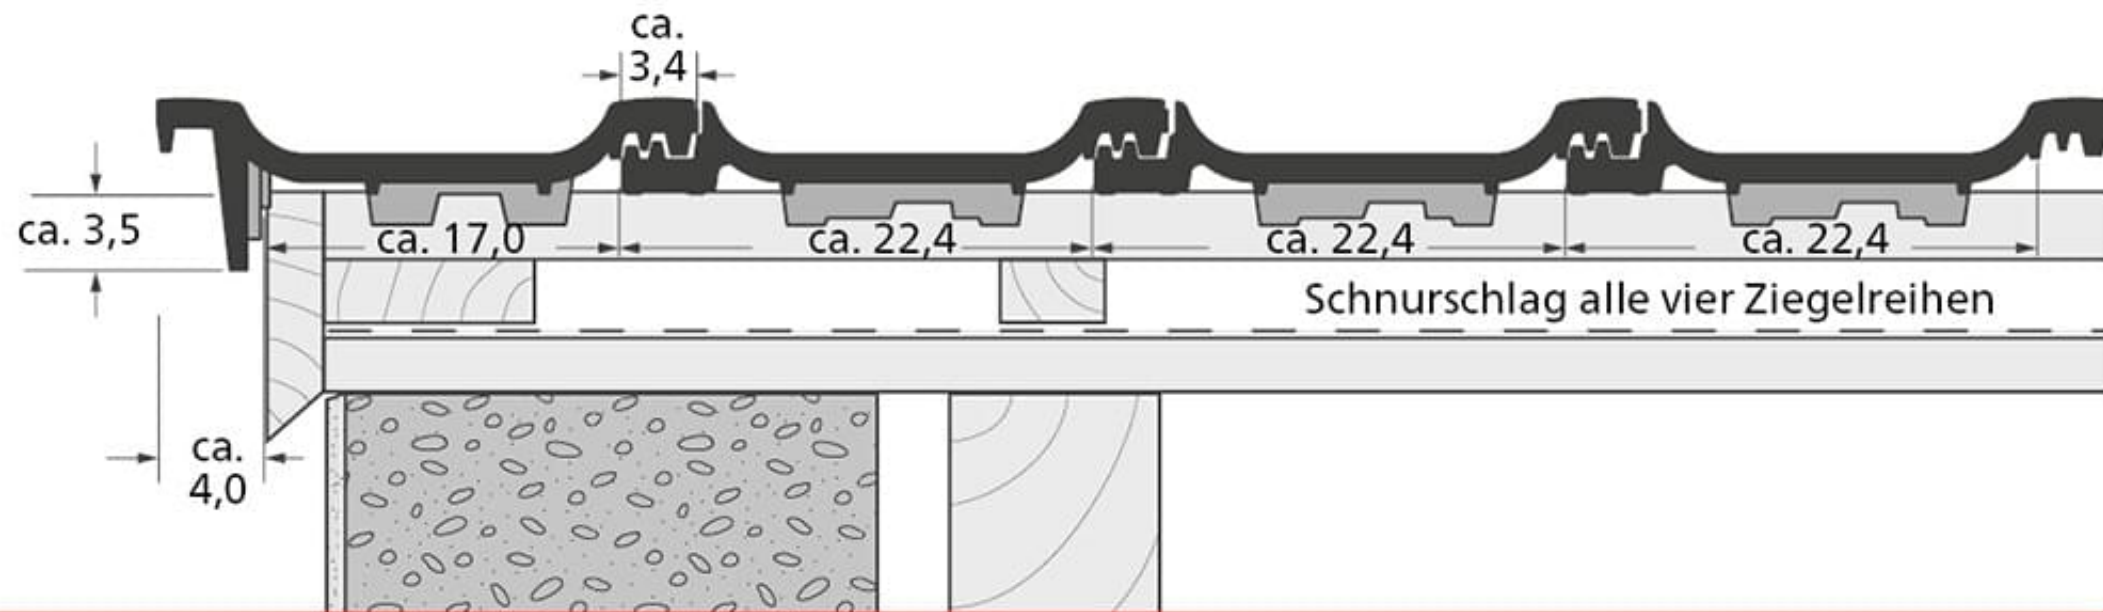


RECHTER ORTGANG*

*bei flacher Dachneigung Verschraubungsloch im Ortgang dauerelastisch
(z. B. mit Spenglerschrauben) abdichten

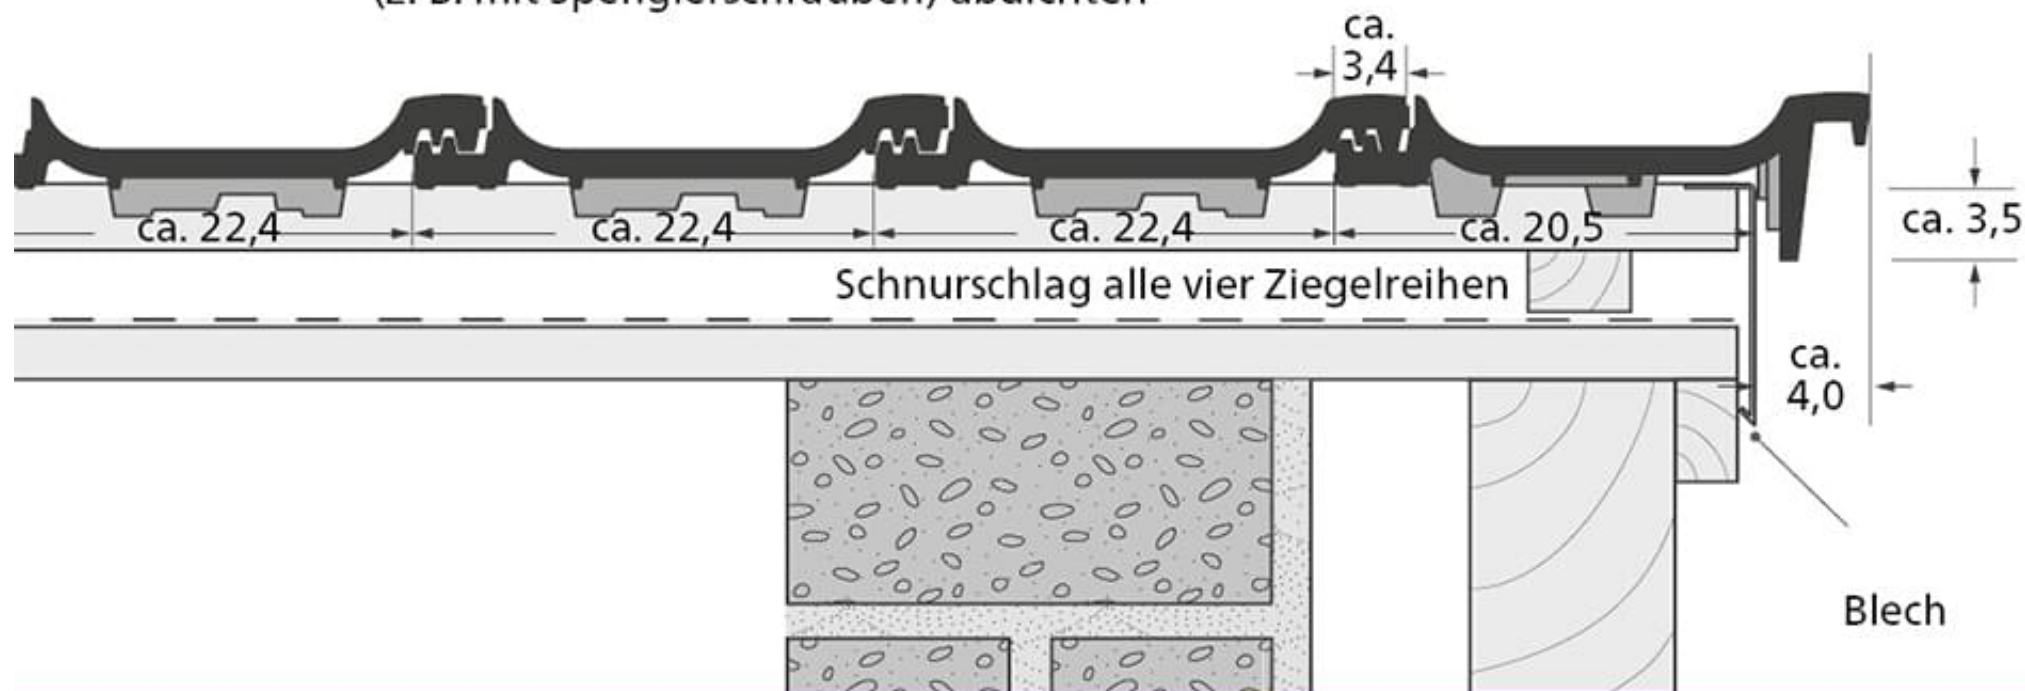

TRAUFE

ERLUS empfiehlt den Einsatz eines Traufbleches.

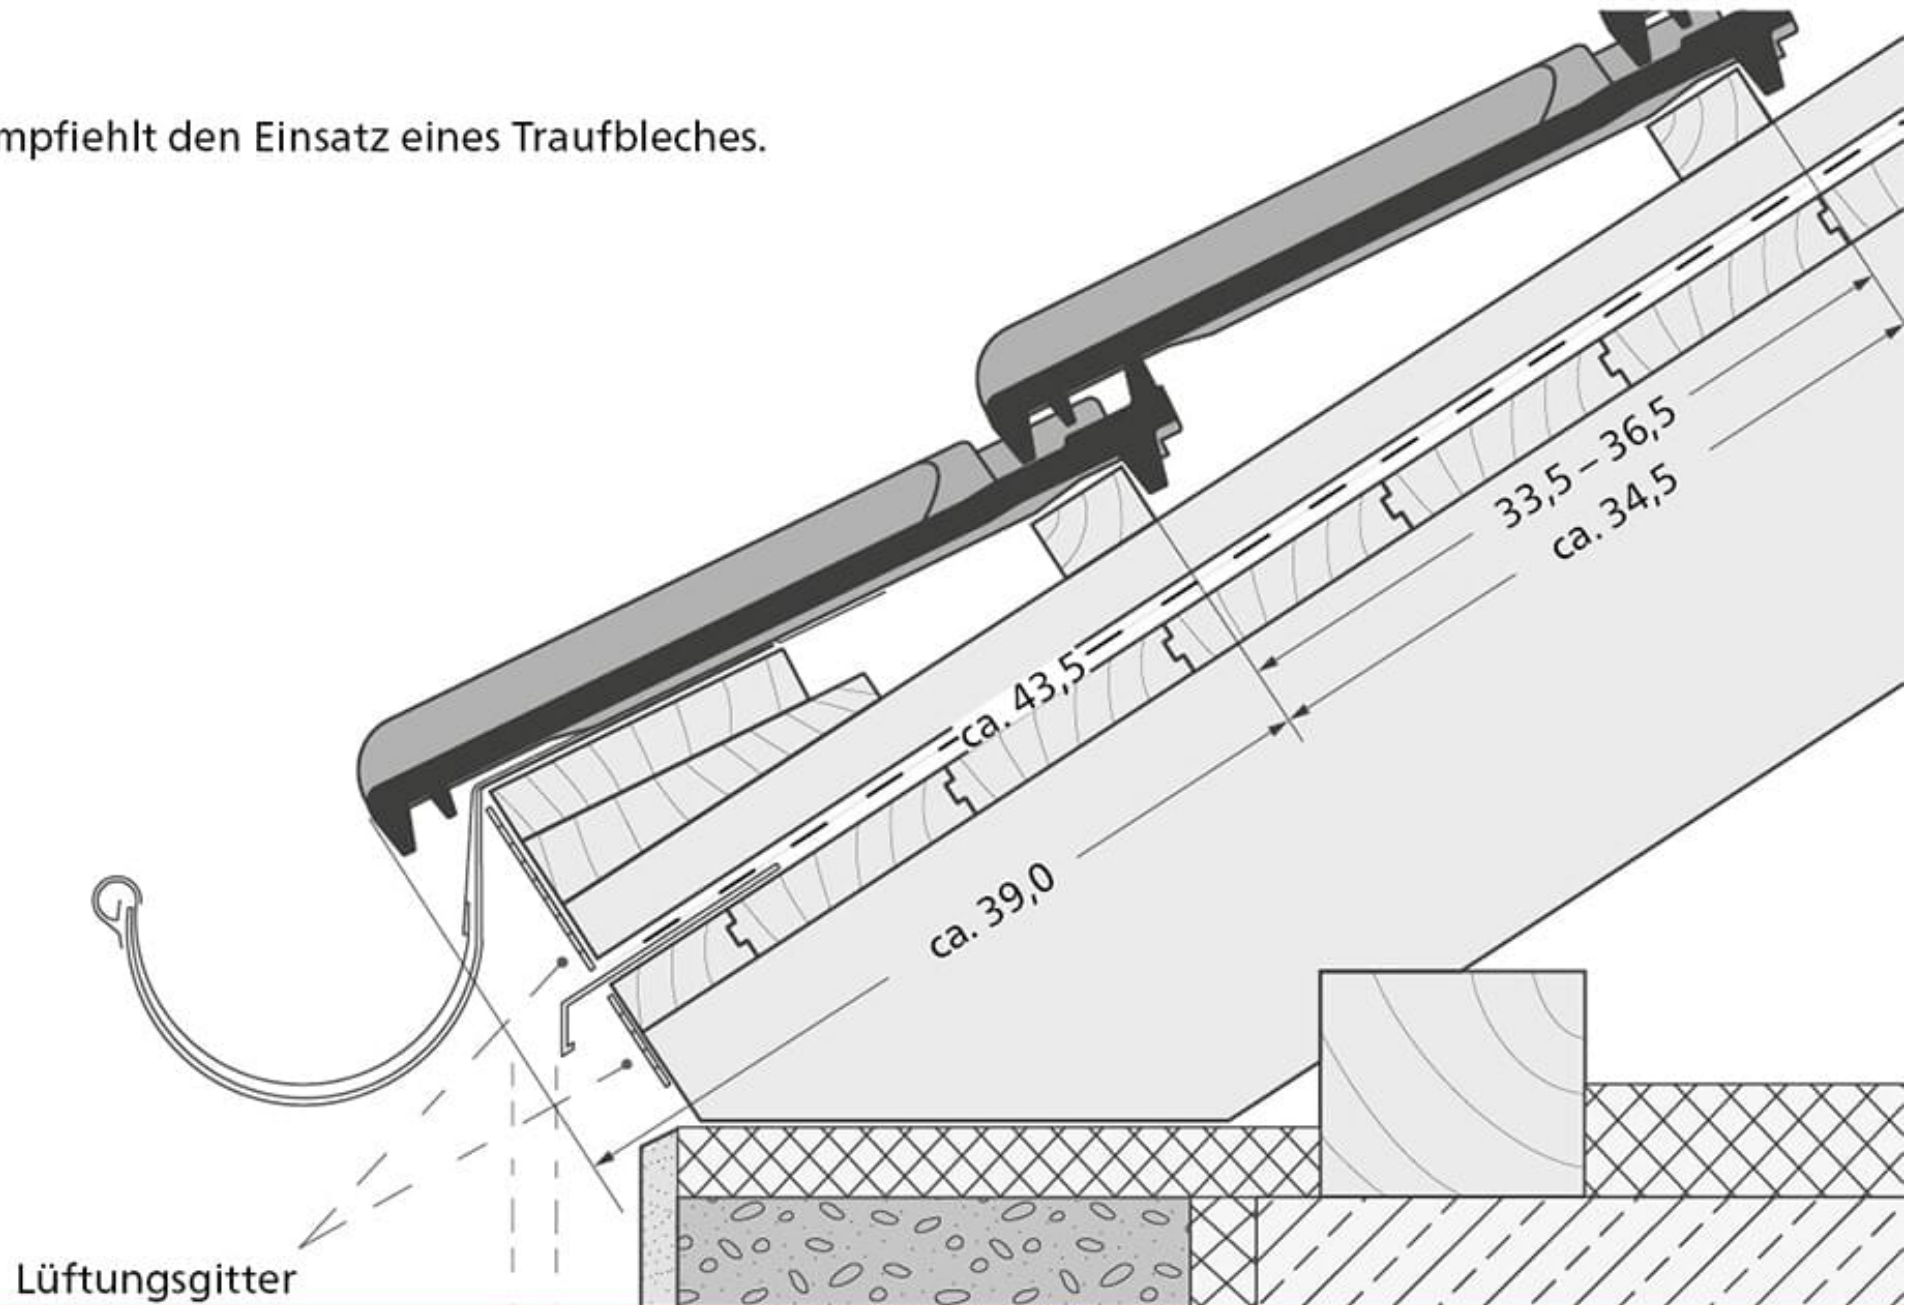

TRAUFE MIT ENTWÄSSERTEM UNTERDACH

ERLUS empfiehlt den Einsatz eines Traufbleches.

