


FIRSTZIEGEL NR. 18 MIT FLÄCHENZIEGEL

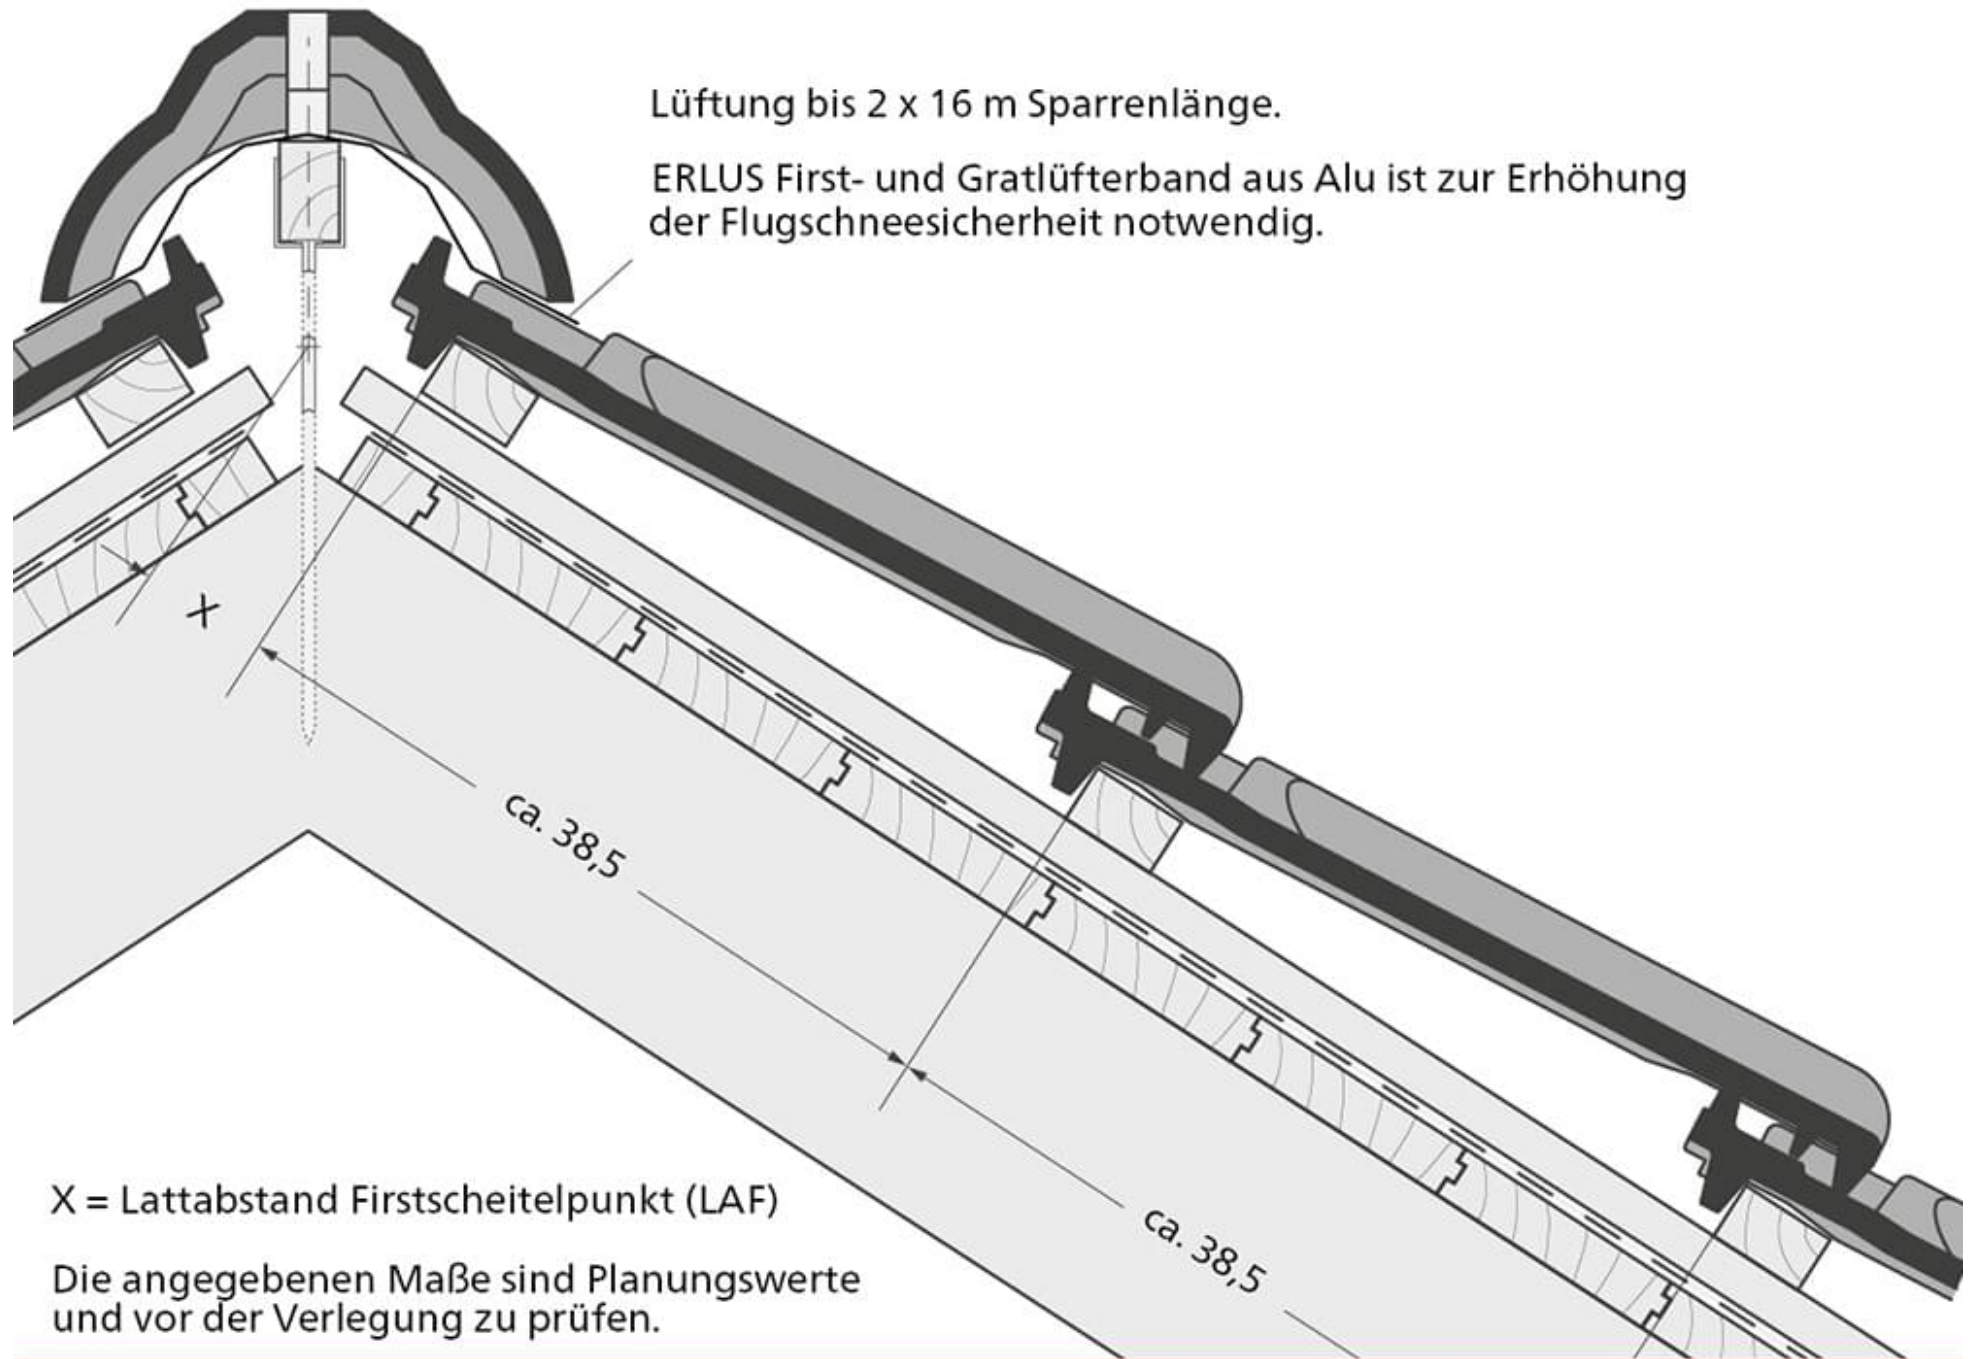


FIRSTLÜFTERZIEGEL NR. 19 LÜ

Firstziegel: 2,8 Stck./lfm.

Firstanfangsziegel

Hauptwetterrichtung

Firstendziegel

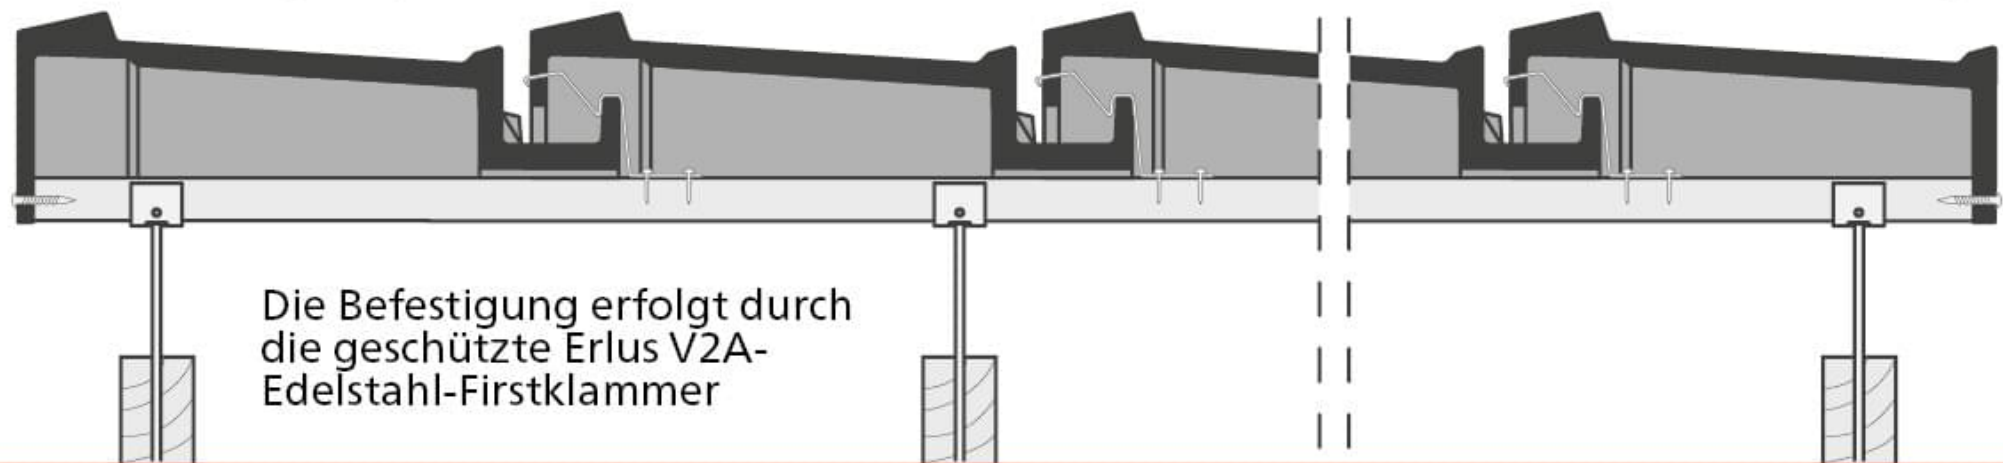


Die Befestigung erfolgt durch die geschützte Erlus V2A-Edelstahl-Firstklammer

FIRSTZIEGEL NR. 18

Firstabschlussziegel
Nr. 18 geschnitten

Firstausgleichsziegel Nr. 18

Firstziegel Nr. 18
2,6 Stck./lfm.

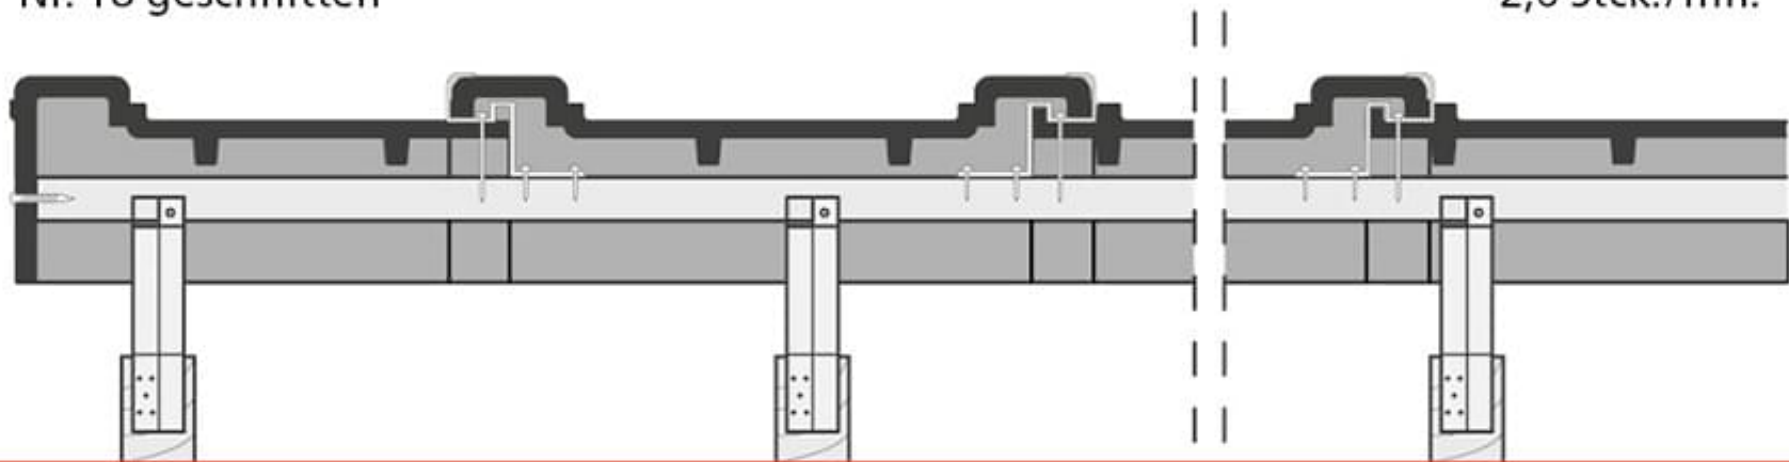

LINKER ORTGANG*


*bei flacher Dachneigung Verschraubungsloch im Ortgang dauerelastisch
(z. B. mit Spenglerschrauben) abdichten



RECHTER ORTGANG*


*bei flacher Dachneigung Verschraubungsloch im Ortgang dauerelastisch
(z. B. mit Spenglerschrauben) abdichten

1/2 Großfalzziegel XXL nur zum Breitenausgleich
von kleinen Dachflächen (Gauben)

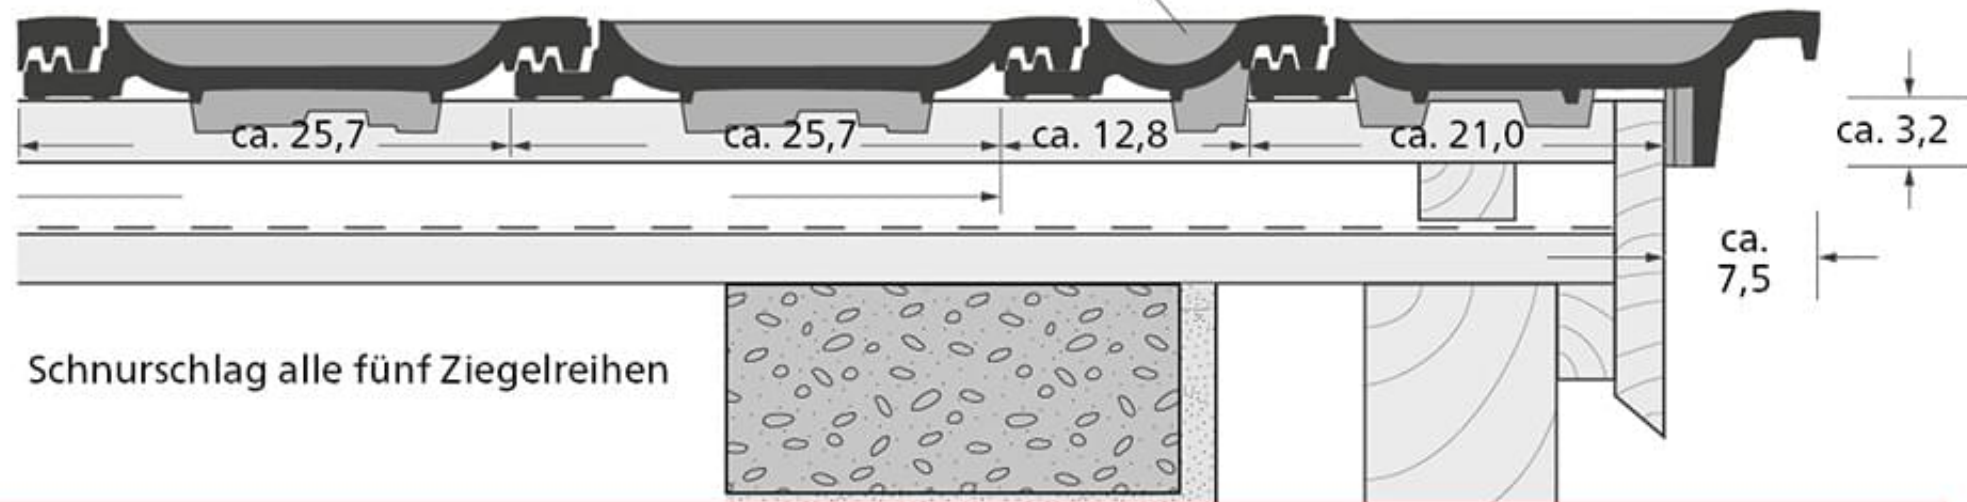

TRAUFE

ERLUS empfiehlt den Einsatz eines Traufbleches.

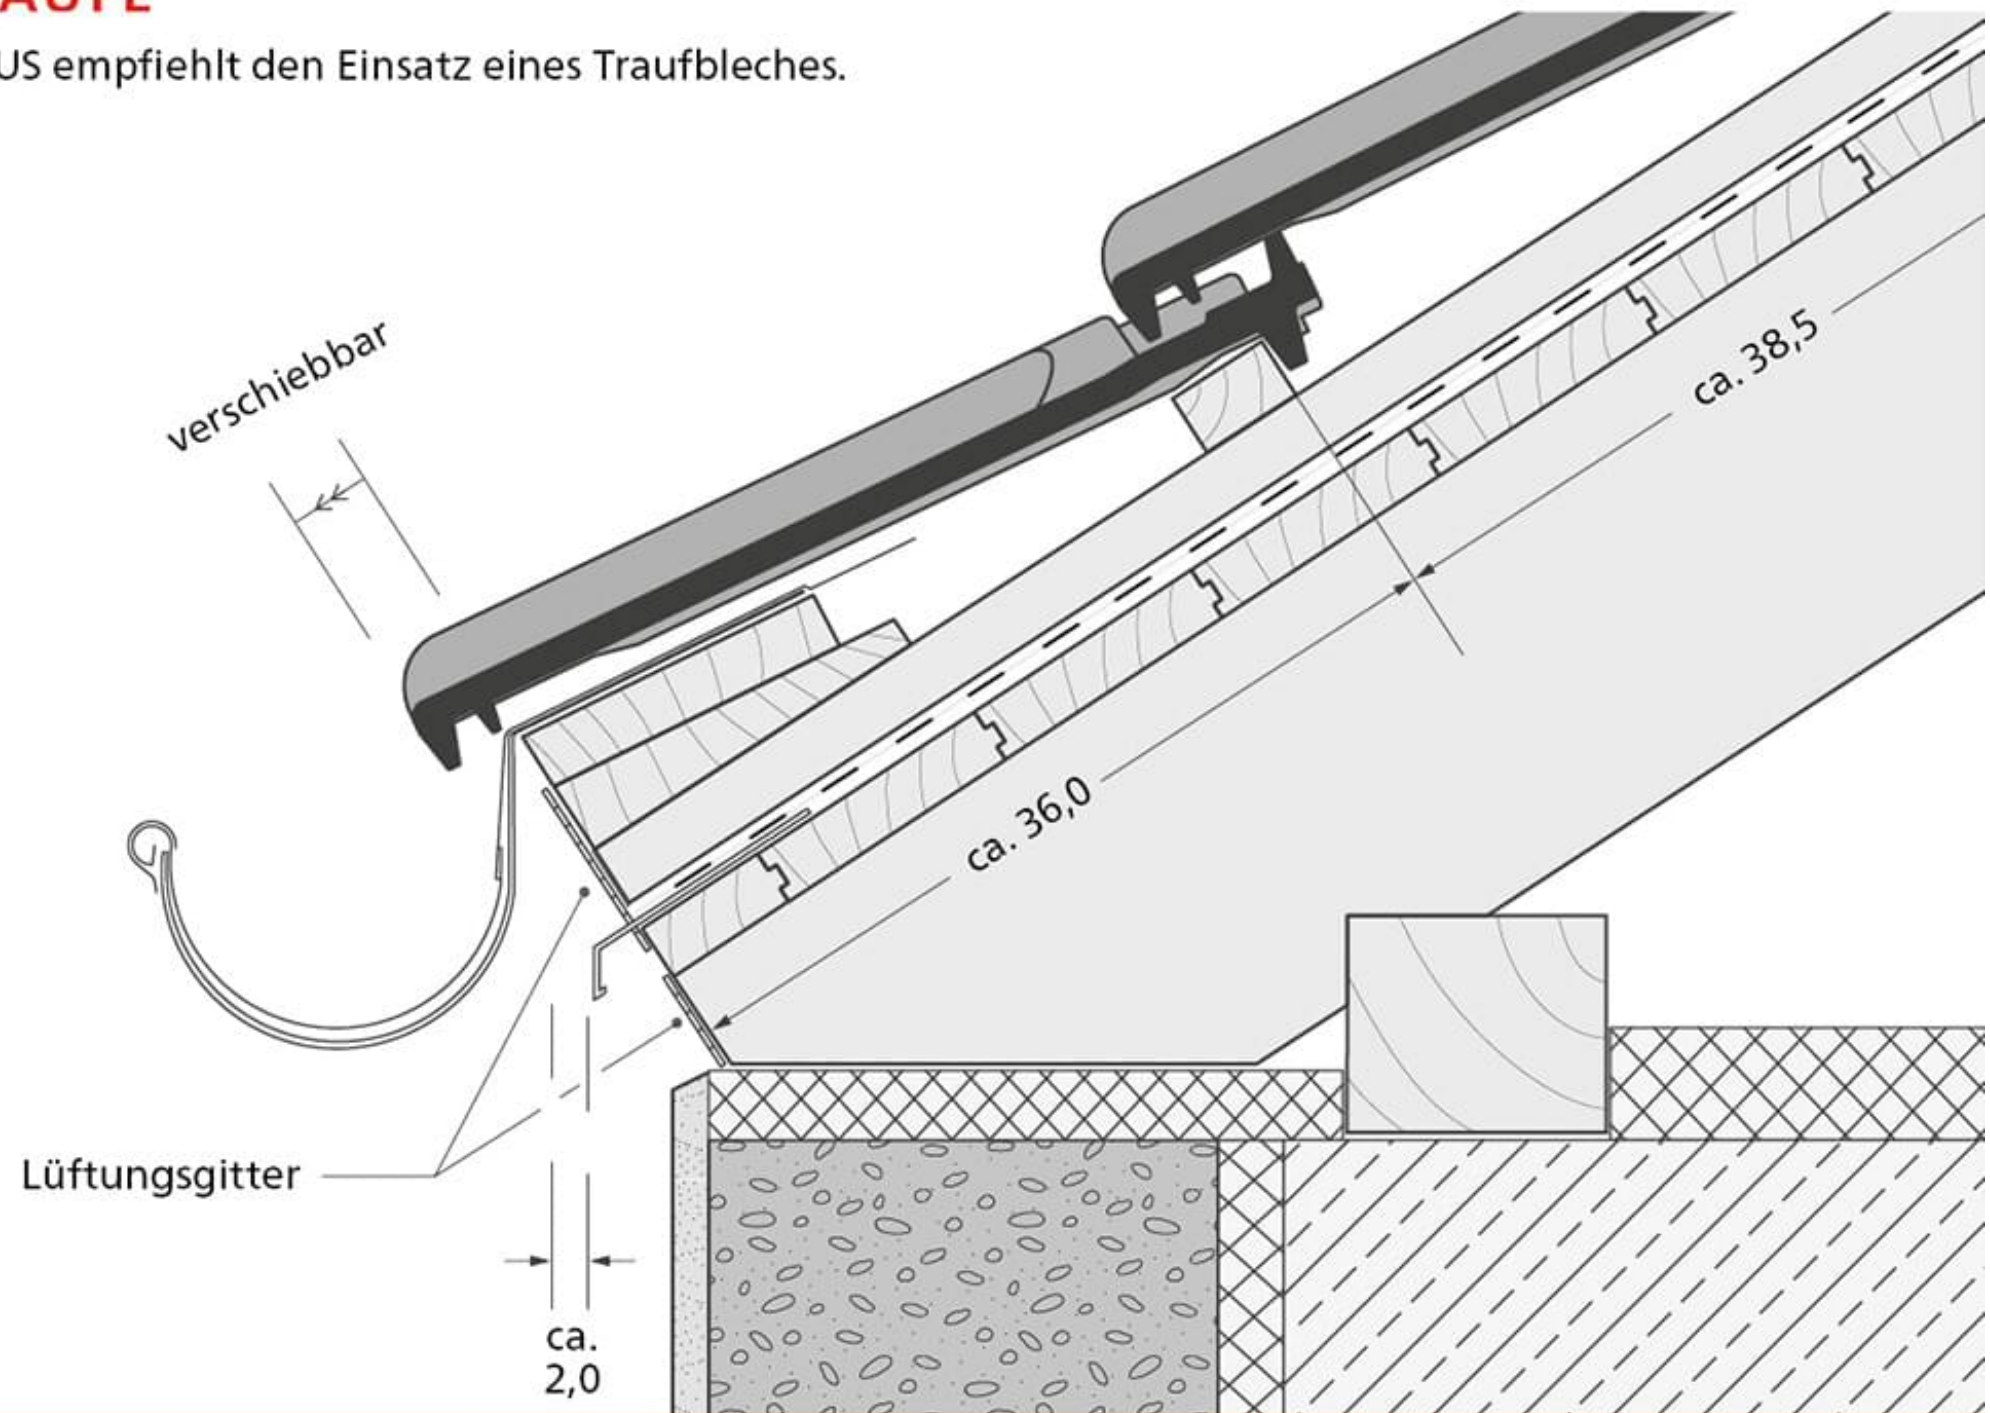

TRAUFE MIT ENTWÄSSERTEM UNTERDACH

ERLUS empfiehlt den Einsatz eines Traufbleches.

