


# ERLUS Dachbegehungssystem

## LATTWEITE < 37,5 cm

alle Maßangaben in cm

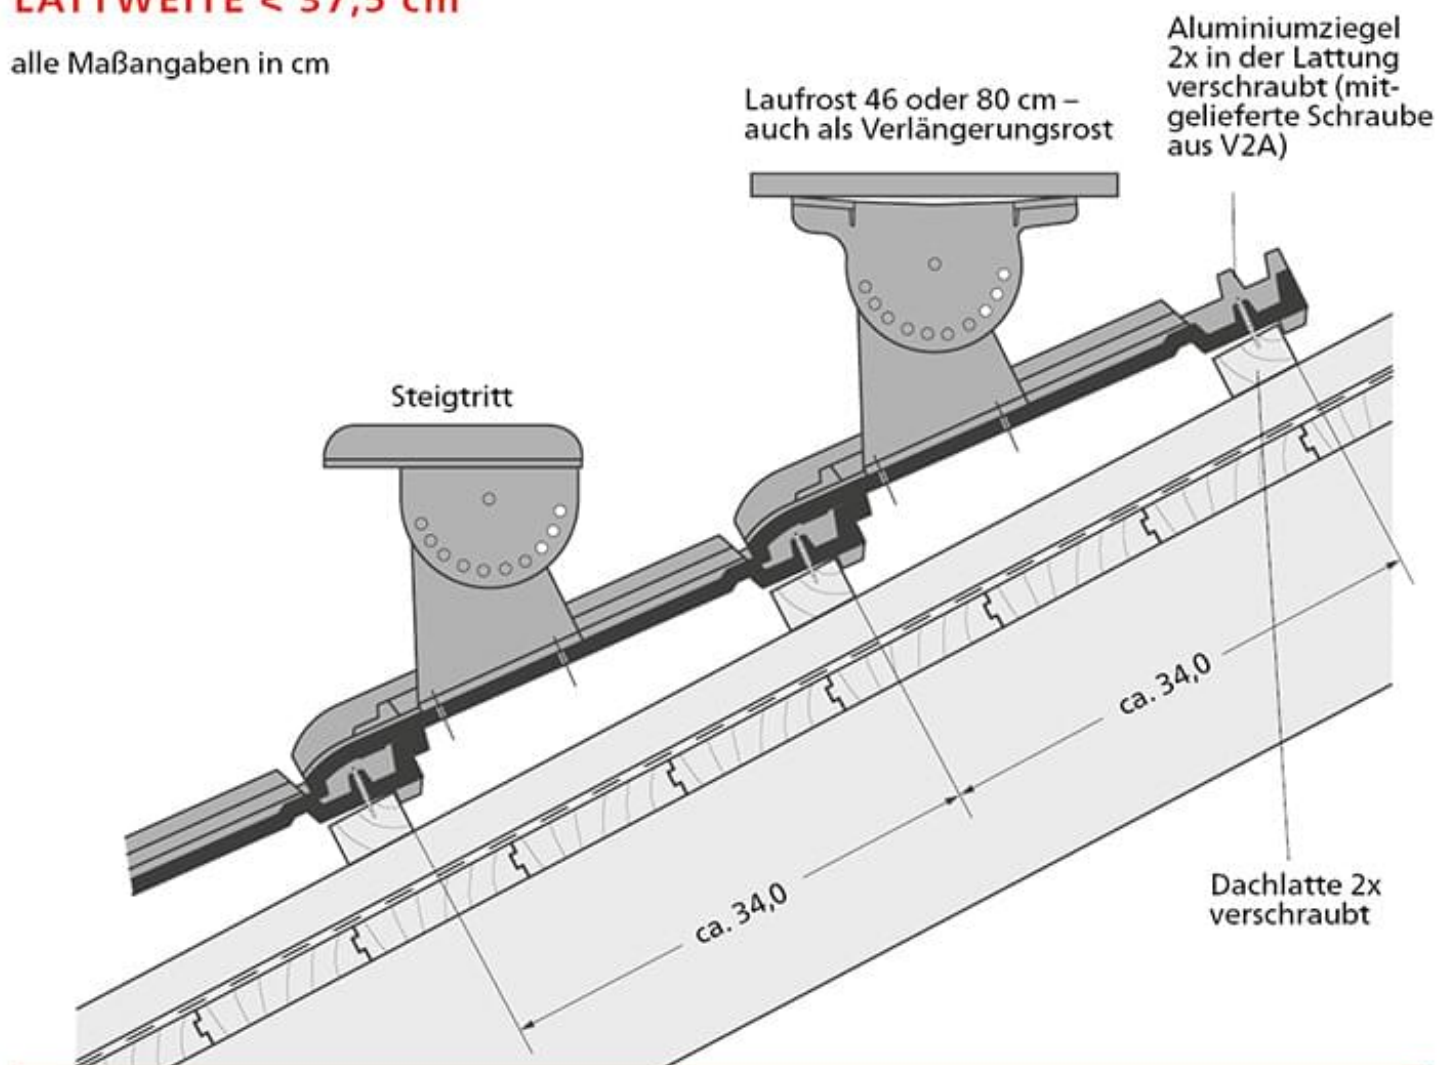

Zeichnung: E58

### VERARBEITUNG VON TRITTFLÄCHEN UND ROSTEN NACH DIN 18160-5


| ARTIKEL                    | $\leq 45^\circ$     | $\geq 45^\circ$  |
|----------------------------|---------------------|------------------|
| Trittflächen (Roste 46 cm) | jede 2. Ziegelreihe | jede Ziegelreihe |
| Einzeltritt (Steigtritt)   | jede Ziegelreihe    | jede Ziegelreihe |

aus nicht rostendem Stahl/Alu, geprüft nach DIN EN 516,

keine Stützlatte erforderlich


## ORTGANG – VERLEGEHINWEIS

Liegt die Decklänge unter 33 cm, müssen die Ortgang-Krempen im oberen Teil abgetrennt werden

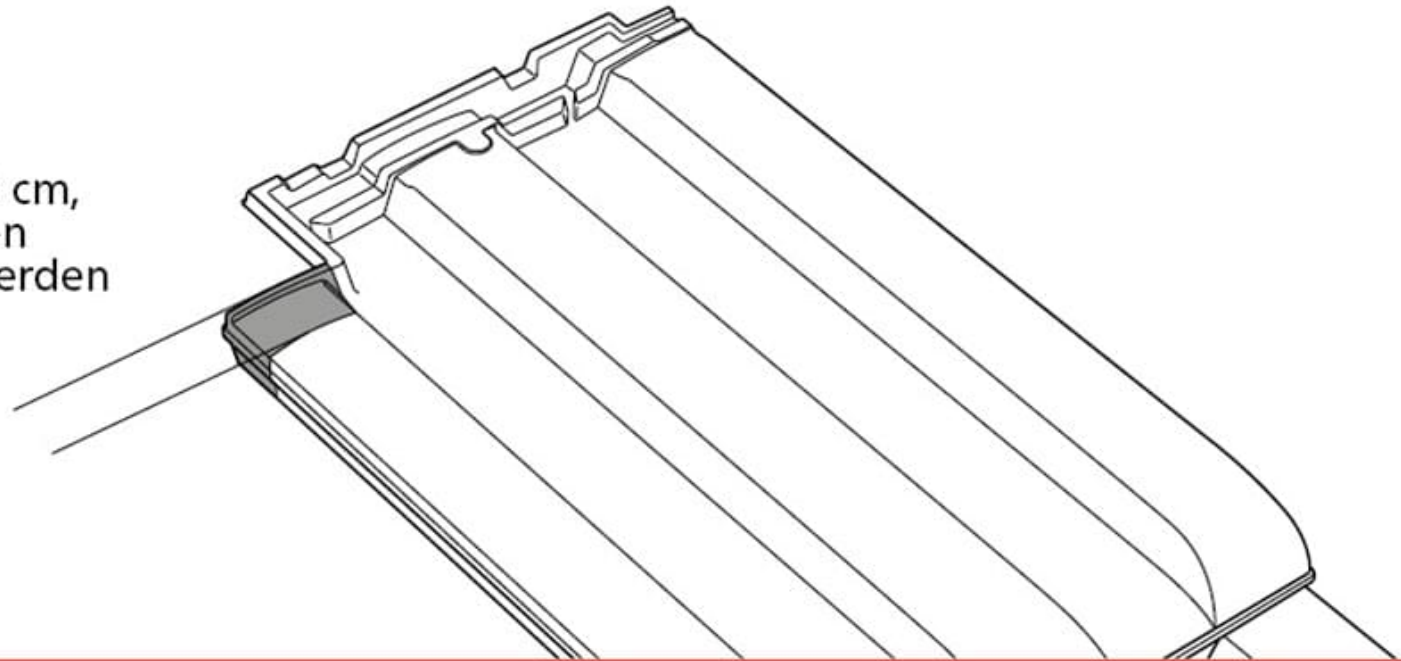

## LINKER ORTGANG\*

\*bei flacher Dachneigung Verschraubungsloch im Ortgang dauerelastisch  
(z. B. mit Spenglerschrauben) abdichten

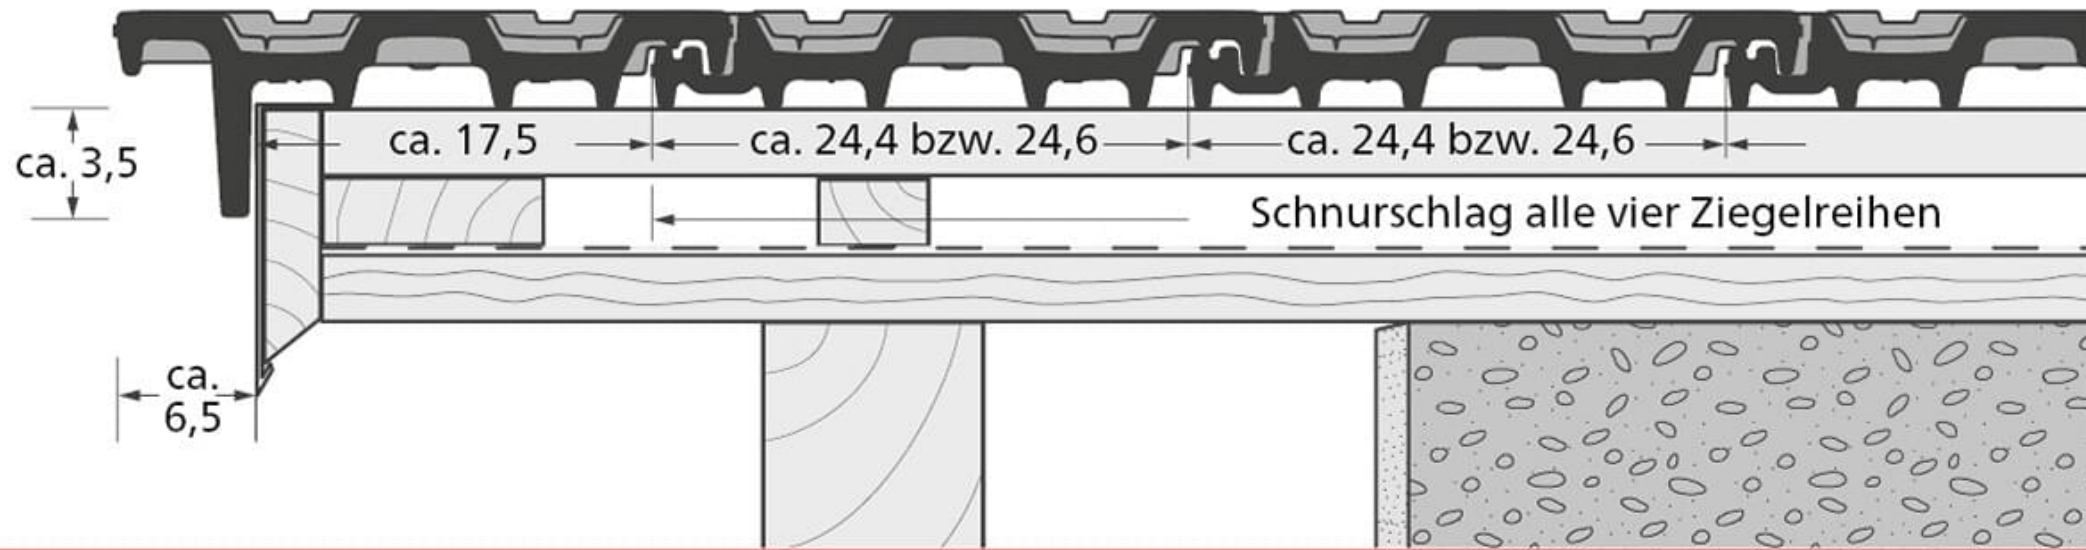


## RECHTER ORTGANG\*

\*bei flacher Dachneigung Verschraubungsloch im Ortgang dauerelastisch  
(z. B. mit Spenglerschrauben) abdichten



# TRAUFE MIT ENTWÄSSERTEM UNTERDACH

ERLUS empfiehlt den Einsatz eines Traufbleches.

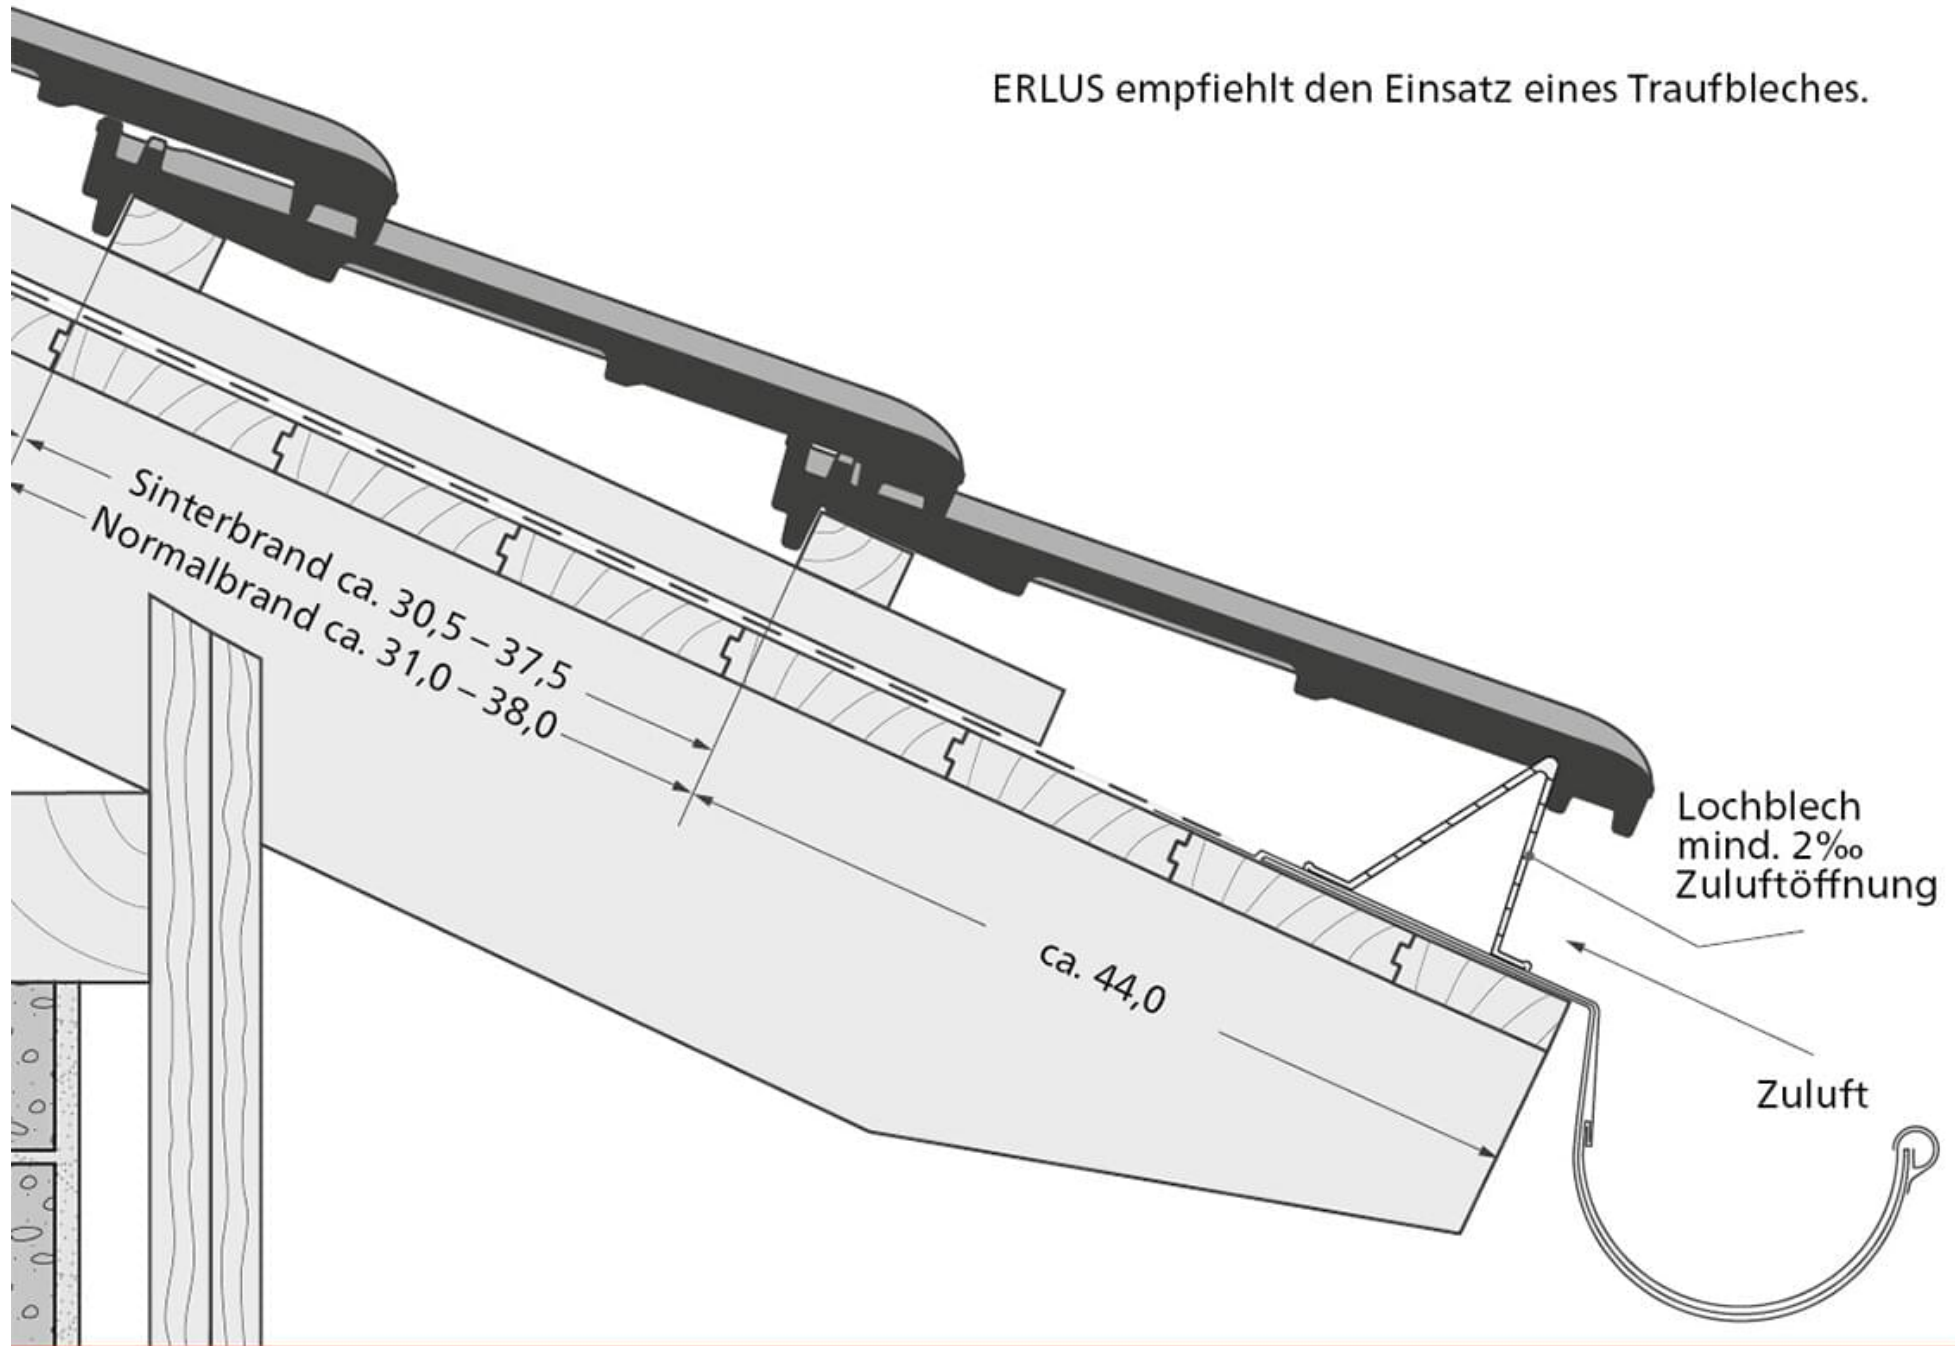



# TRAUFE MIT AUFSPARRENDÄMMUNG

ERLUS empfiehlt den Einsatz eines Traufbleches.

